




P O R T F O L I O

A B I A R E V A L O

F A L L 2 0 2 5
S P R I N G 2 0 2 6

I N T R O D U C T I O N

This portfolio presents a selection of my architectural work and creative explorations as a first-year architecture student. My projects focus on transforming emotions, memories, and artistic inspiration into spatial experiences through design, form, and atmosphere. Both semesters have their own backgrounds and show how they evolved from ideas to buildings that are useful for people.

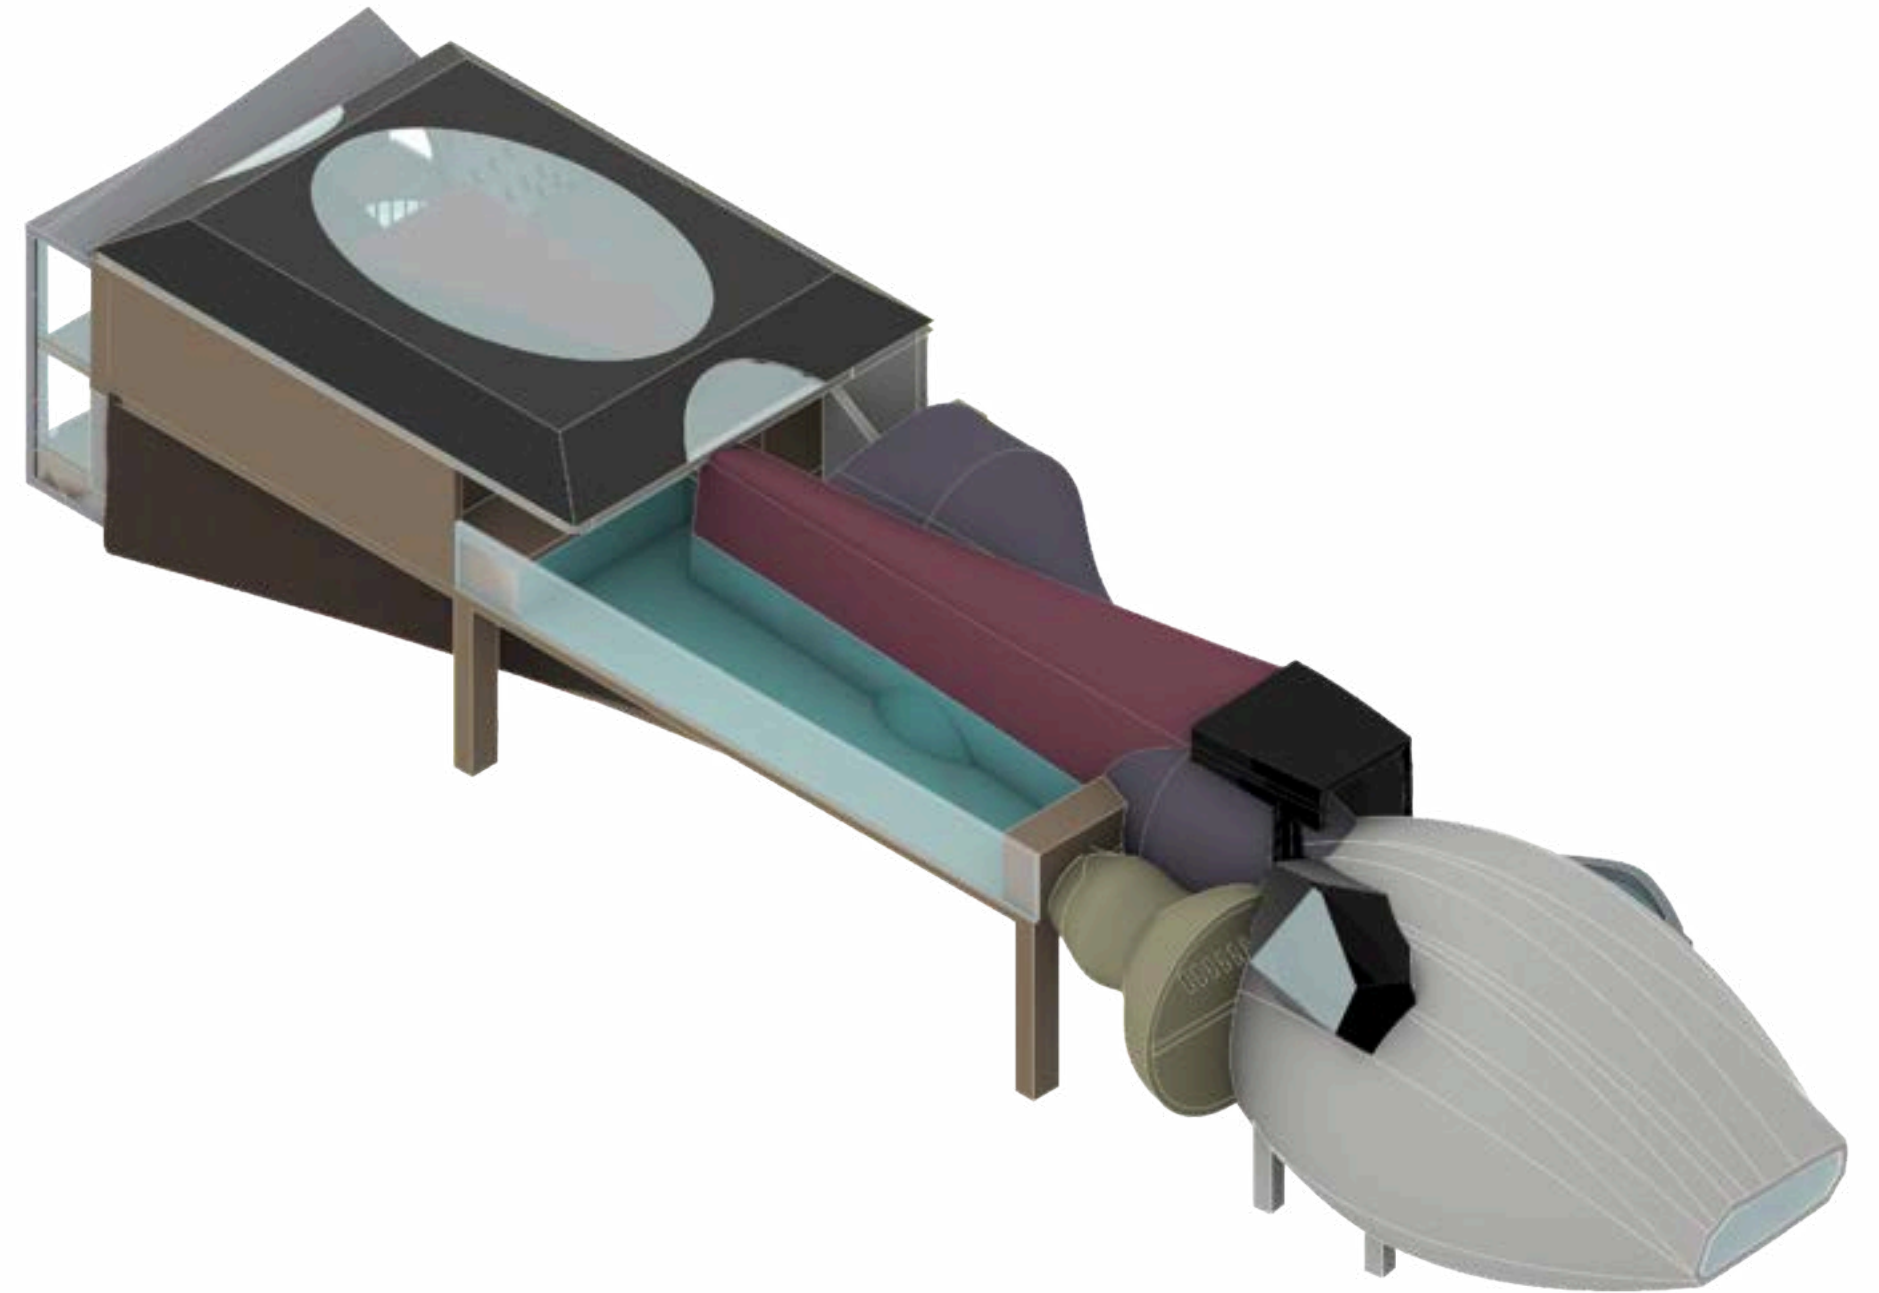

CONTENT

1ST SEMESTER



- DIGITAL/PHYSICAL FOLDED CUBES WITH ORTHOGONALLY DRAWN LINE PATHS
- DIGITAL VOLUMES
- DIGITAL EXPLODED ISOMETRIC OF THE CUBES
- DIAGRAMS & MODELS OF HORIZON & SKY VOLUMES
- FIRST PHYSICAL MODEL
- ENVIRONMENTAL ENCLOSURES
- TAXONOMY
- FLOOR PLANS / SECTIONS
- CIRCULATION
- TRANSITIONAL CLEANSING
- MATERIALIZED SPACES (ISOMETRIC)

2ND SEMESTER



- NARRATIVE
- PAINTING TRACING + ELEMENTS
- SCENE 1
- SCENE 2
- SCENE 3
- GRID OF VOLUMES
- VOLUMETRIC SCENES
 - 1 - 2 - 3
- SPATIAL NARRATIVE 1
 - ISOMETRIC
 - FLOOR PLANS
 - TRANSVERSE SECTIONS
 - LONGITUDINAL SECTIONS
 - TRANSVERSE ELEVATIONS
 - LONGITUDINAL ELEVATIONS
- SITE
- DIAGRAMS FINAL MODEL
- FINAL MODEL ISOMETRIC
- PERSPECTIVE RENDERS
- FINAL FLOOR PLANS
- FINAL TRANSVERSES
- FINAL SECTIONS

1 S T
S E M E S T E R



DIGITAL/PHYSICAL FOLDED CUBES WITH ORTHOGONALLY DRAWN LINE PATHS

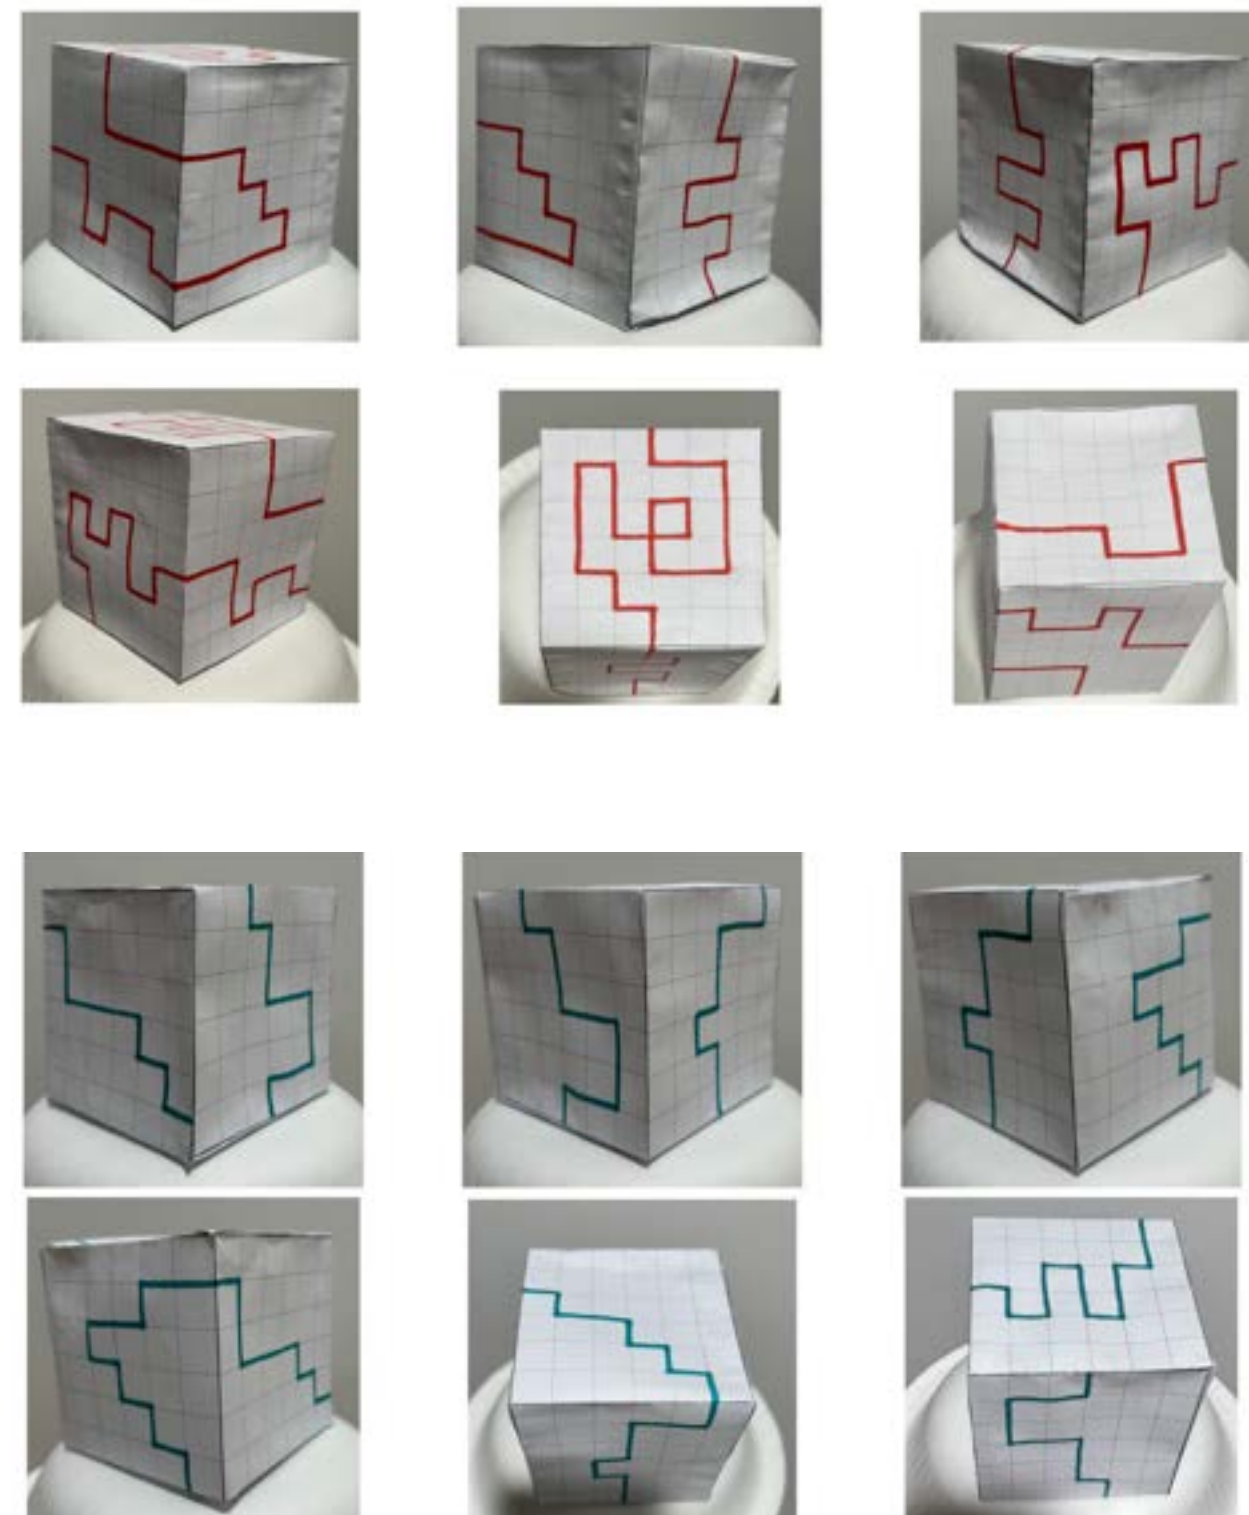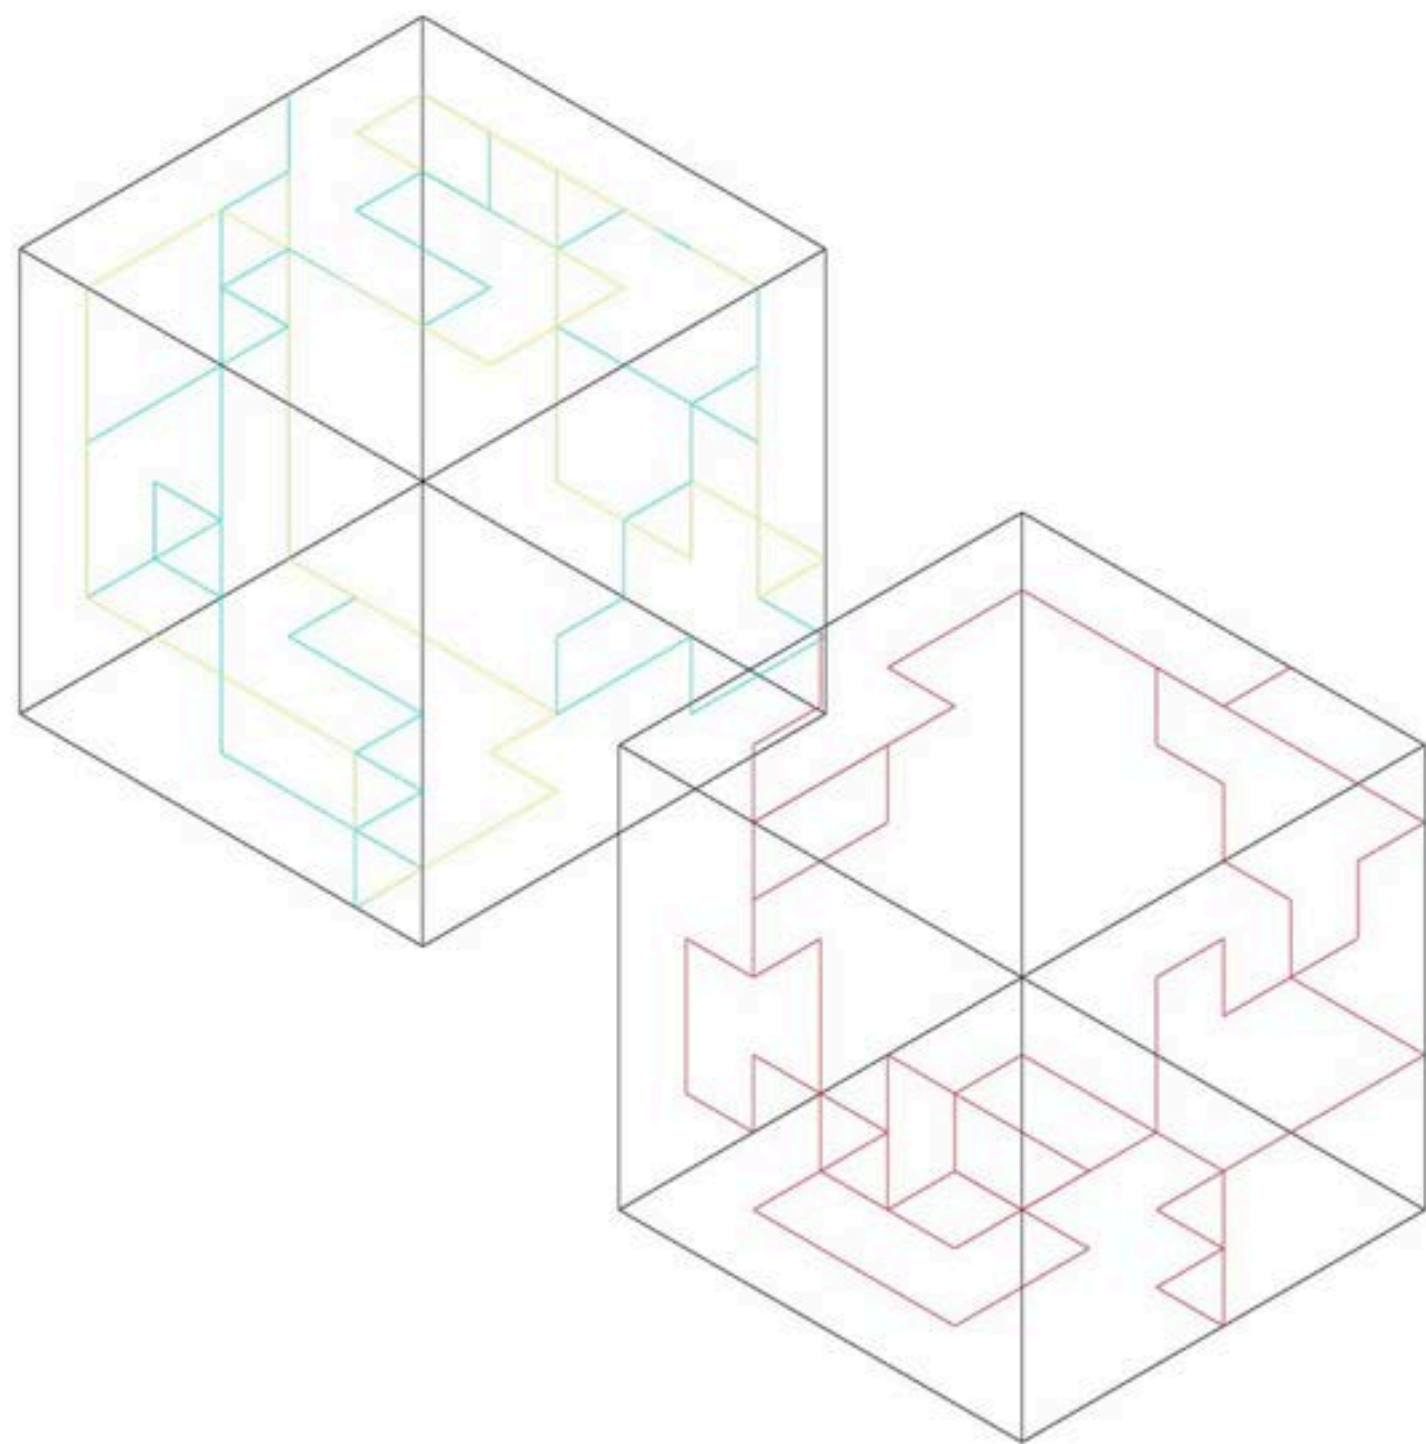

D I G I T A L E X P L O D E D I S O M E T R I C O F T H E C U B E S

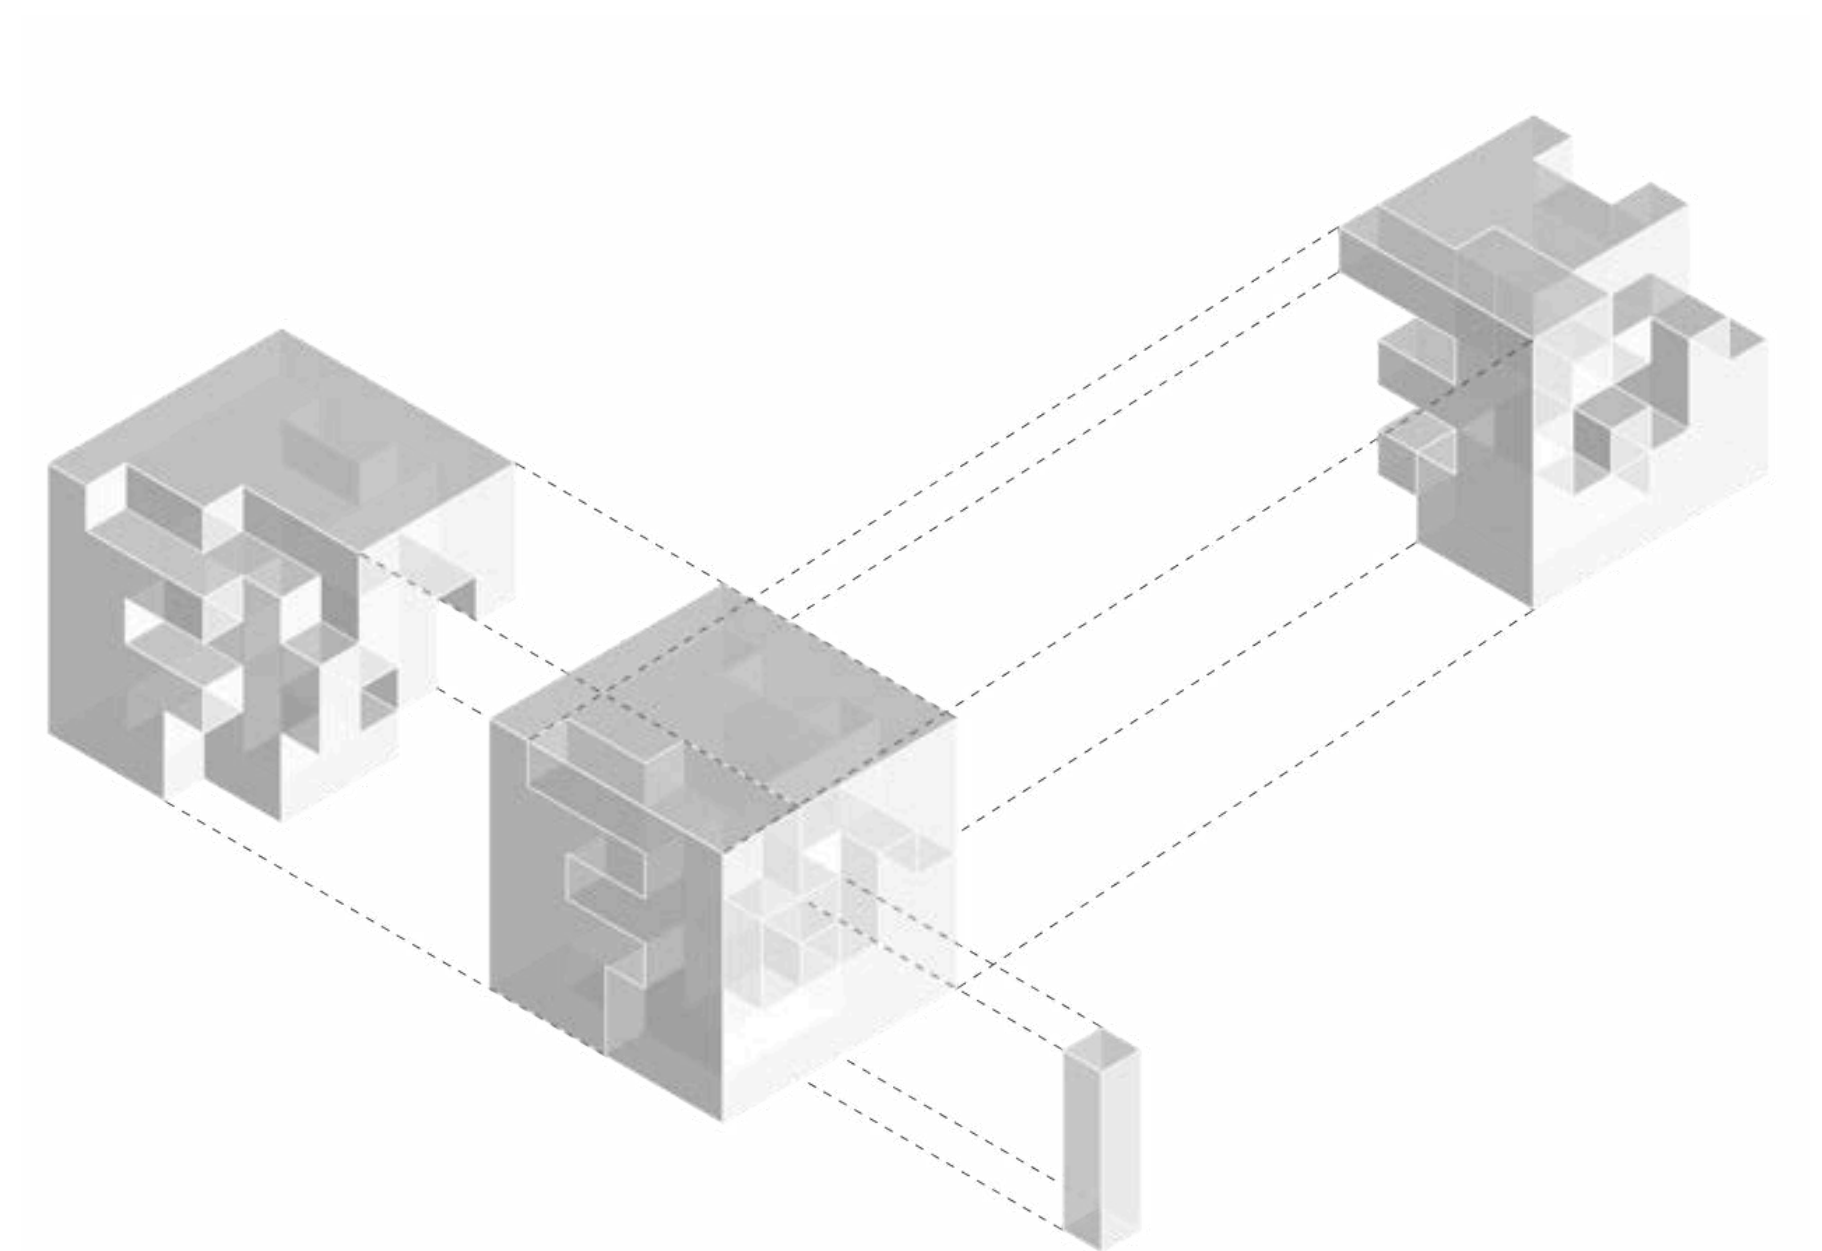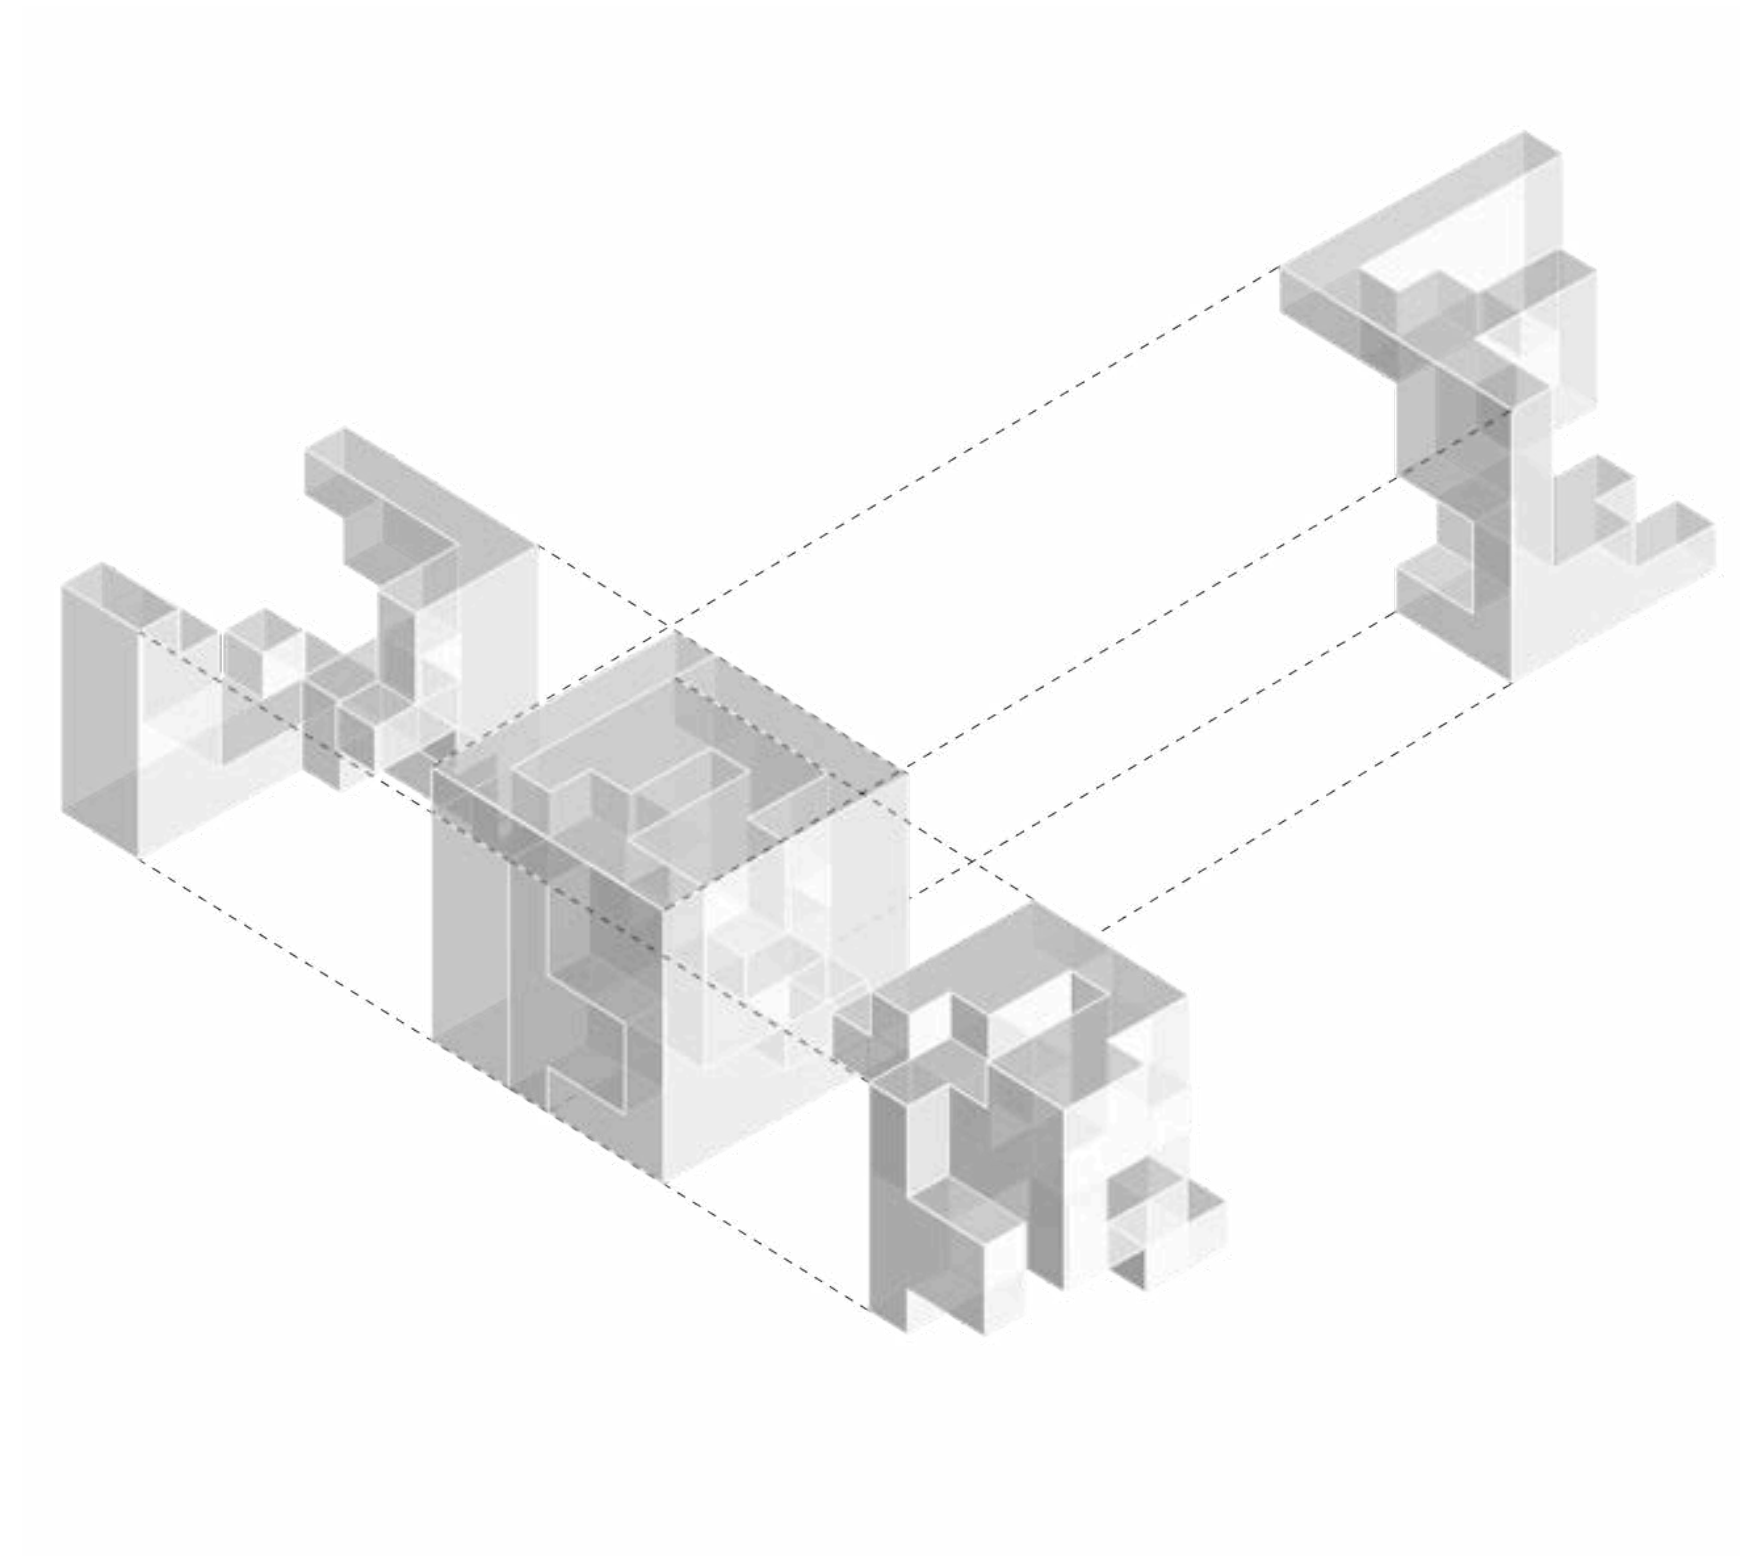


D I G I T A L V O L U M E S

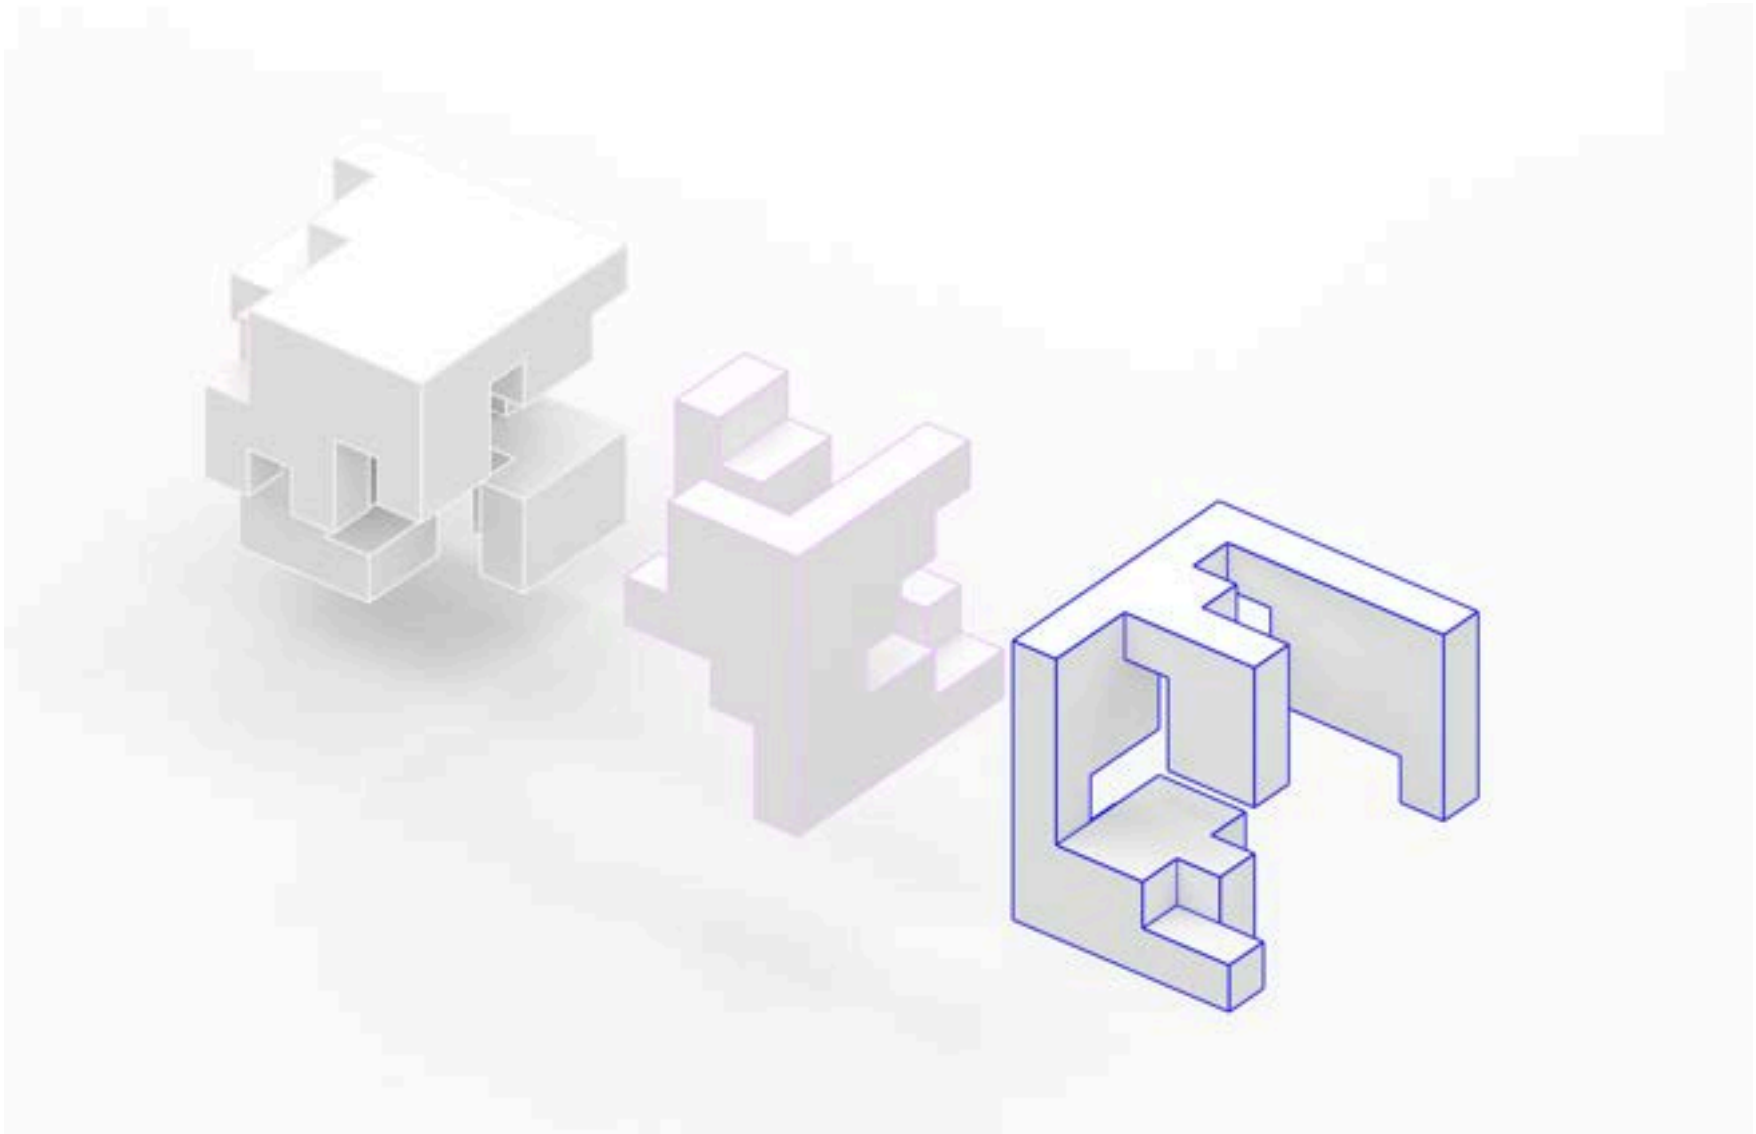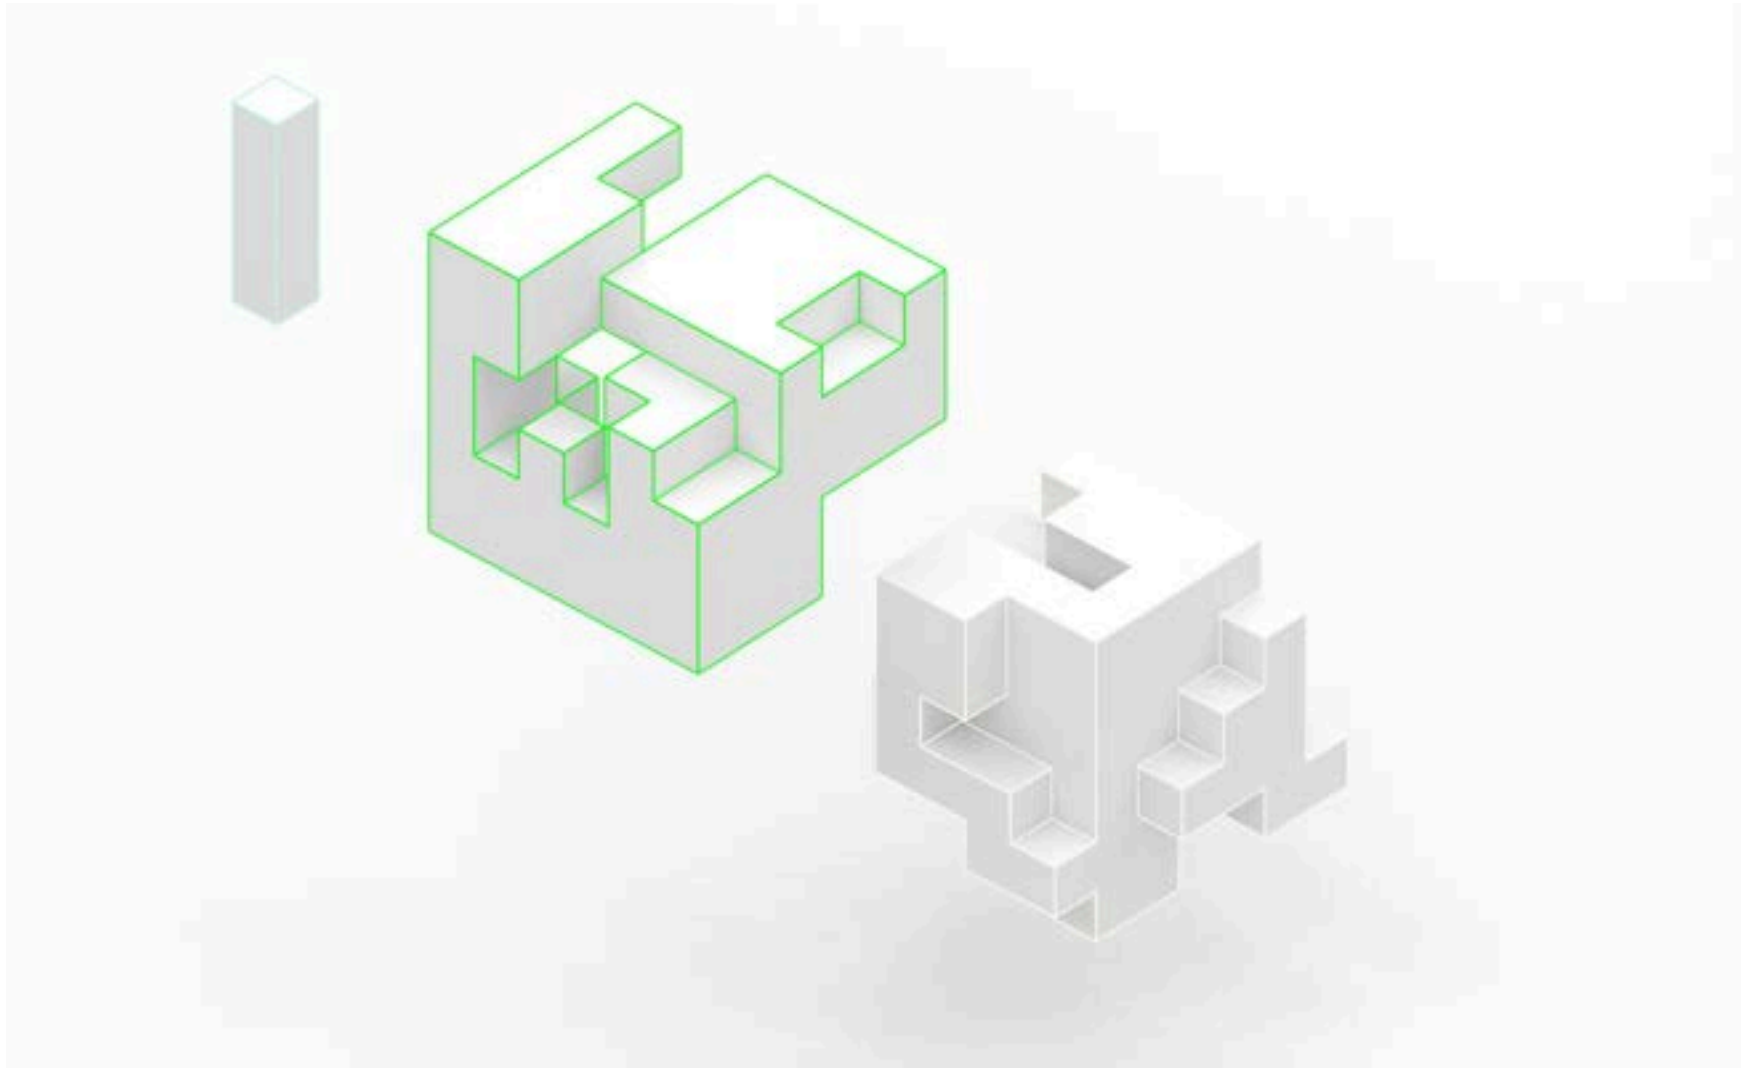

DIAGRAMS & MODELS OF HORIZON & SKY VOLUMES




Horizon

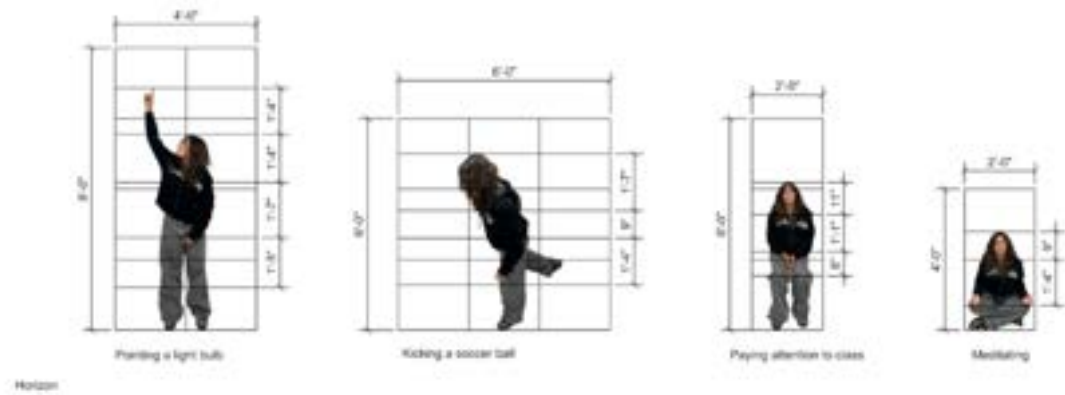

Horizon






Sky

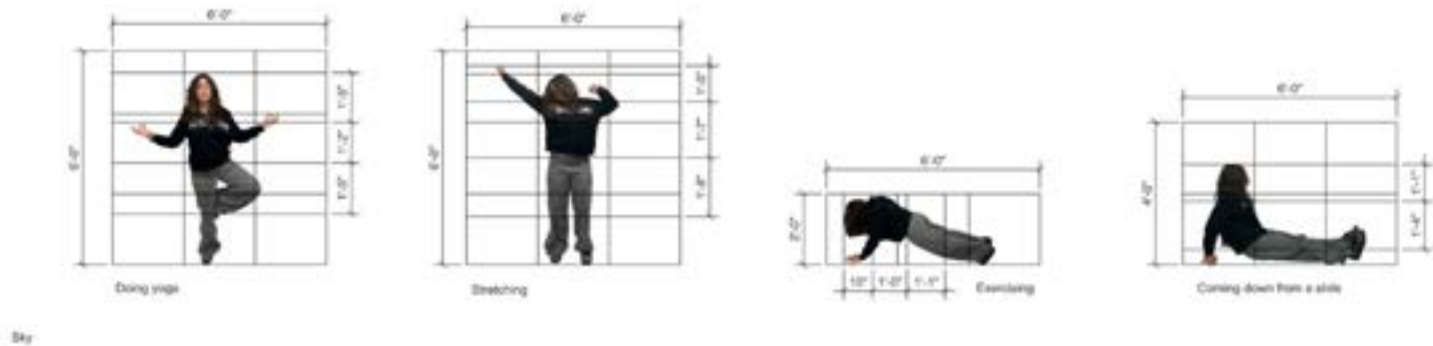


sky


FIRST PHYSICAL MODEL

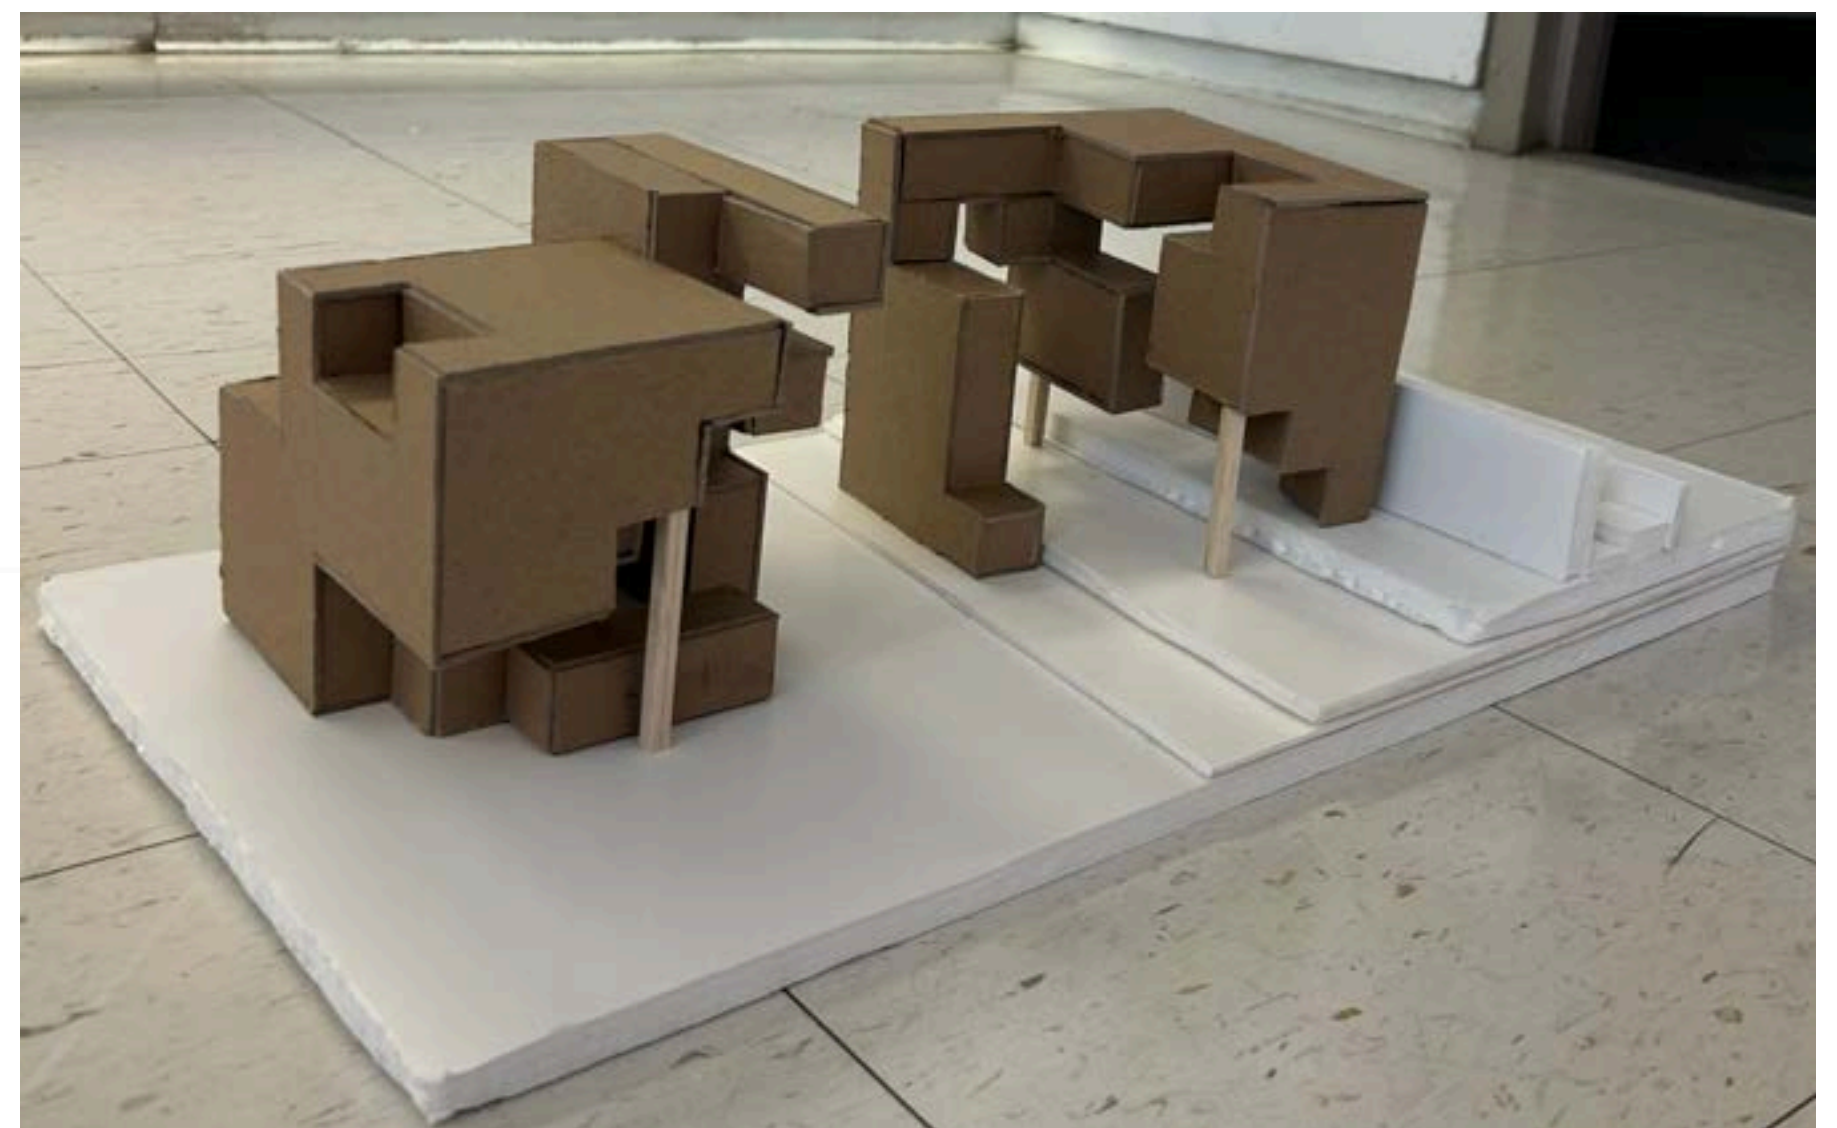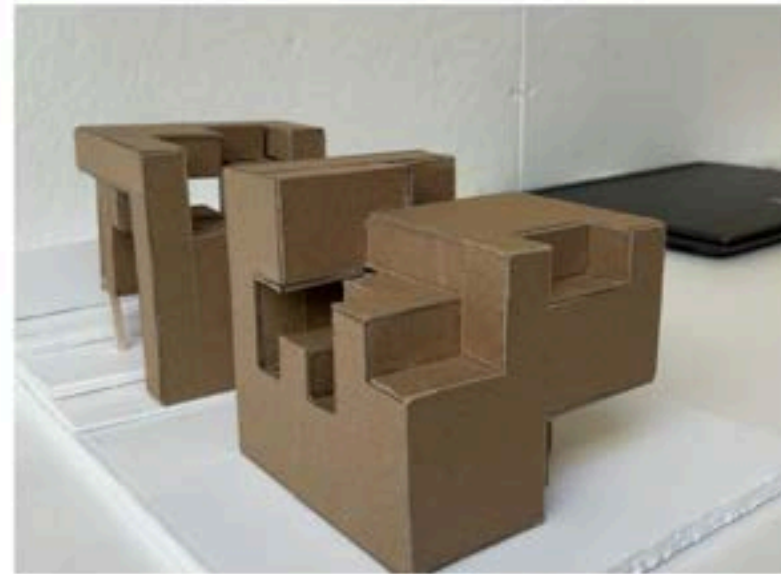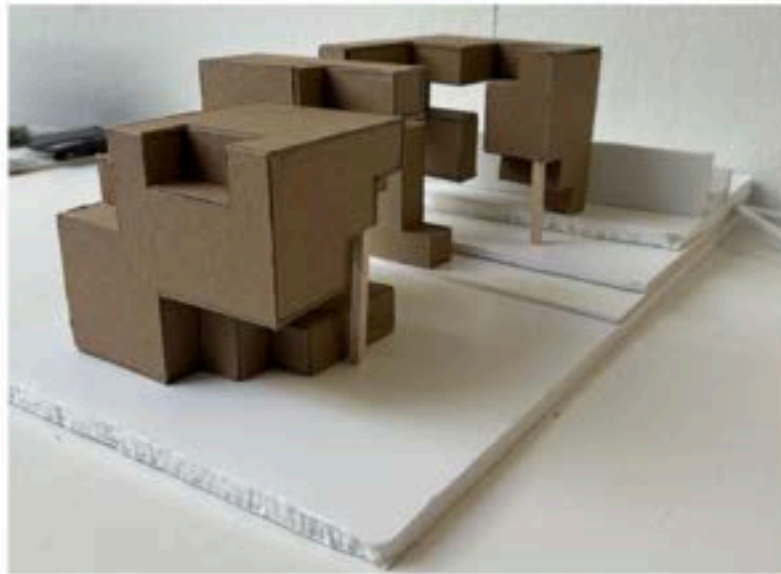


ENVIROMENTAL ENCLOSURES

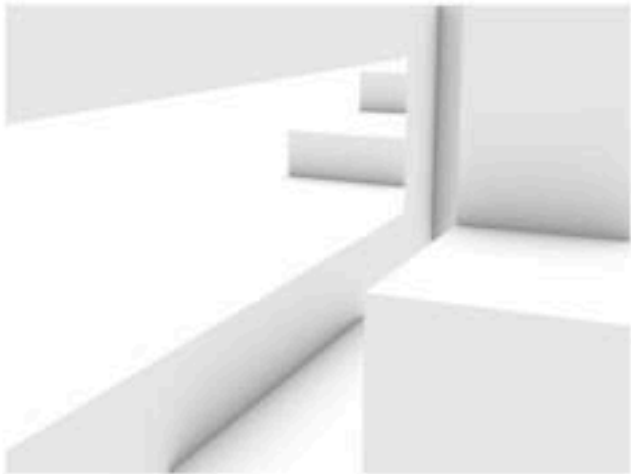


Hallway first floor
Horizon

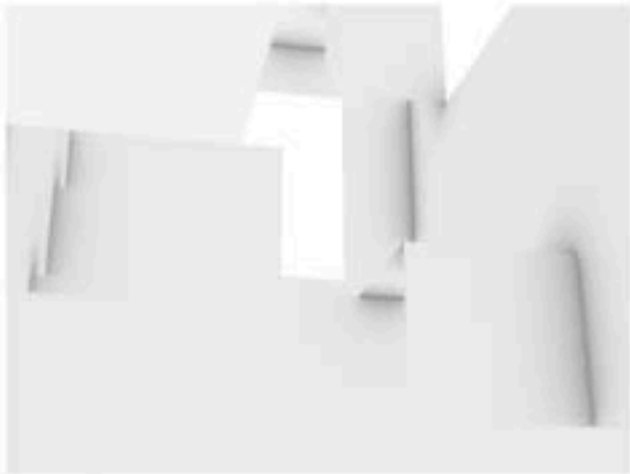

Recreational room
Horizon

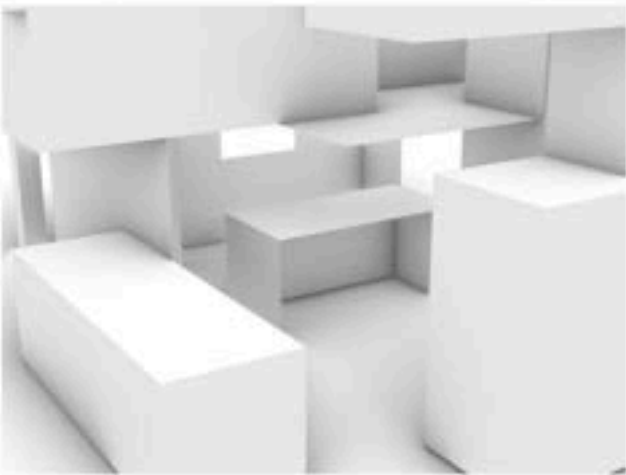


Living room
Horizon

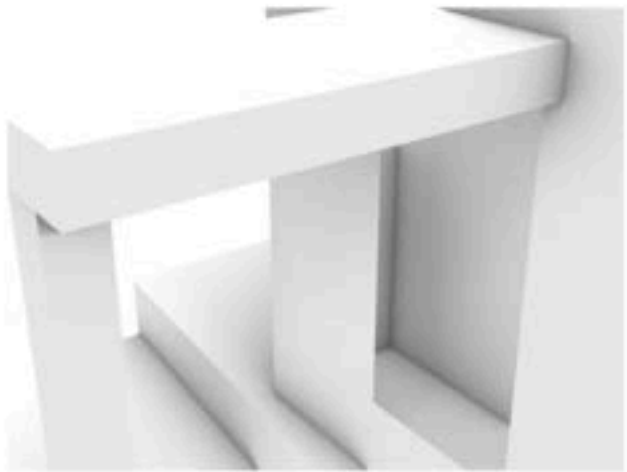

2nd Entry
Sky









Hallway 2nd floor
Sky

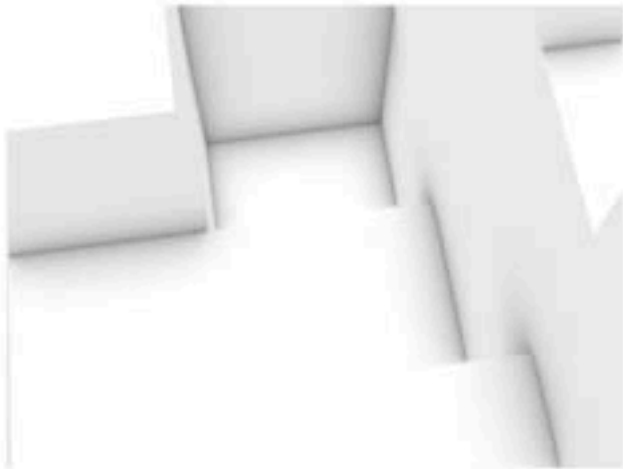


Balcony with stairs
Sky


DIAGRAMS FLOOR PLANS

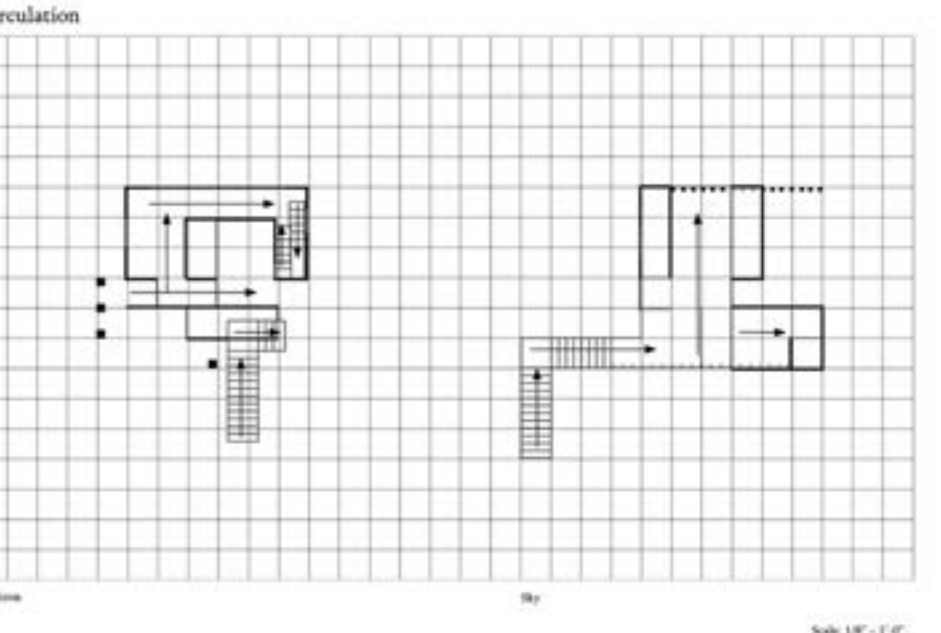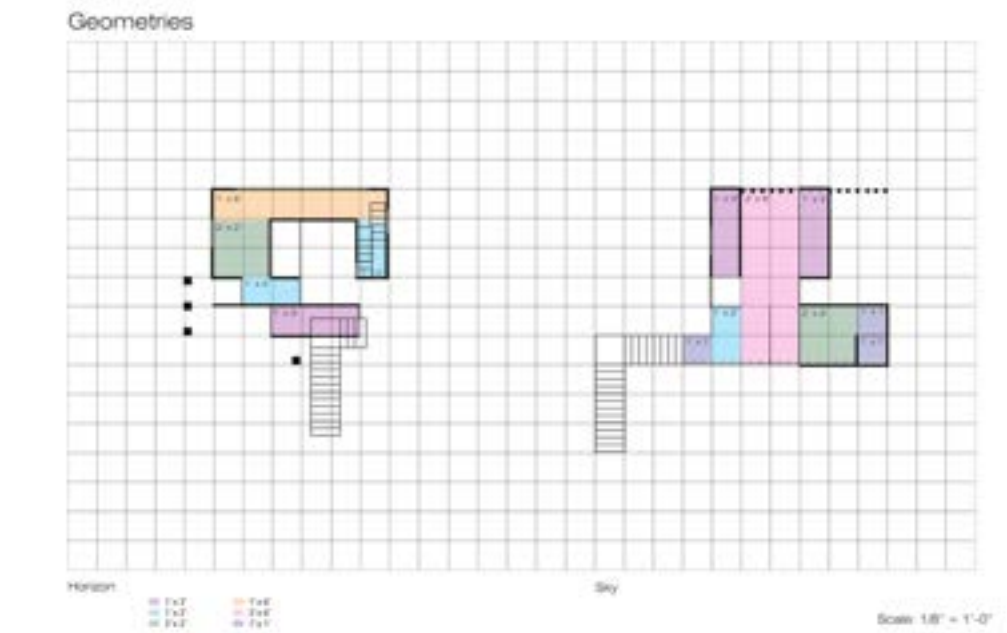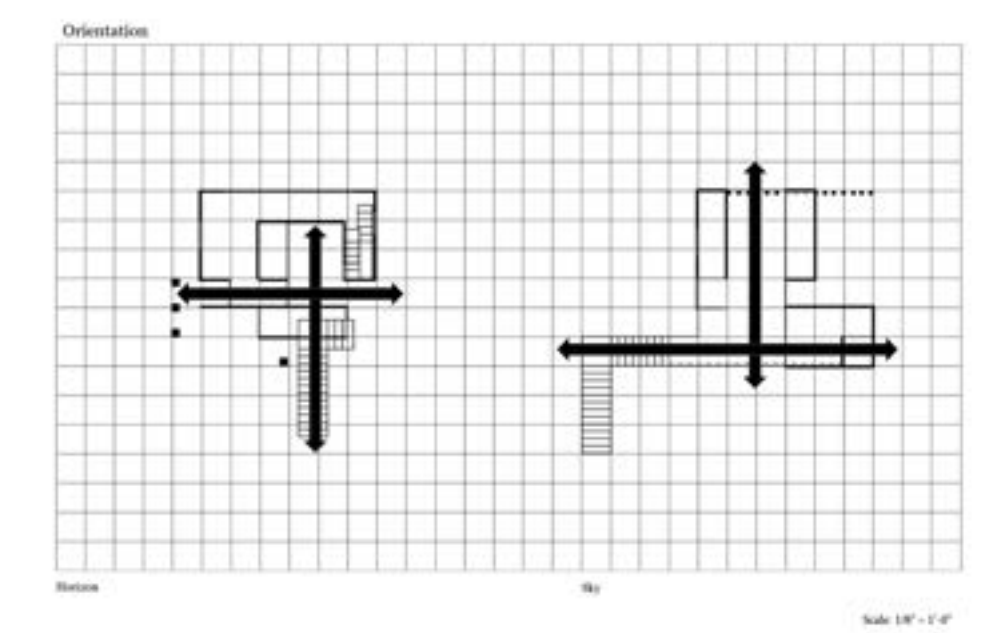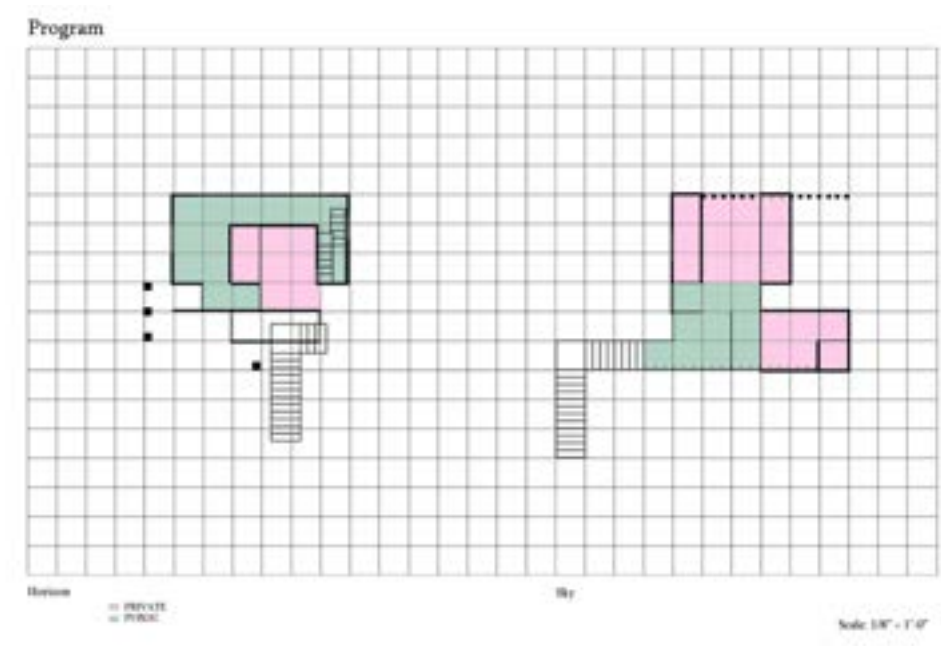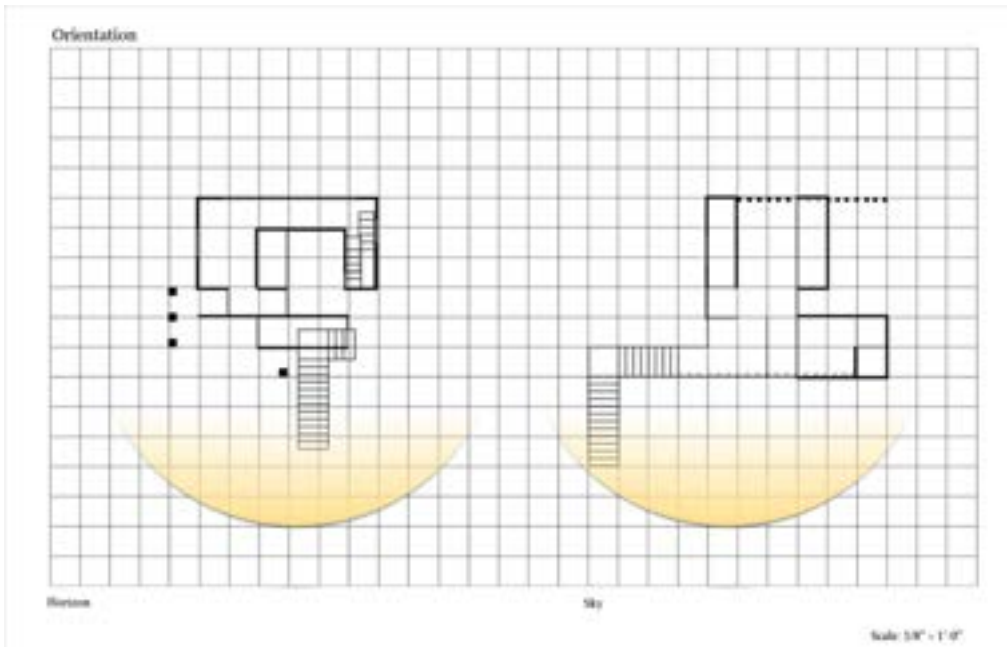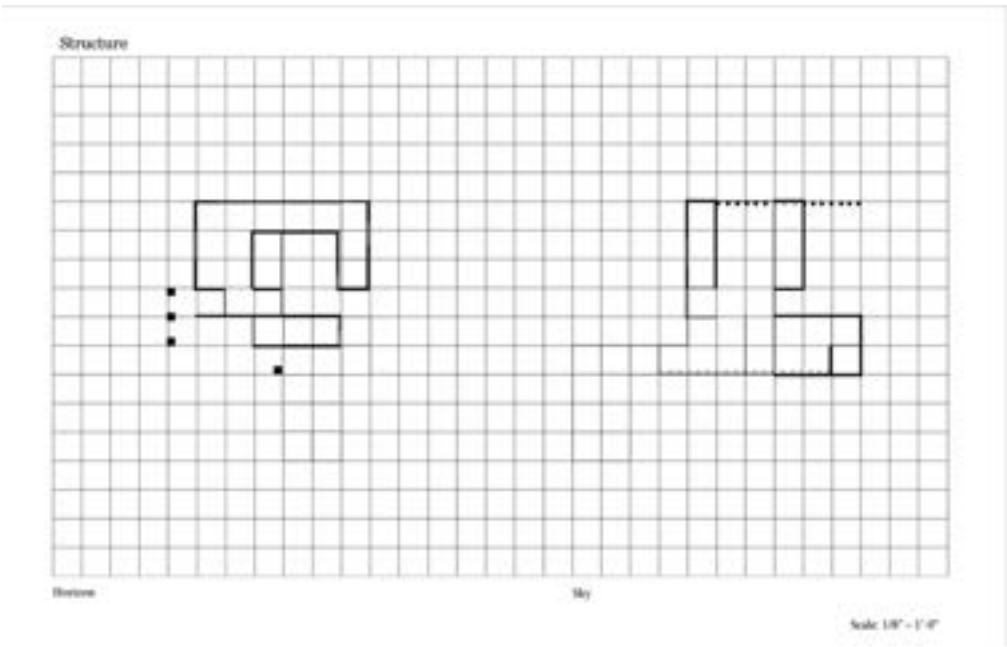

TAXONOMY

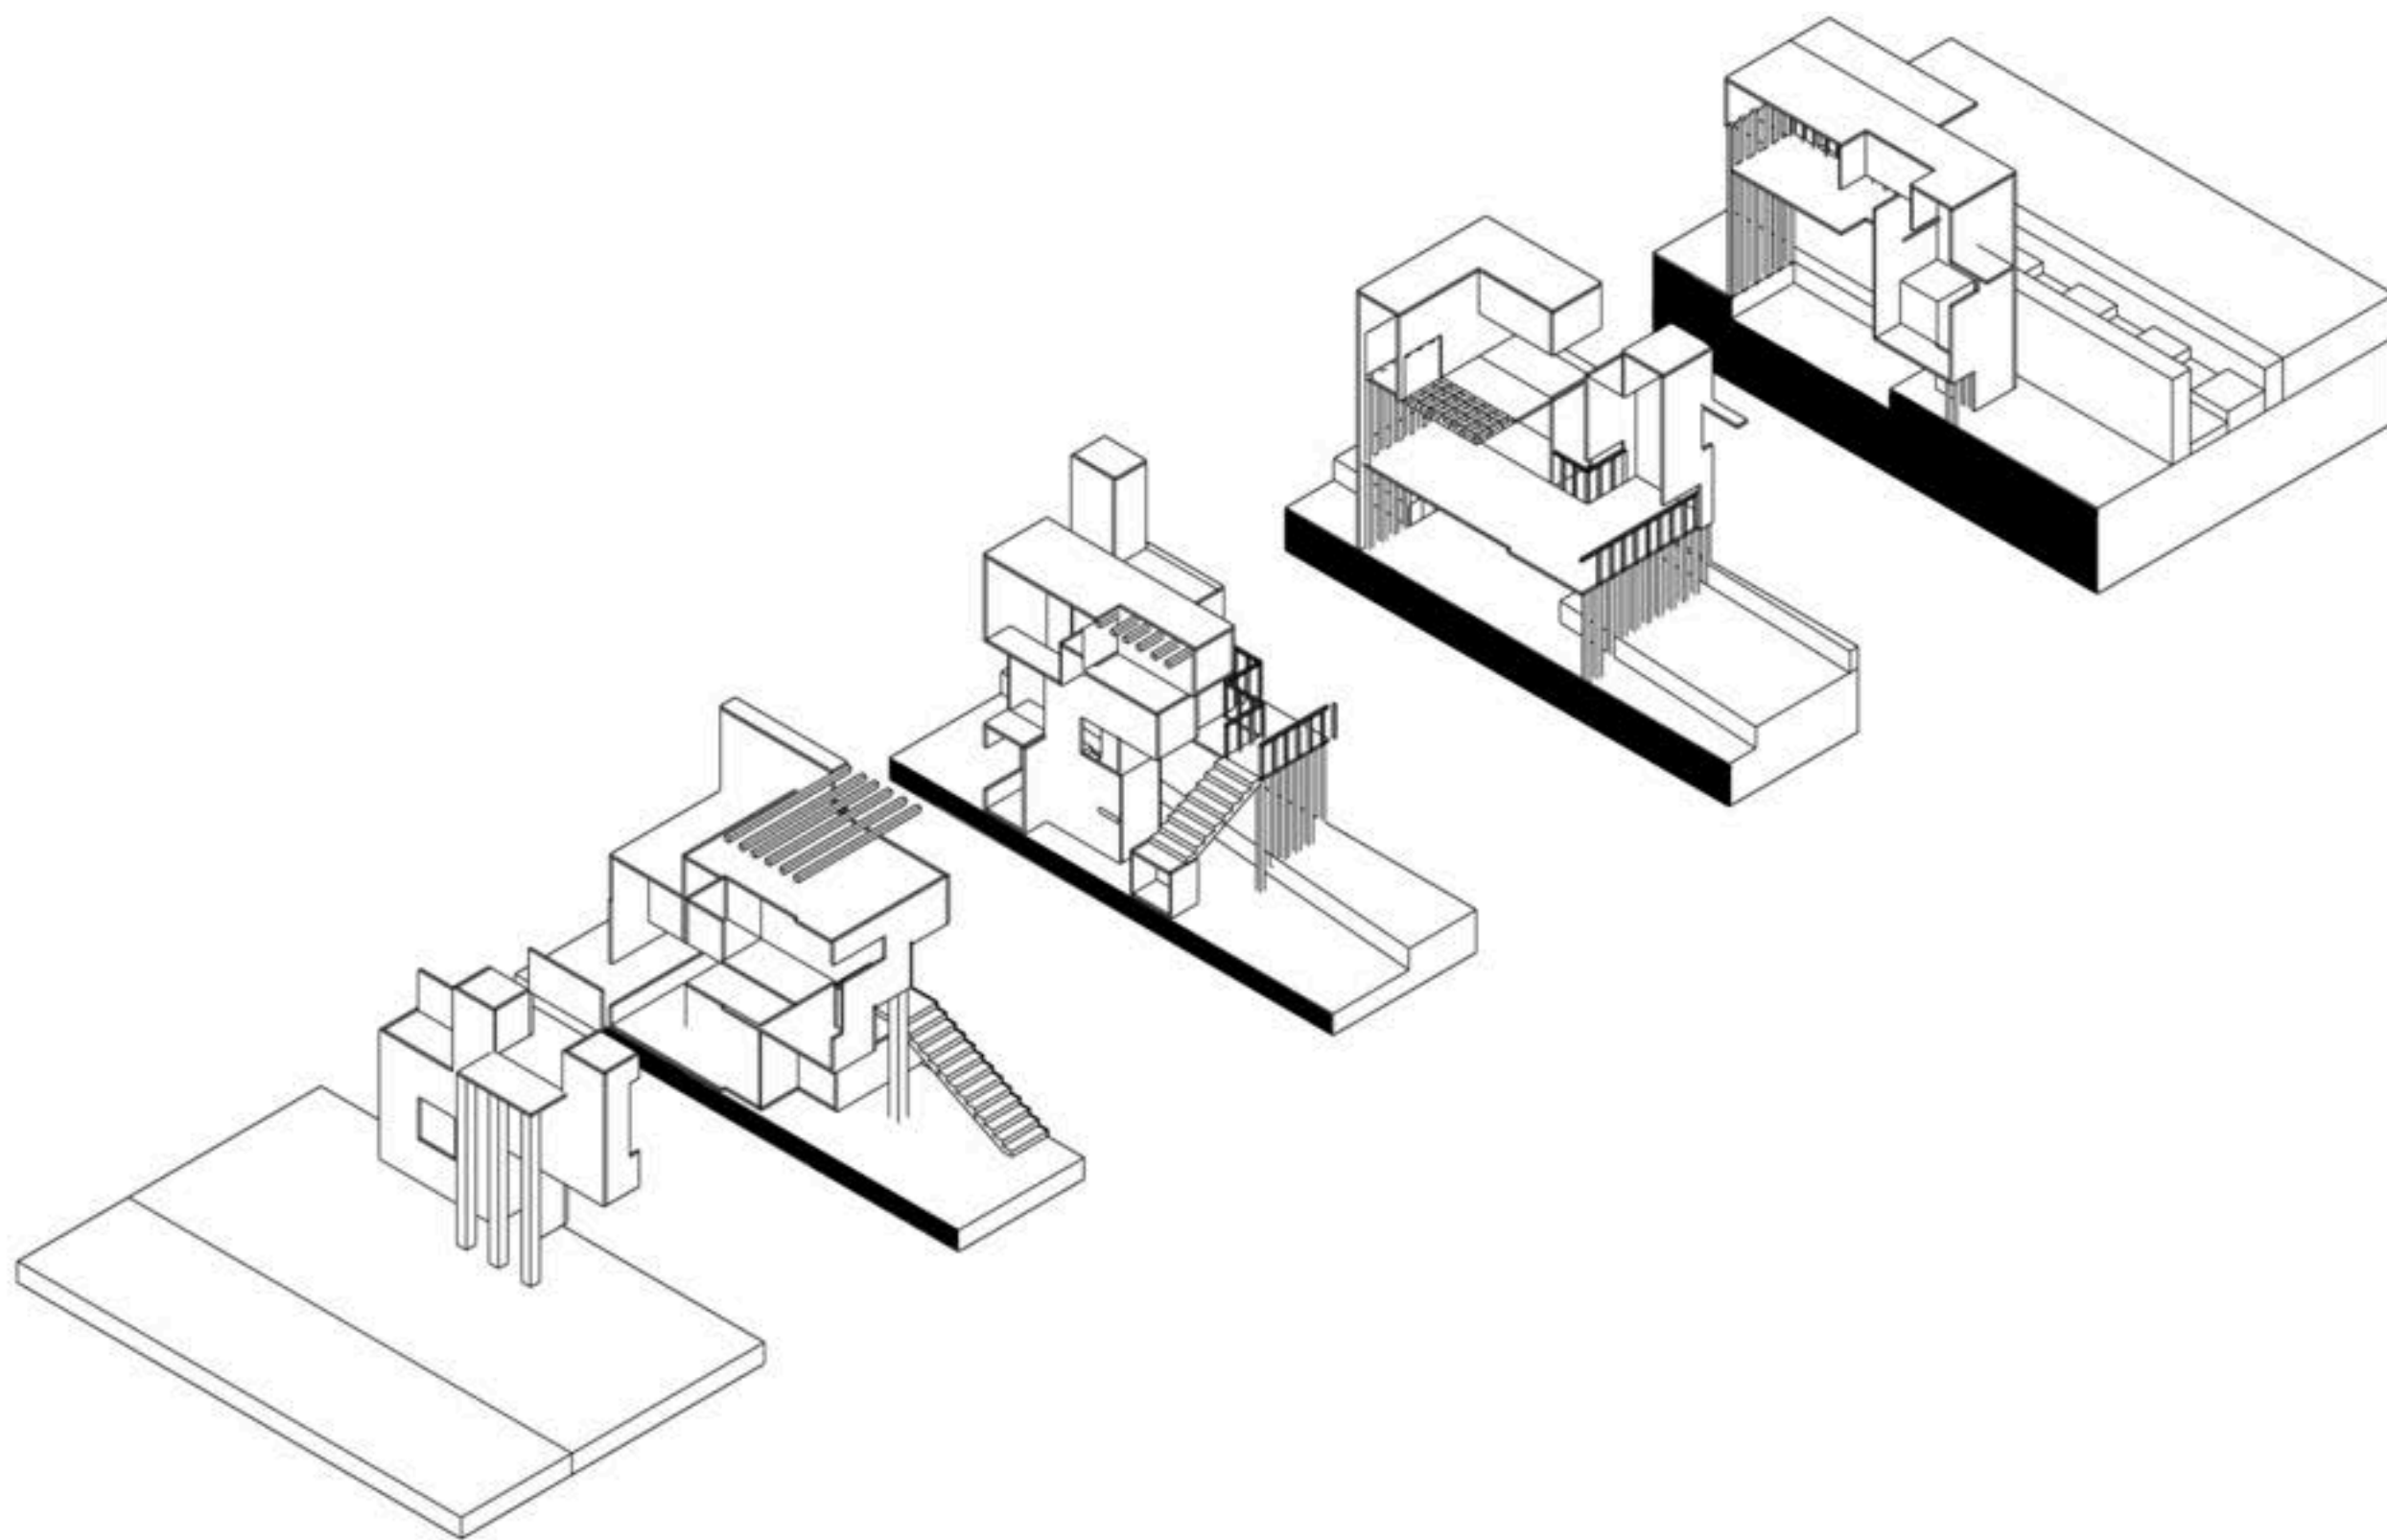


FLOOR PLANS & SECTIONS

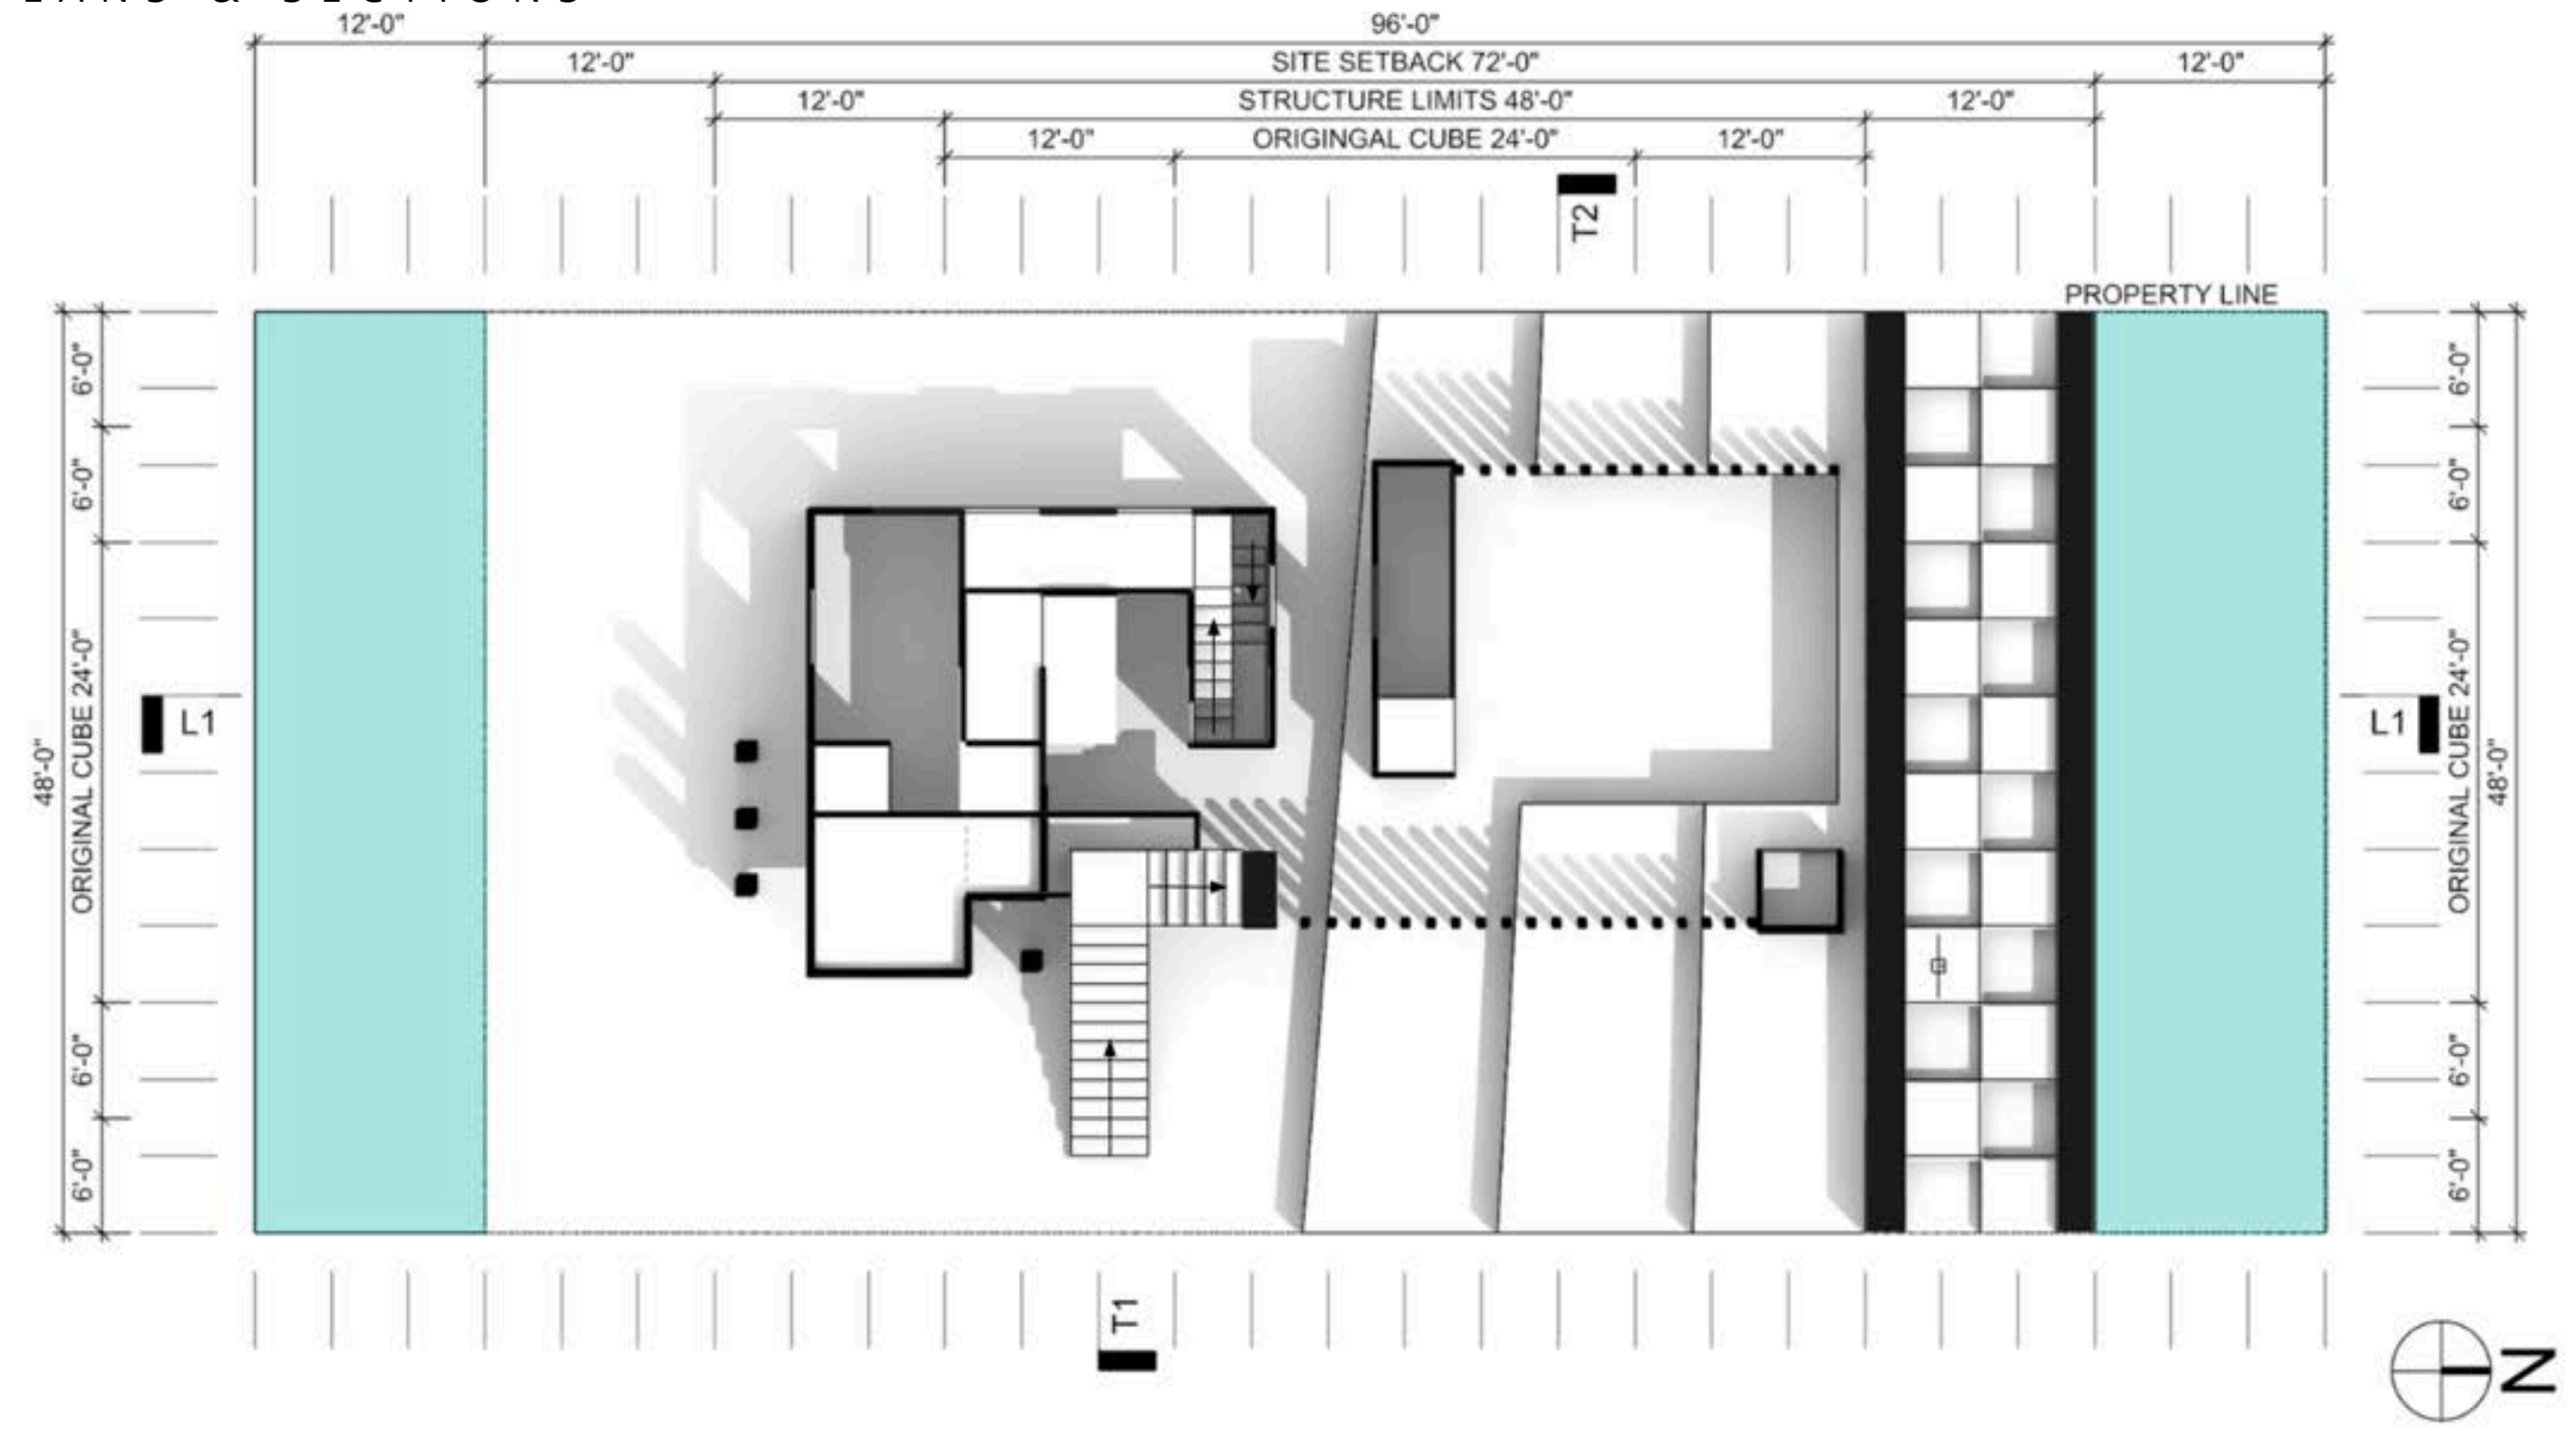


1 FIRST FLOOR PLAN
scale : 1/8" = 1'-0"




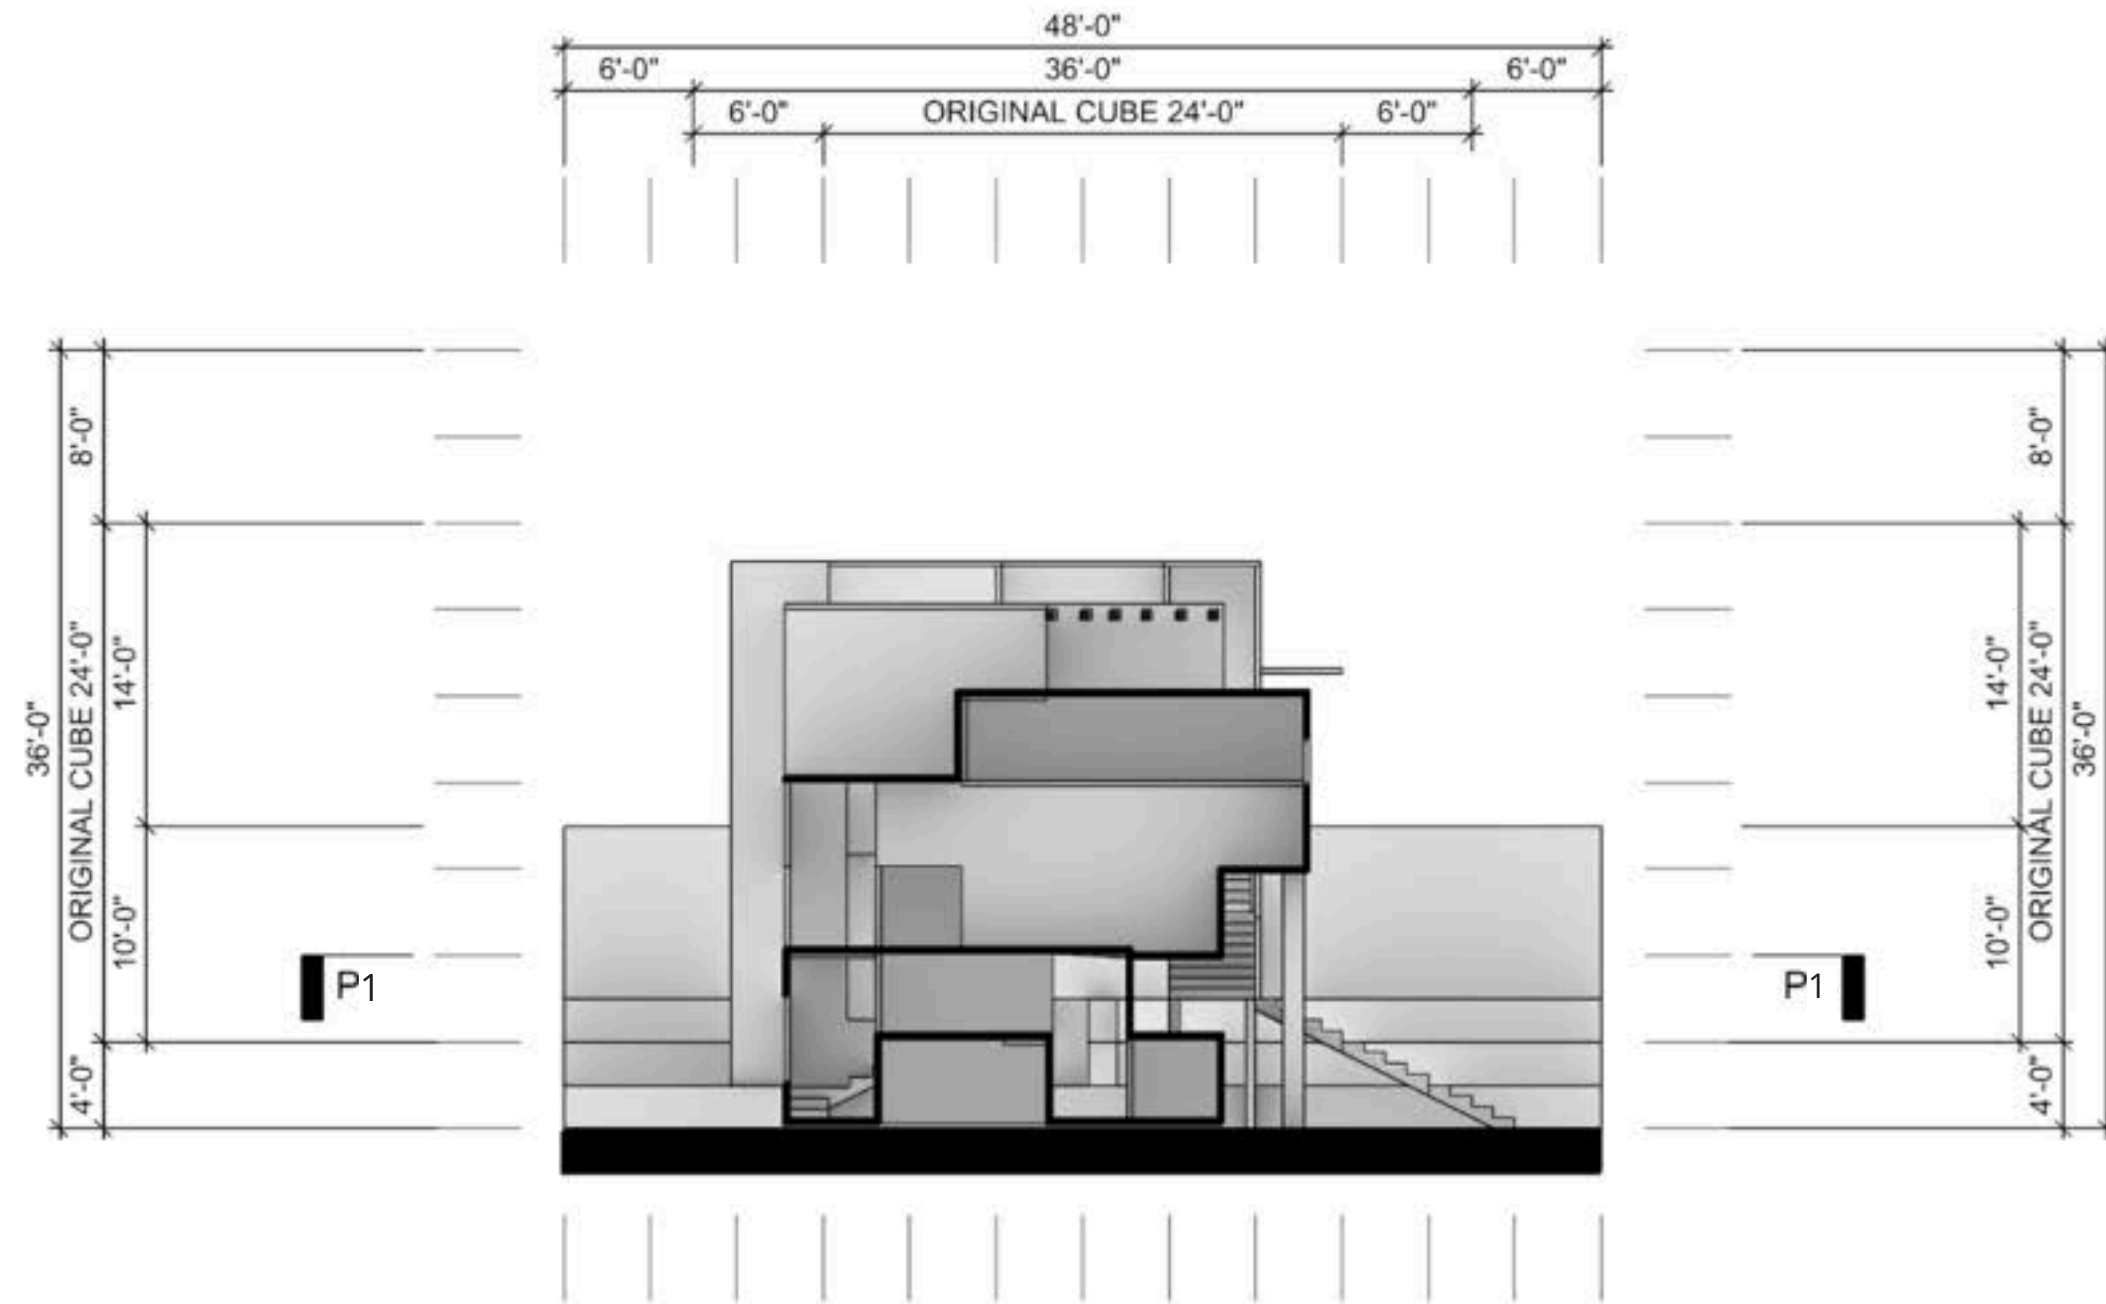


1 TRANSVERSE SECTION
scale : 1/8" = 1'-0"

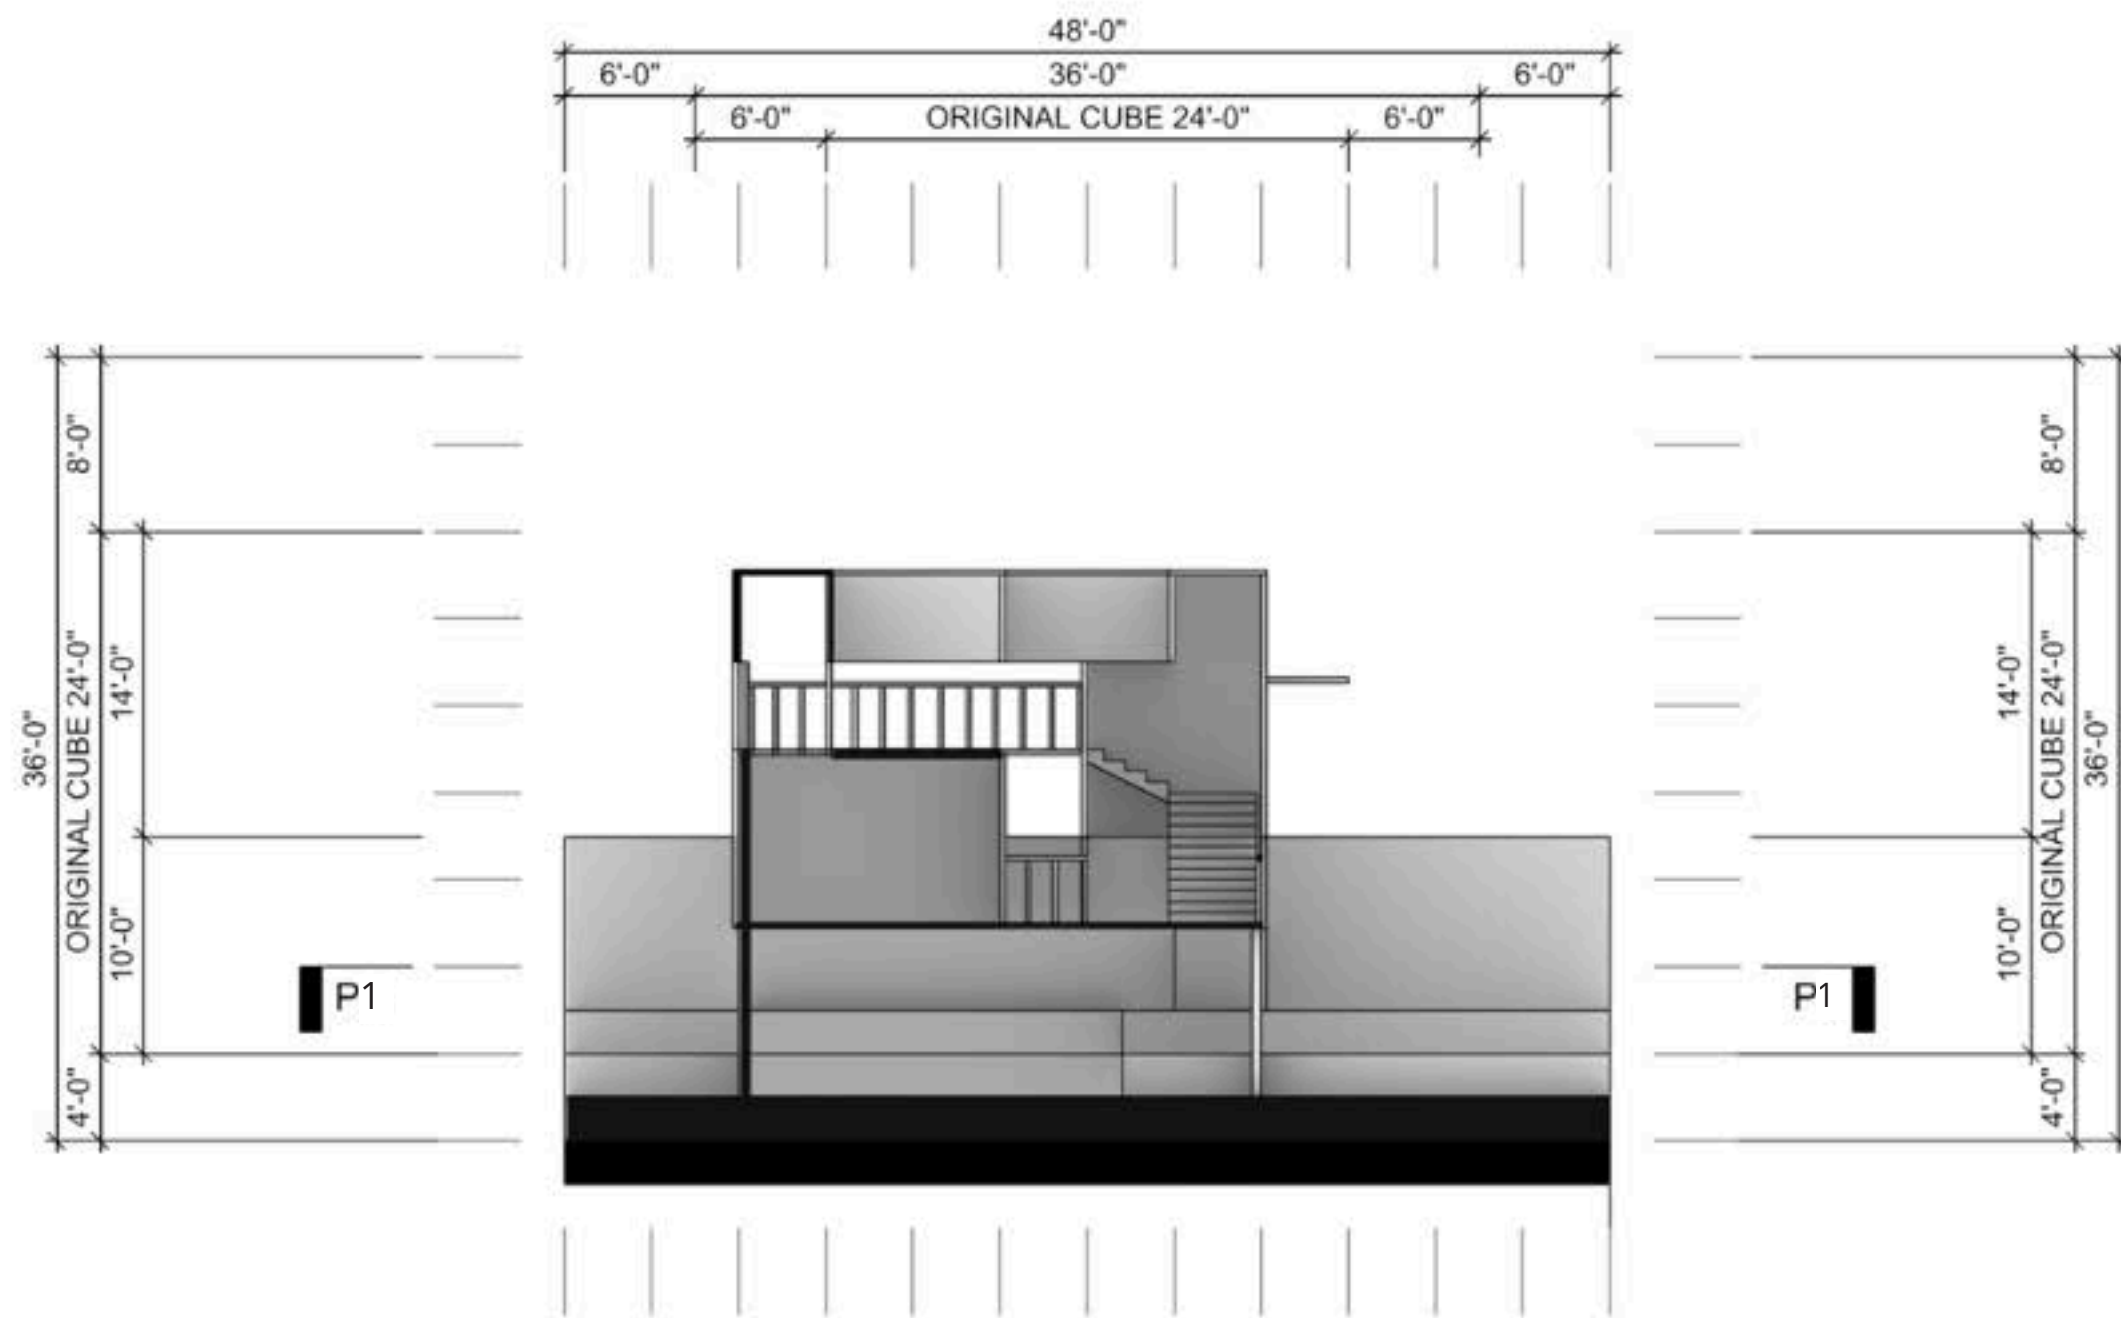


2 TRANSVERSE SECTION
scale : 1/8" = 1'-0"

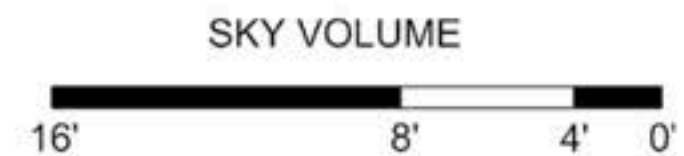

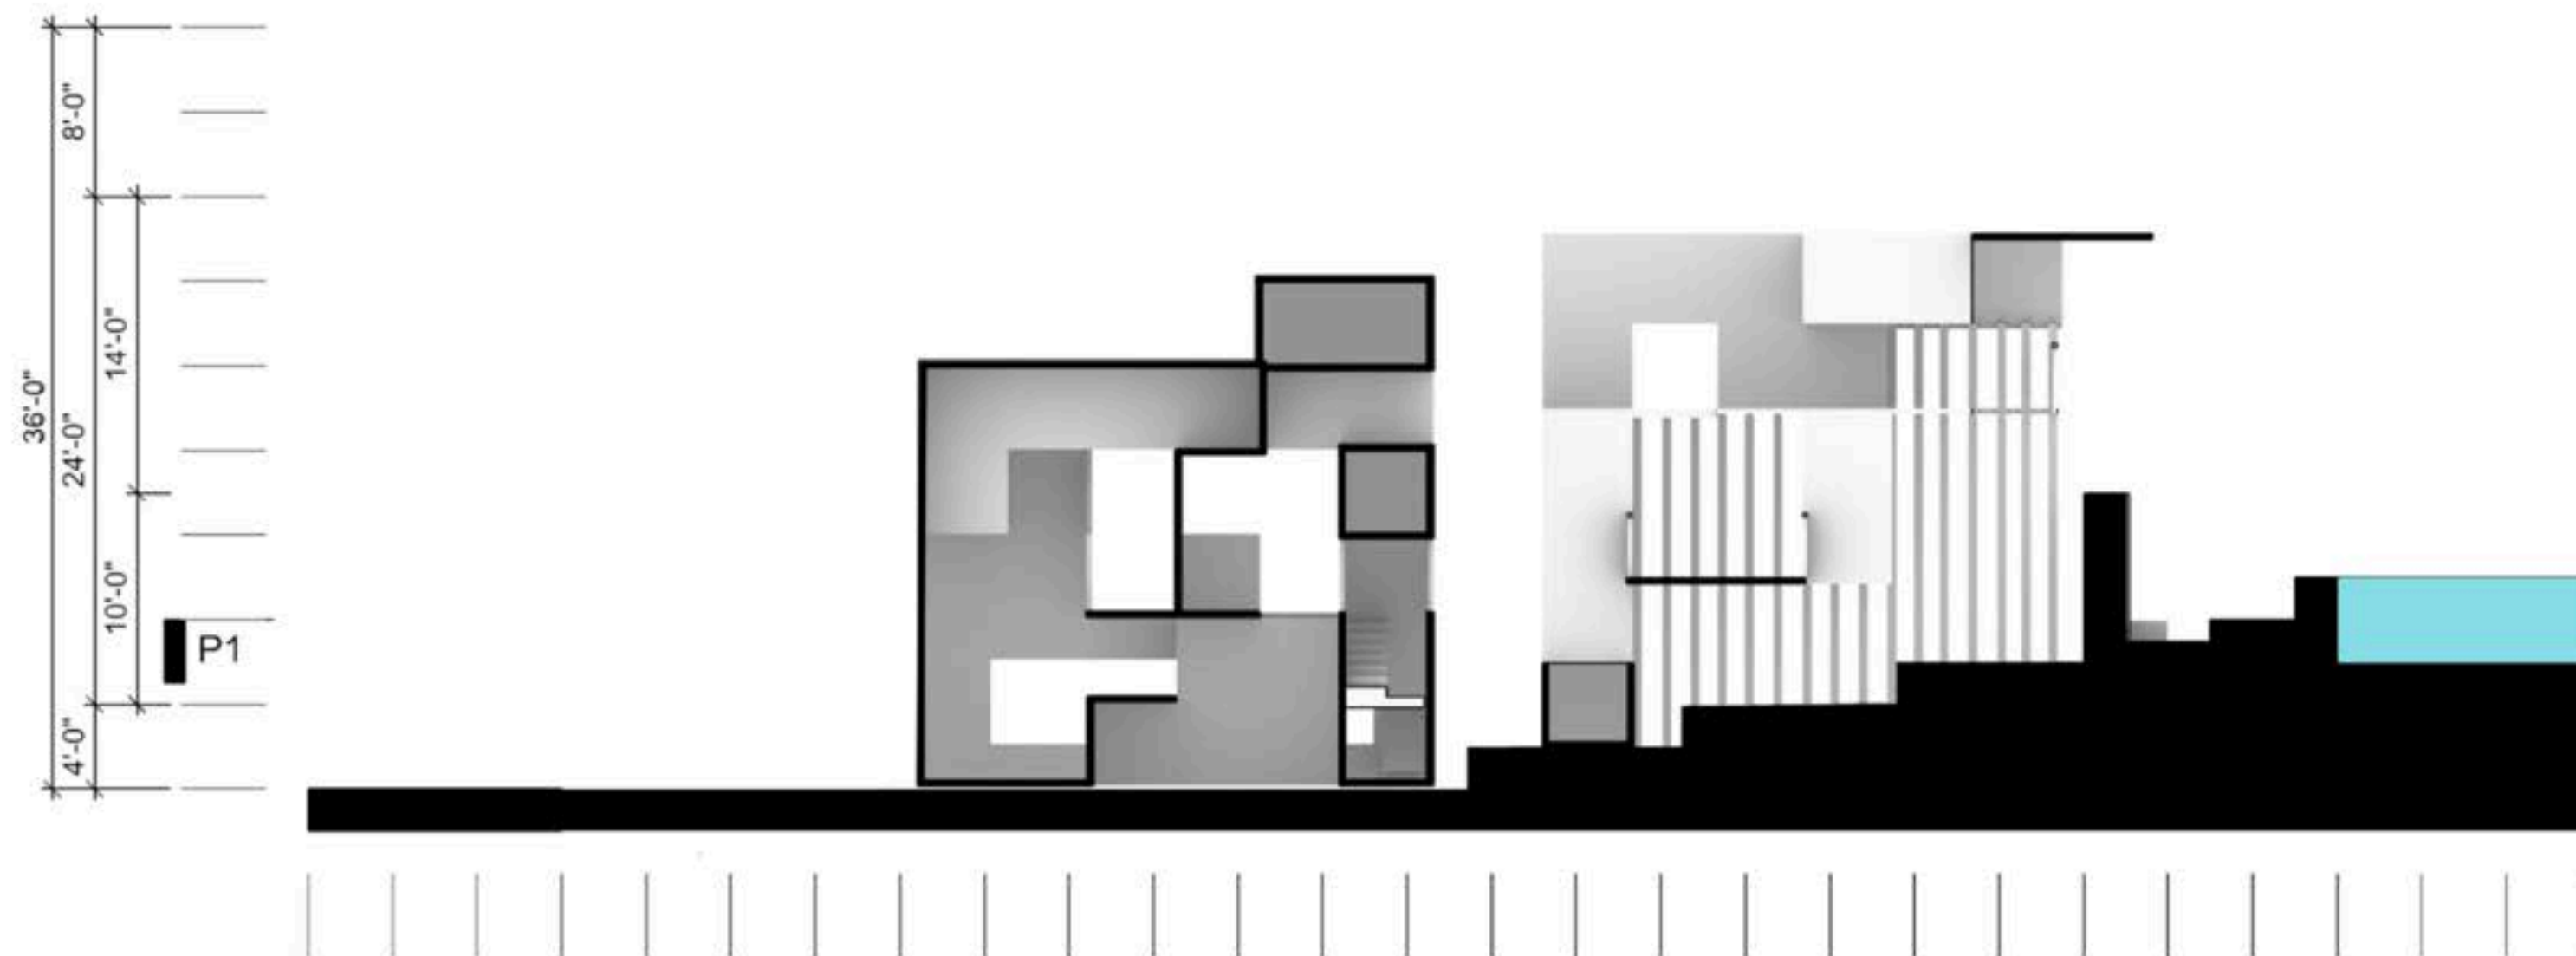

1 LONGITUDINAL SECTION
scale : 1/8" = 1'-0"




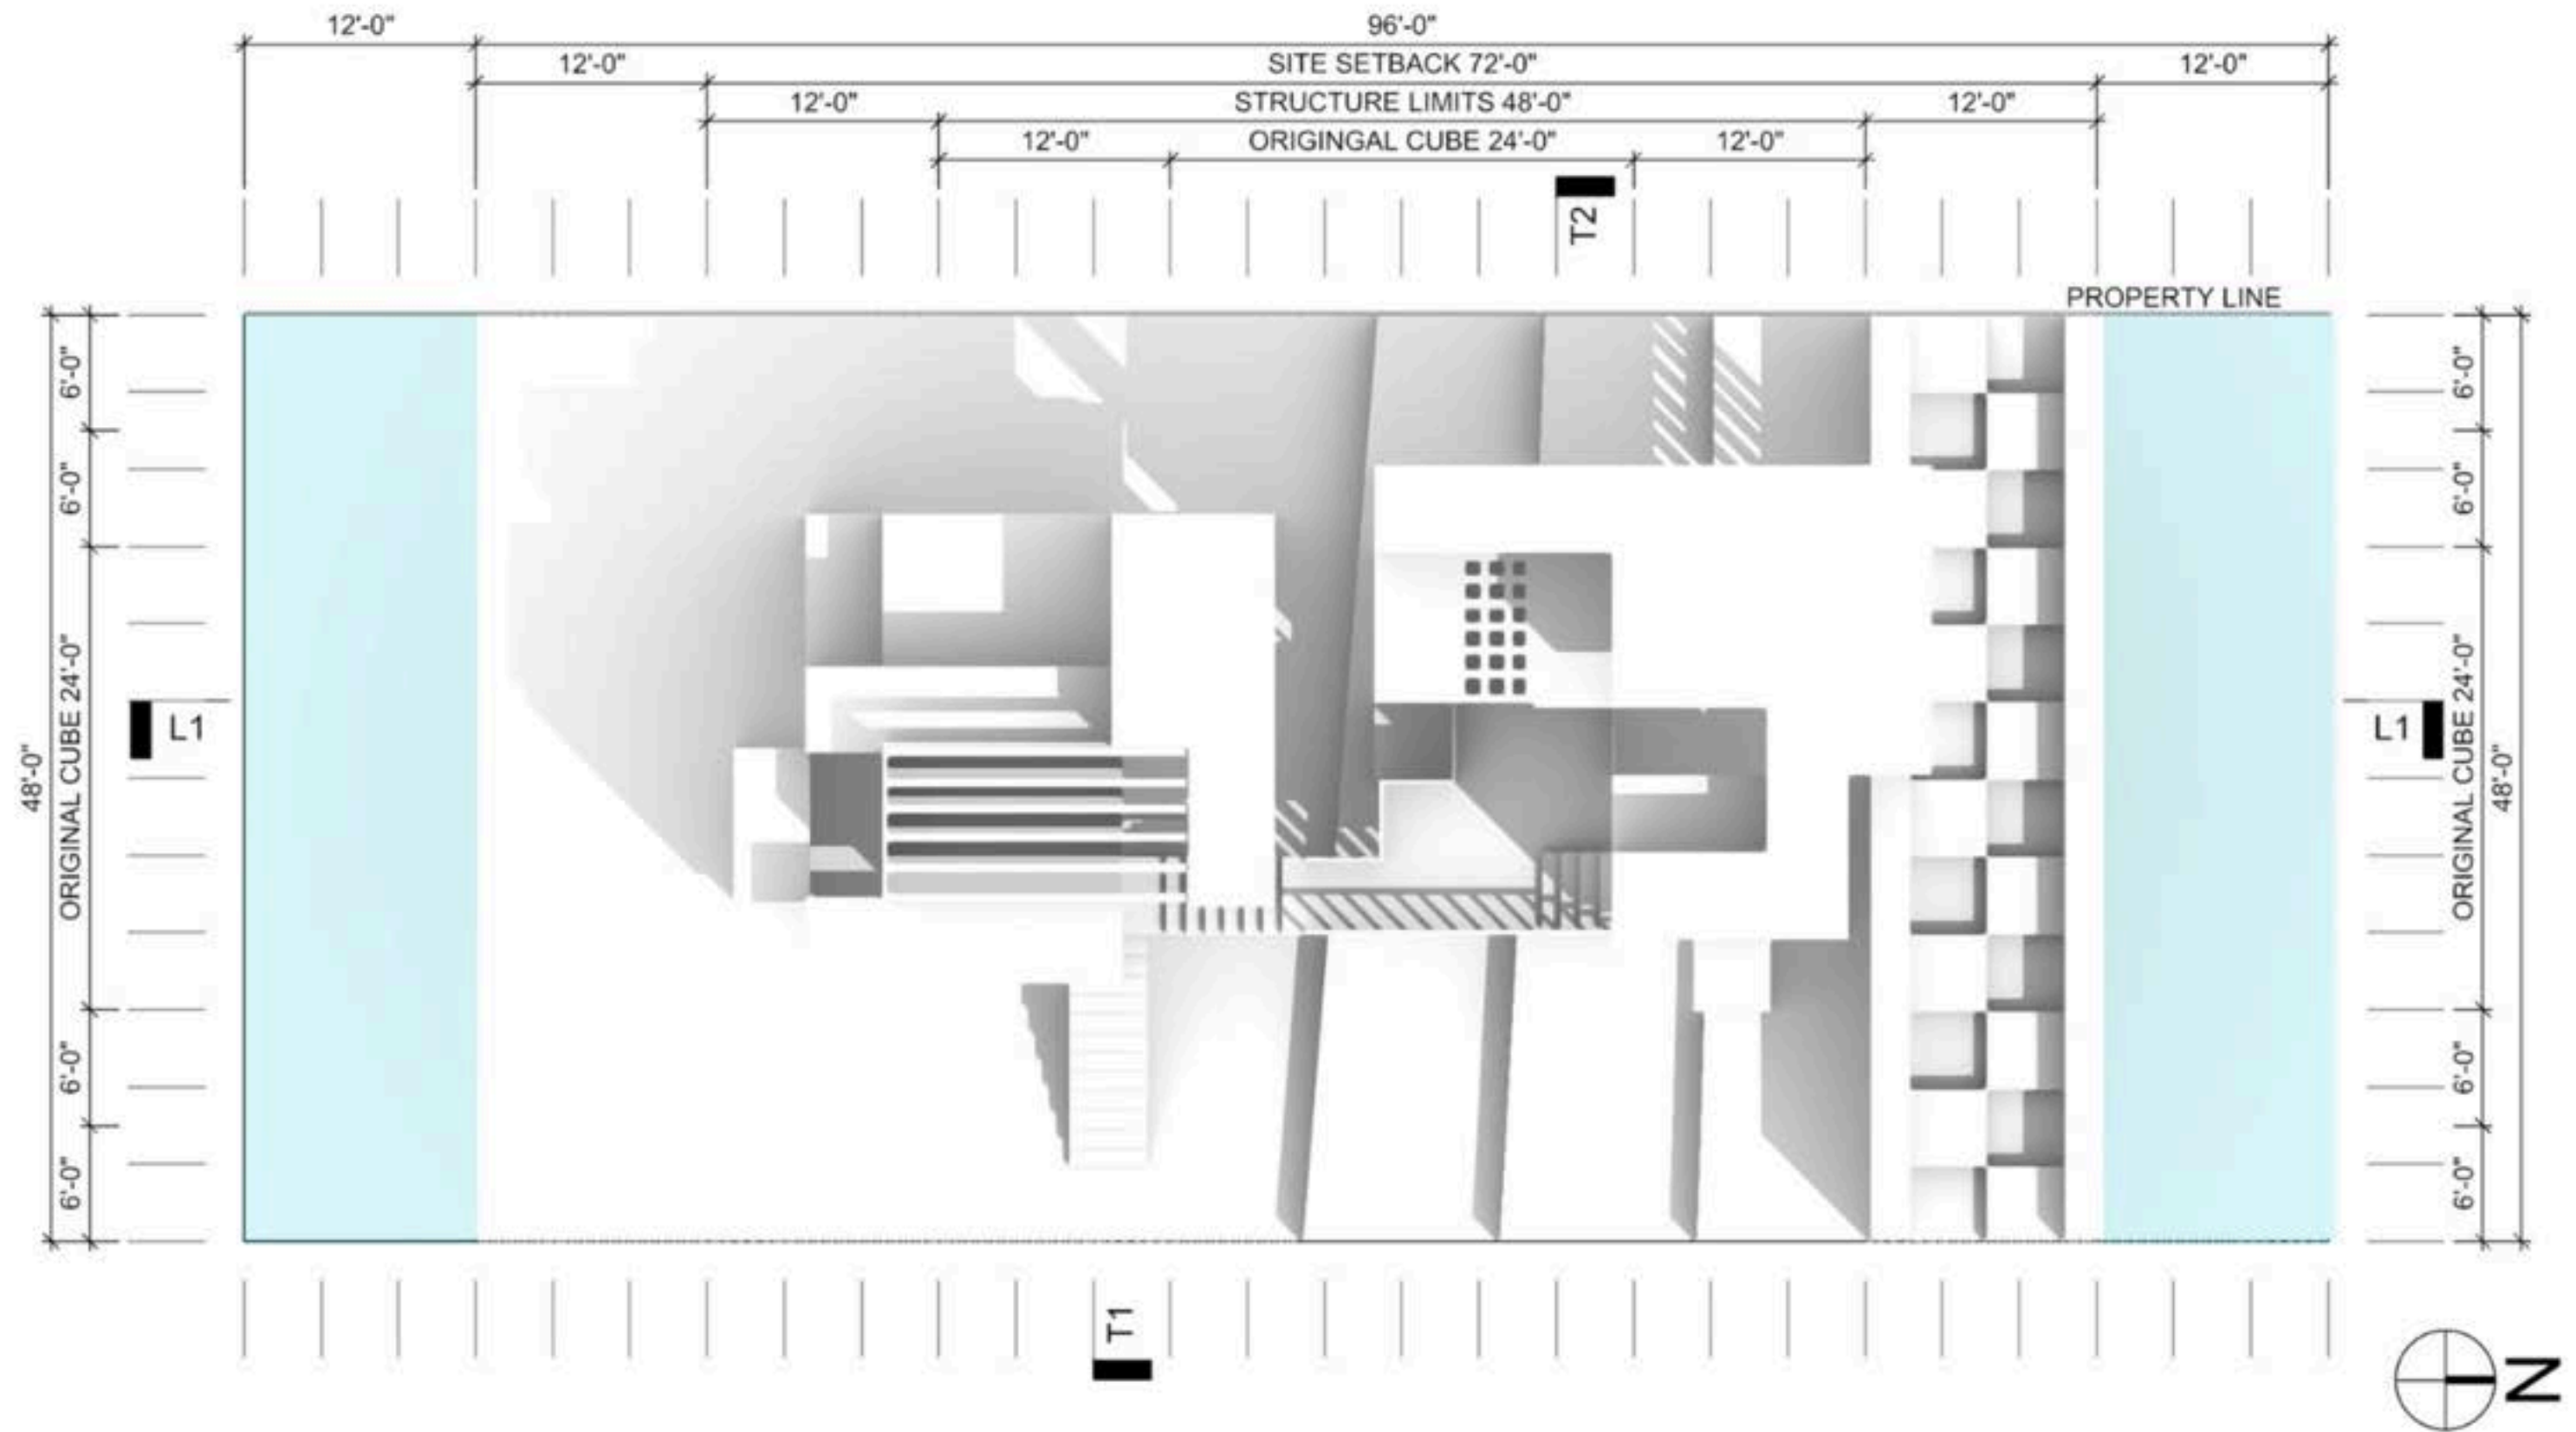

1 ROOF PLAN
scale : 1/8" = 1'-0"




CIRCULATION

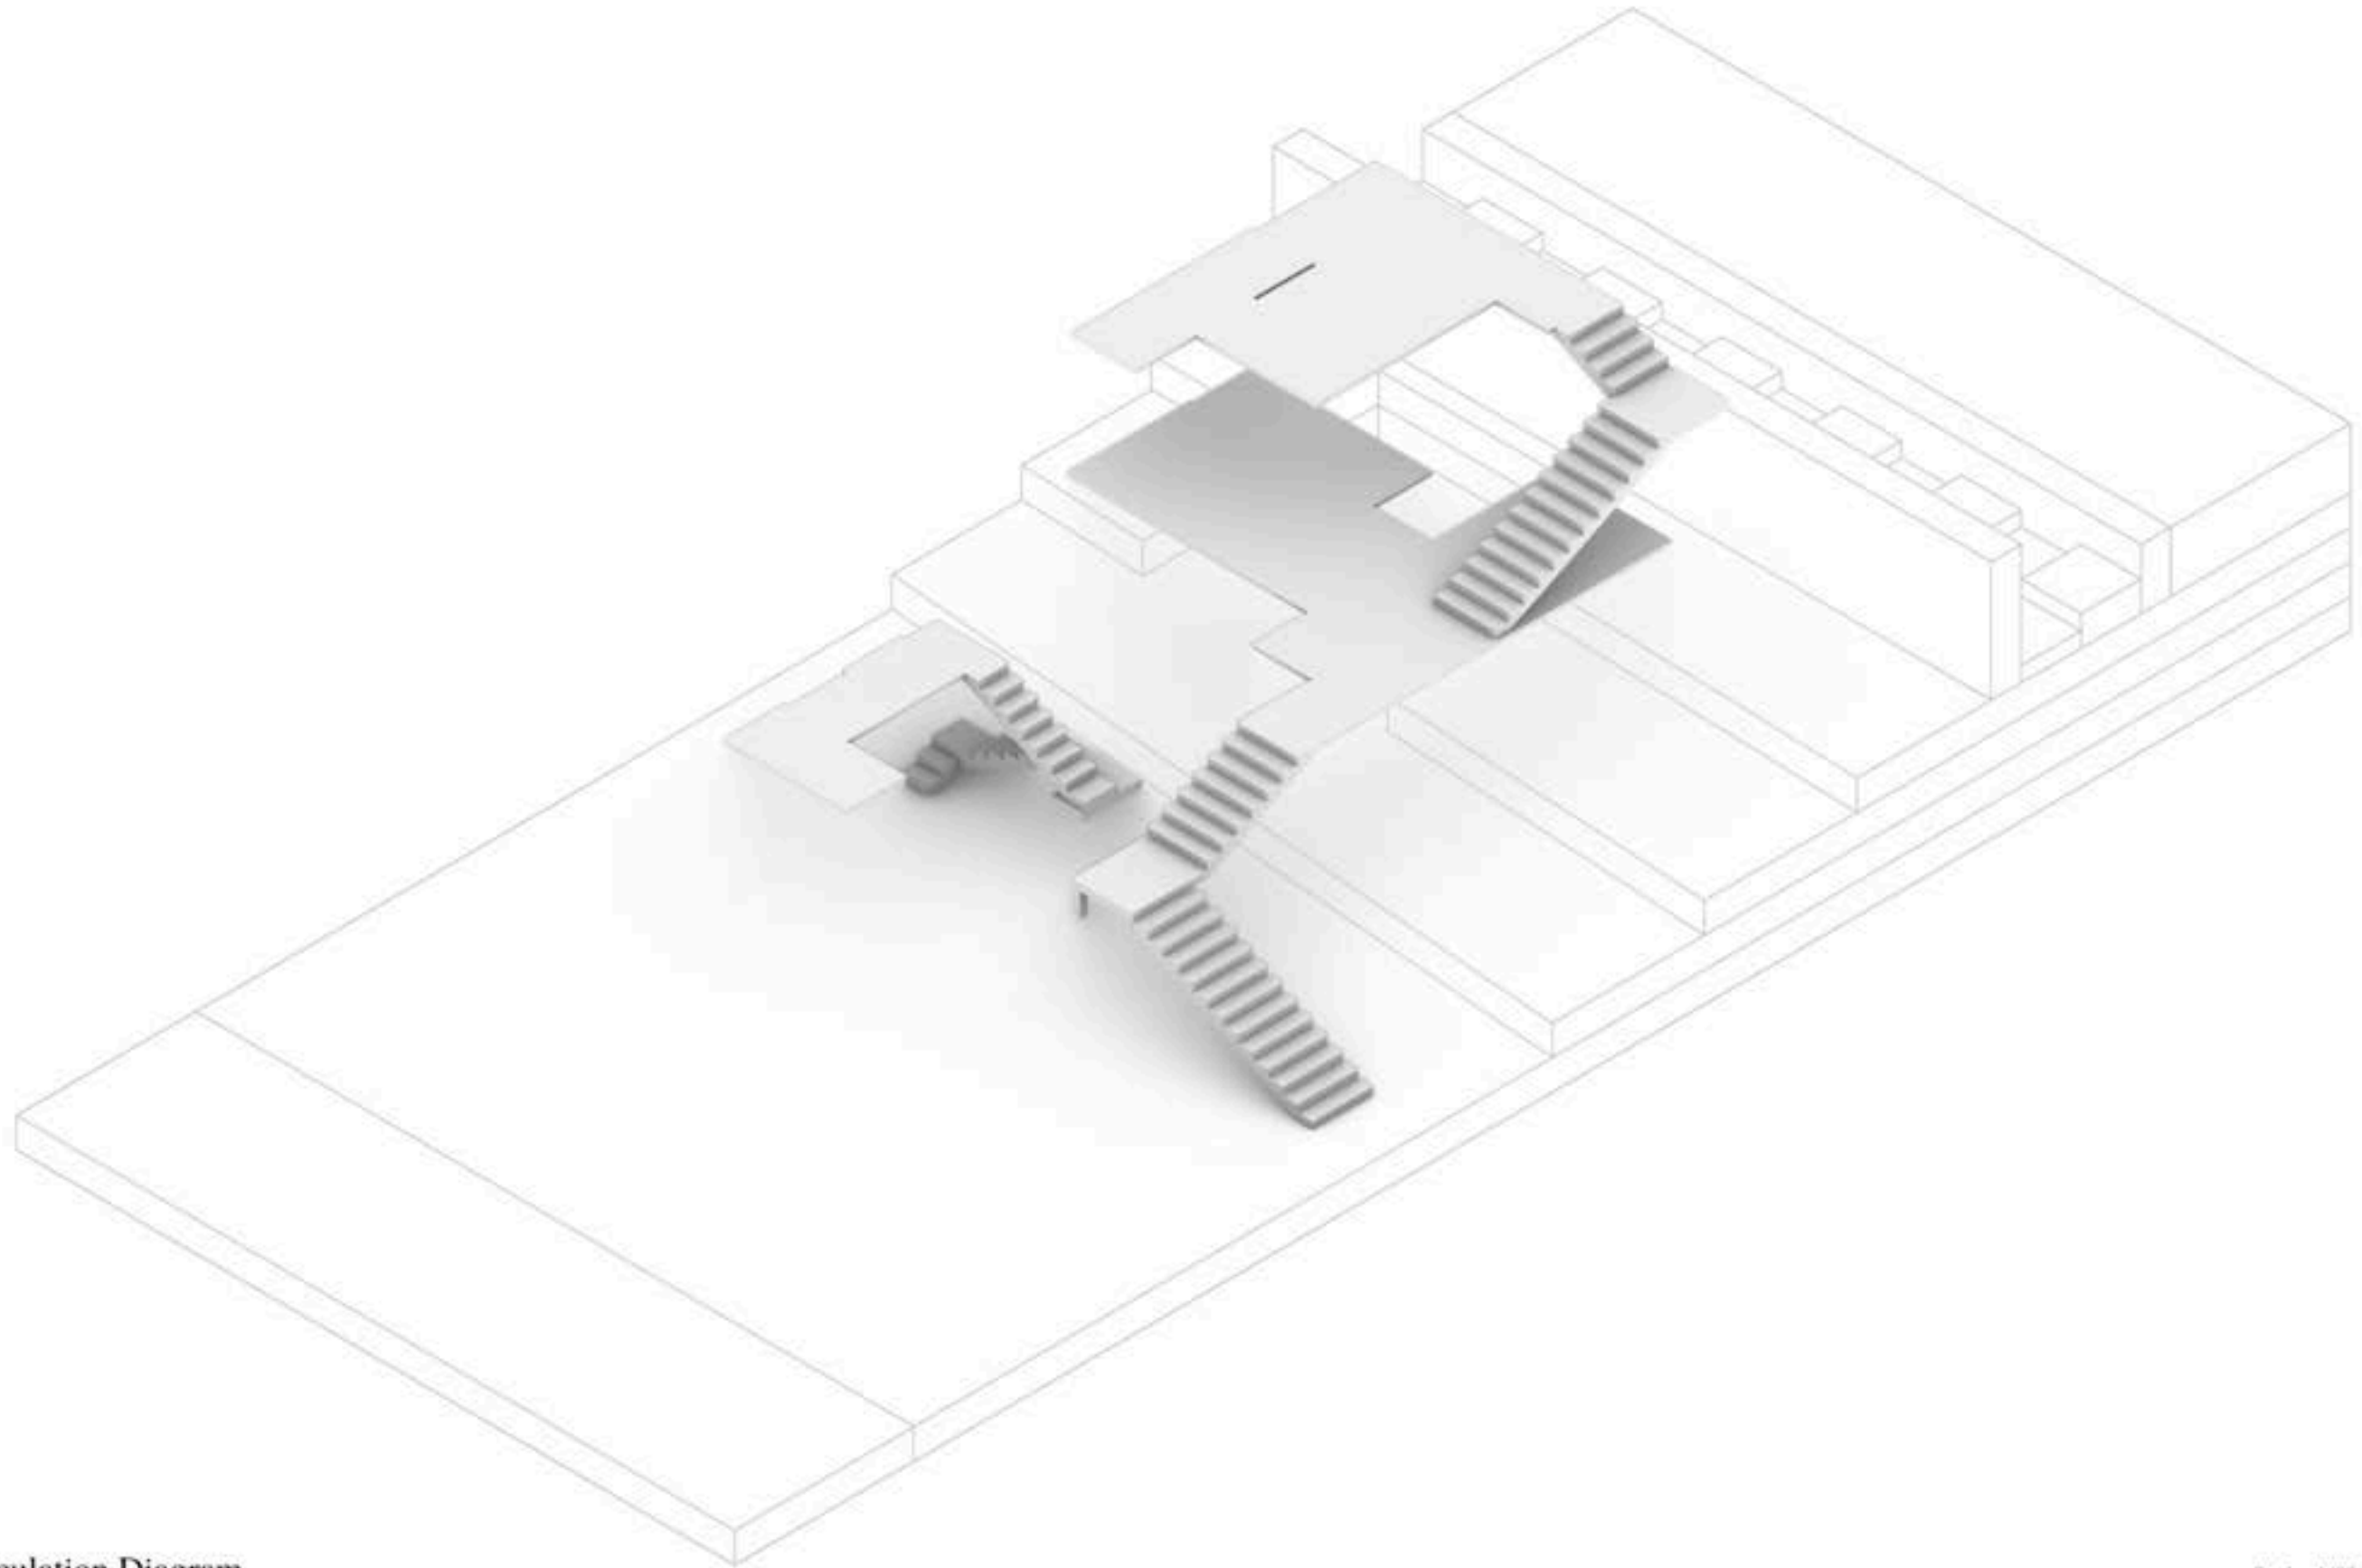


Circulation Diagram

Scale: 1/8" = 1'-0"


FINAL ENVIROMENTAL ENCLOSURES

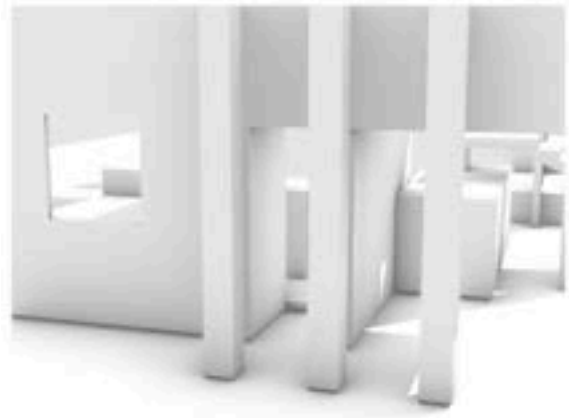

Entry
Horizon

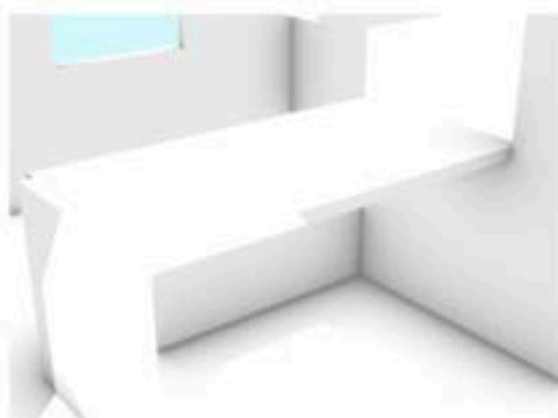


Living room
Horizon

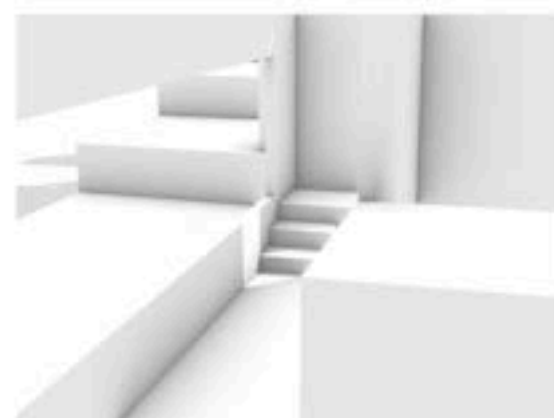

Hallway
Horizon



Stairs
Horizon

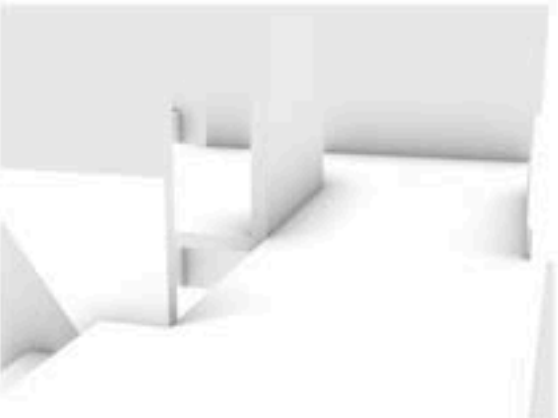

Second floor
Horizon




Recreational Room
Horizon




Soccer Field
Sky



Second Entry
Sky

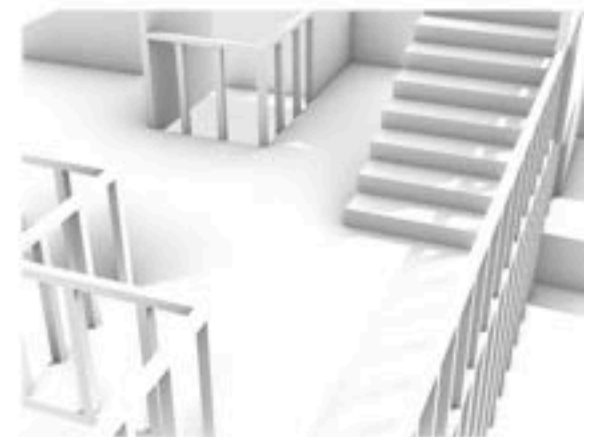


Second level
Sky

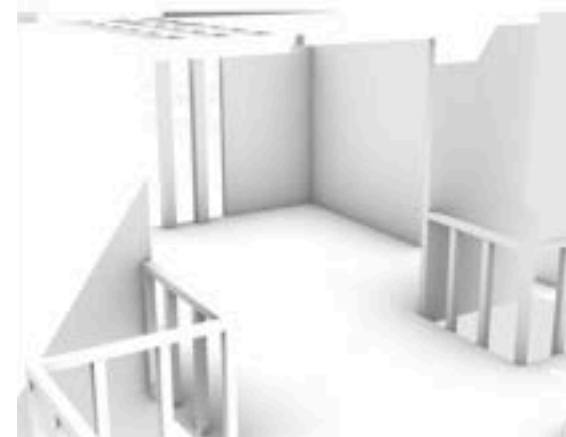

Bedroom
Sky




Third Floor Entry
Sky

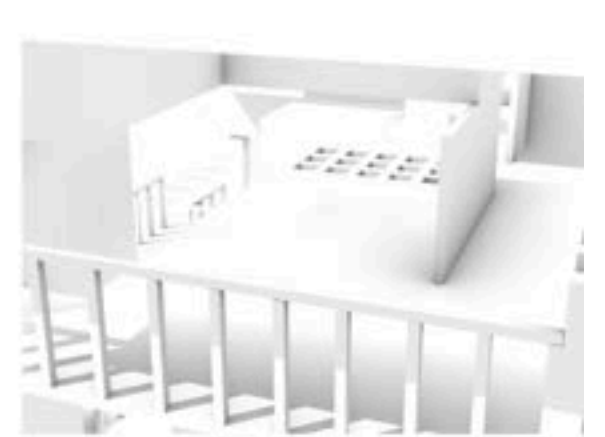


Balcony
Sky

FINAL SITE ISOMETRIC

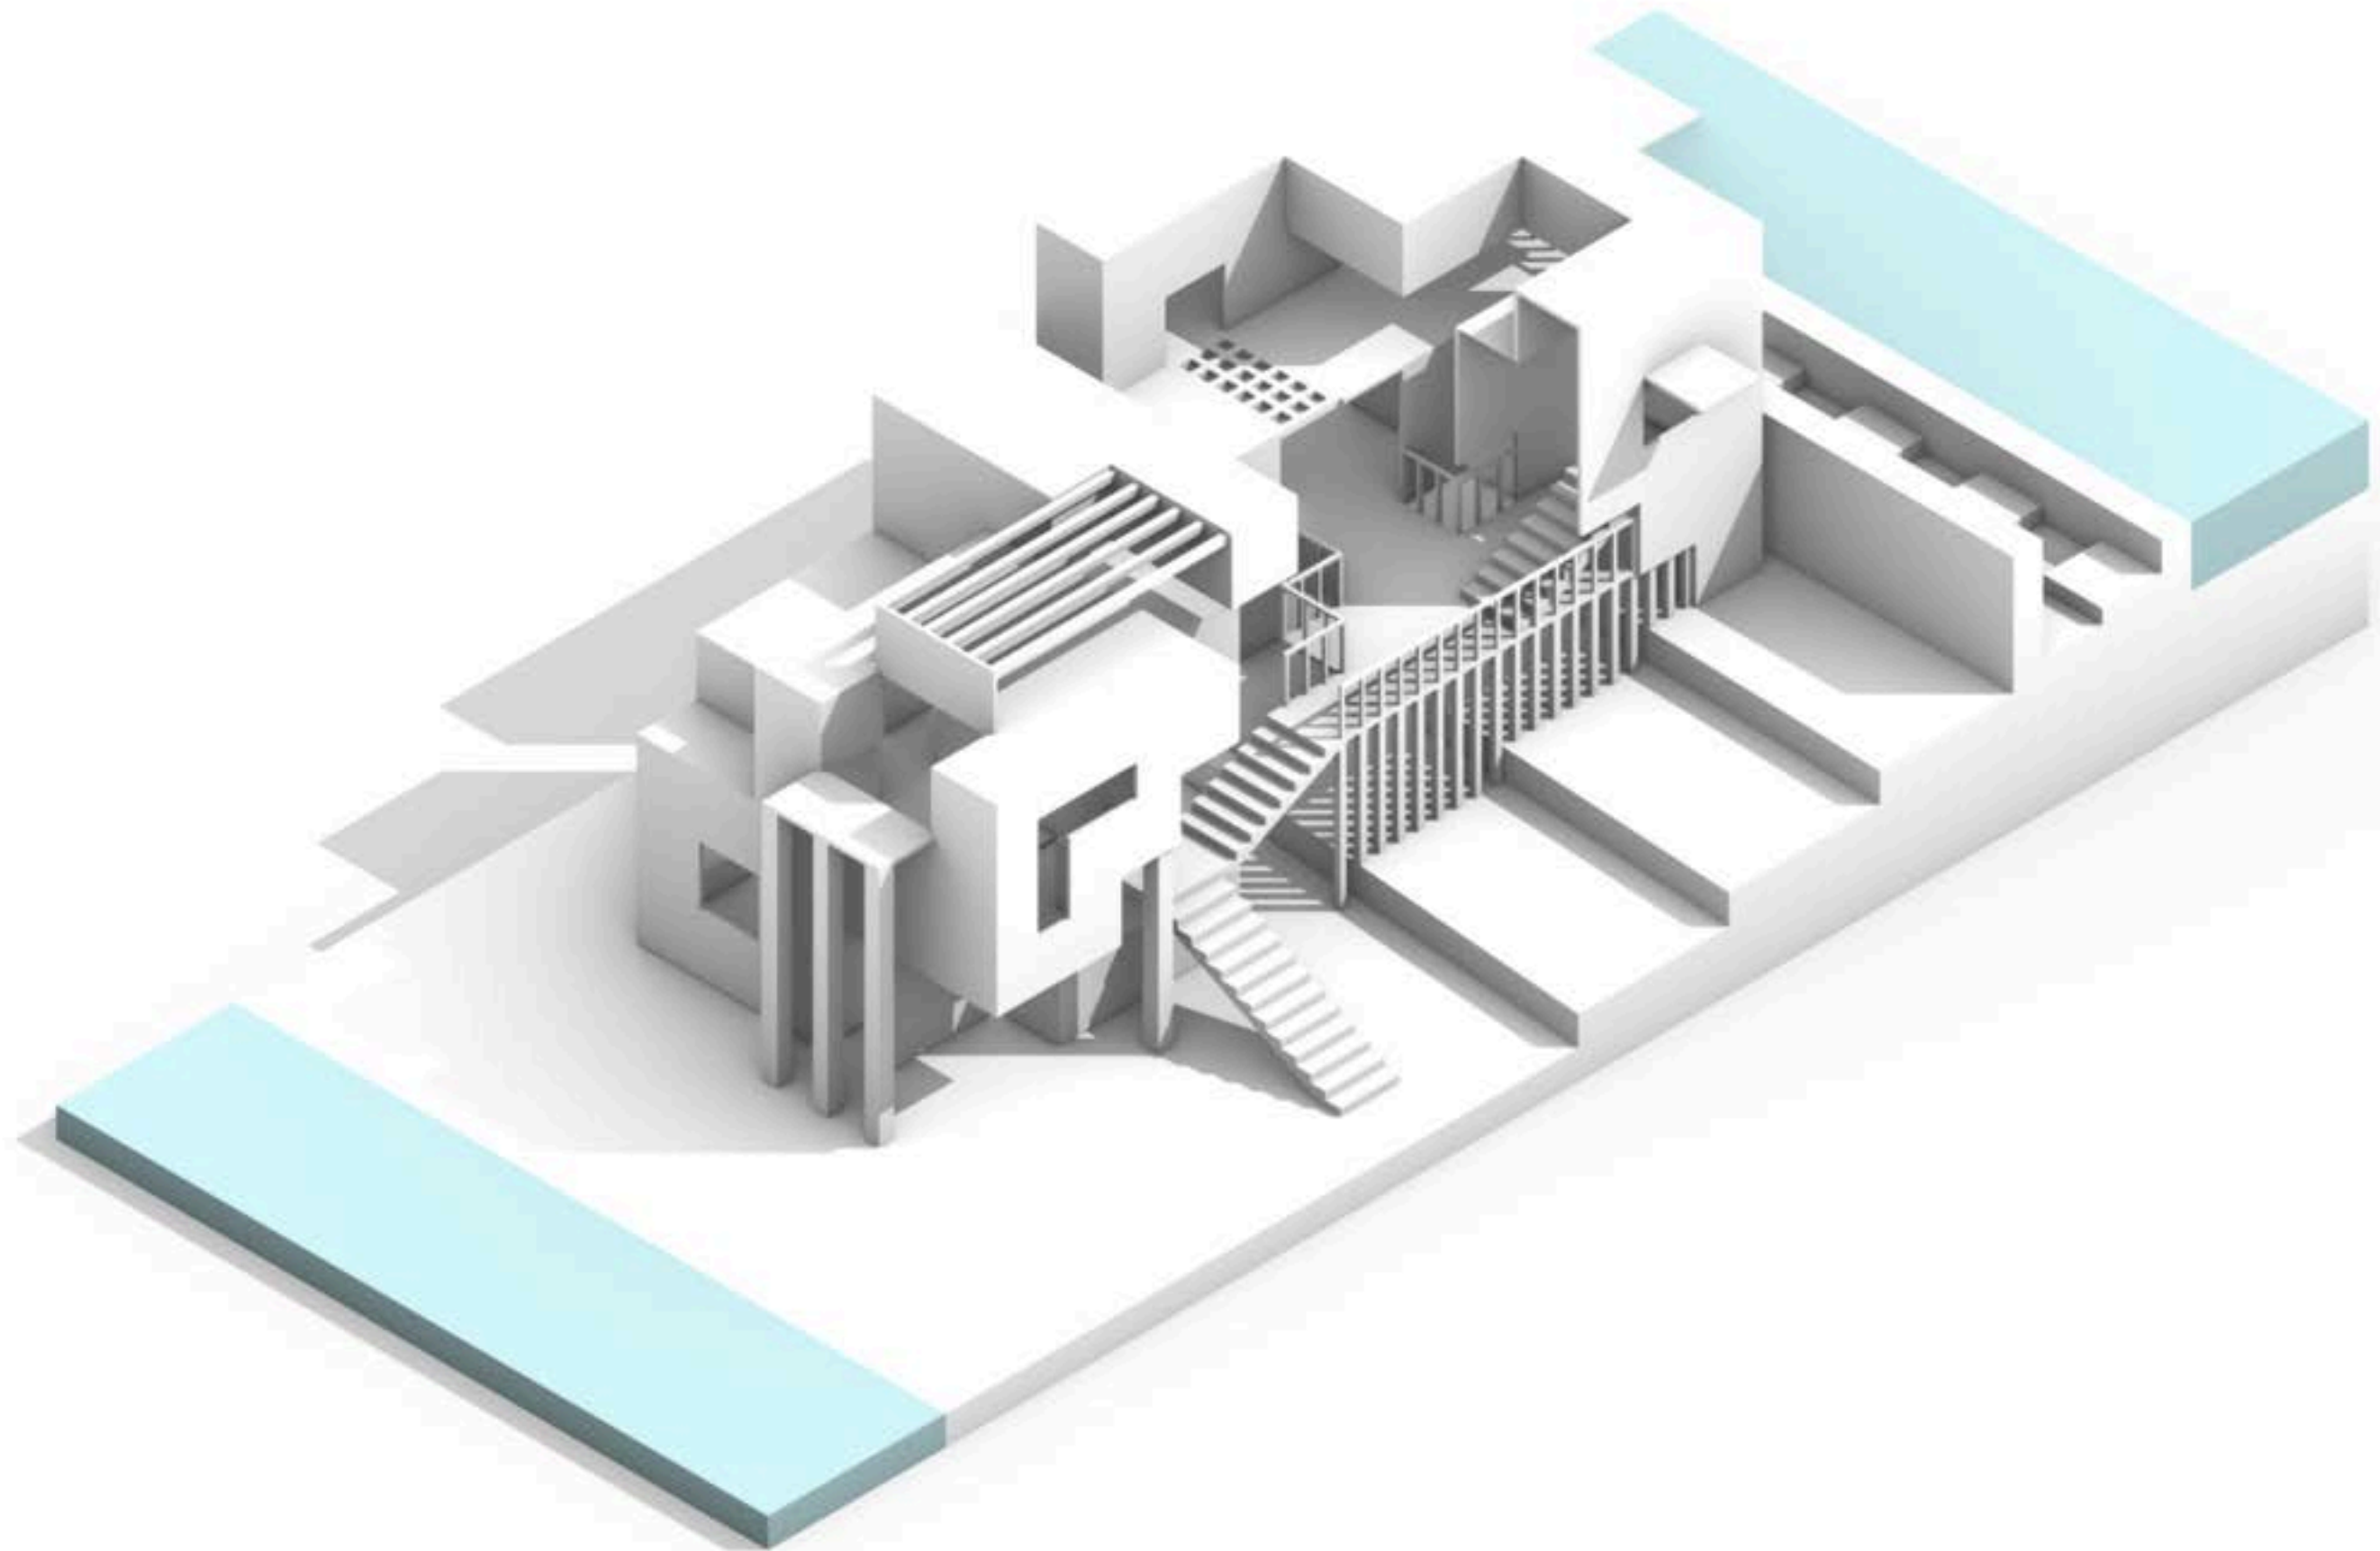

FINAL PHYSICAL MODEL

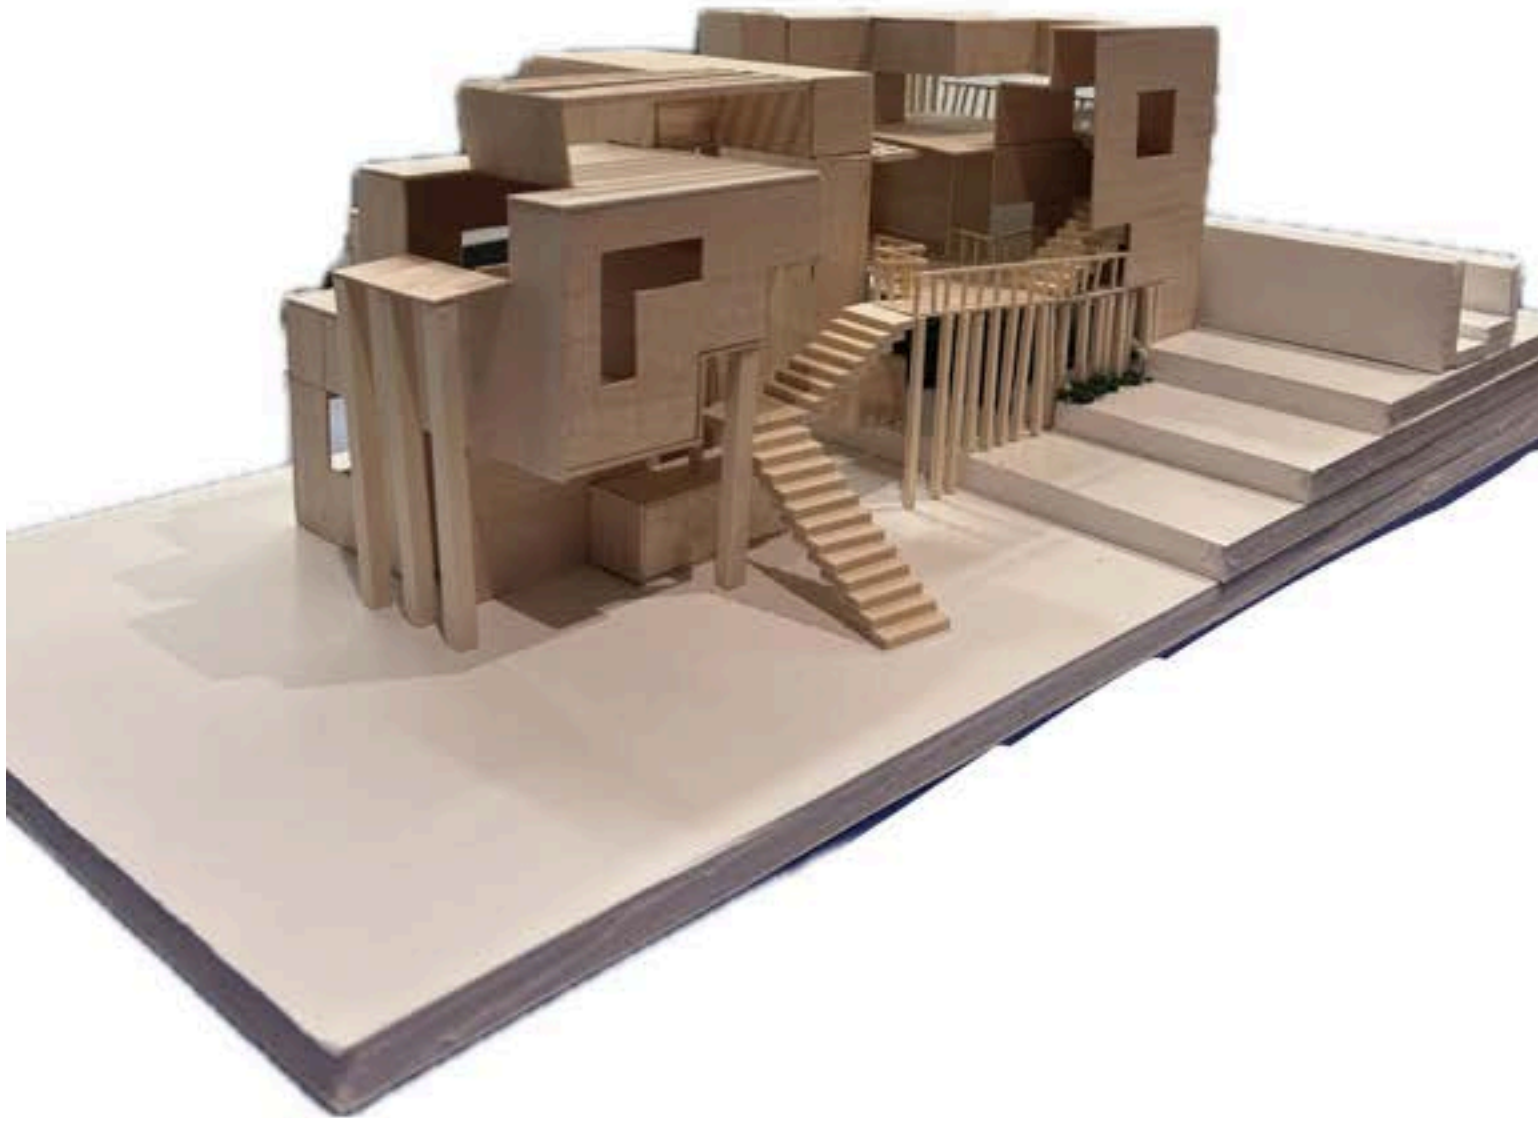

2 N D
S E M E S T E R

Narrative





The name of the painting is *Study for a Painting*, made in **1939** by the artist **Ad Reinhardt**. I chose this painting because I saw the potential of the objects and colors. I created three scenes based on a story of a little kid.

The volumes talk about a kid that (**scene 1**) was playing in his bedroom with his videogames, then suddenly his family tells him that they are going to visit Grandma down in Texas. The kid gets ready and prepares himself for the different setting and weather. When they got in the car, they started exploring the surroundings and the kid found a little armadillo (**scene 2**) next to a cactus in the middle of a little dessert on the way to Grandma's house. After a long trip from the kid's house to Texas, they arrived at the house and his Grandma was outside in the garden. At that moment (**scene 3**) the kid notices a little snail on the grass lifting a rose petal right next to a seed. The whole family spent the whole week at Grandma's house and the best things the kid remembered were the scenes. The building represents the little journey of a child in another state with new things to discover and see, highlighting the innocence and simplicity of the shapes that the painting had.



PAINTING TRACING + ELEMENTS

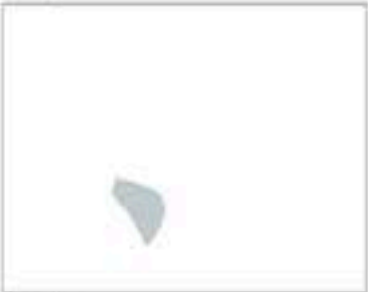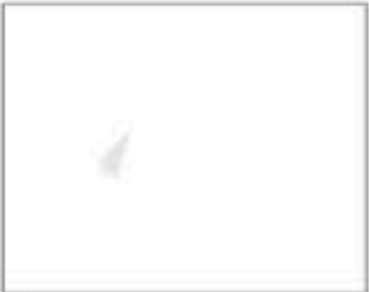


Background				
Cactus				
Middle Ground				
Foreground				
Boot with a stick				

SCENE 1 - 2 - 3


Game-room

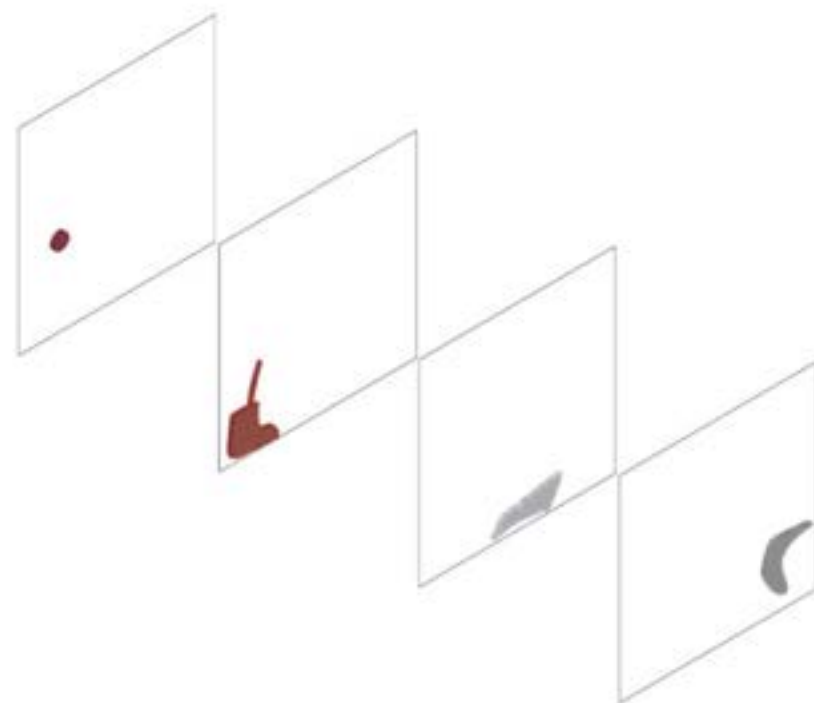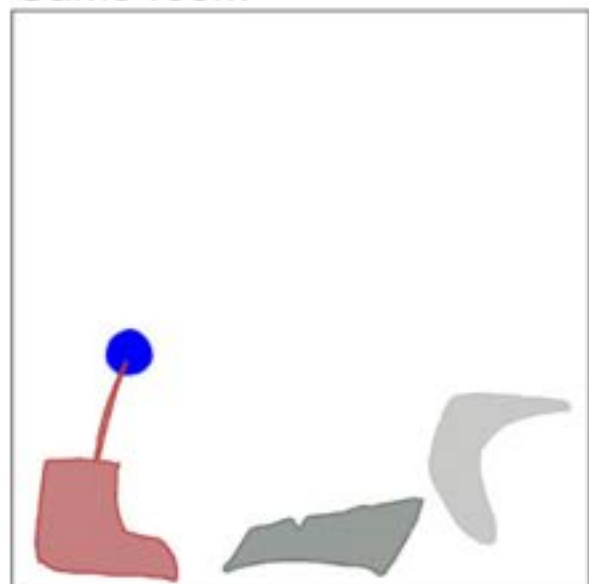

Armadillo in a Desert

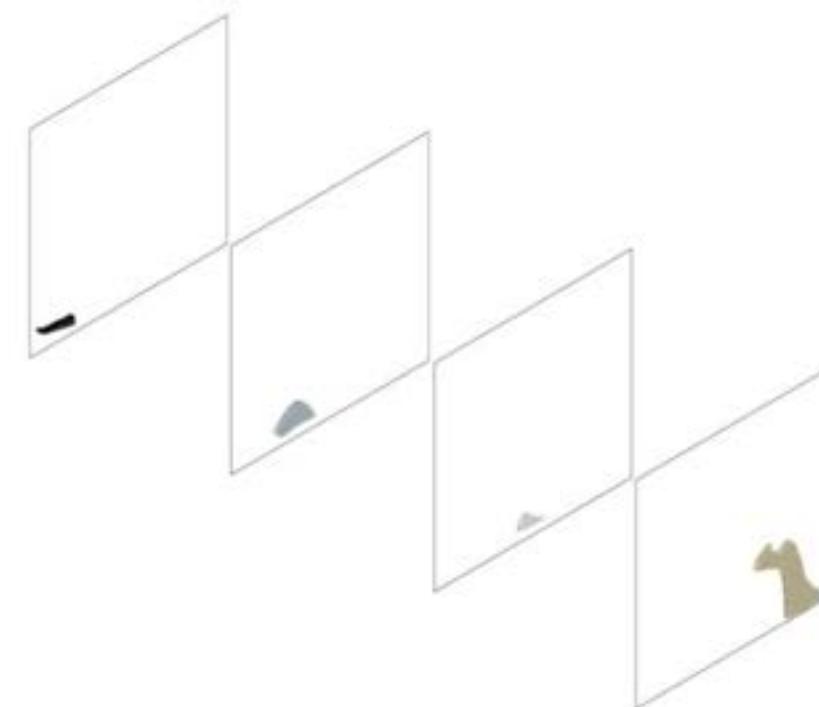




Garden

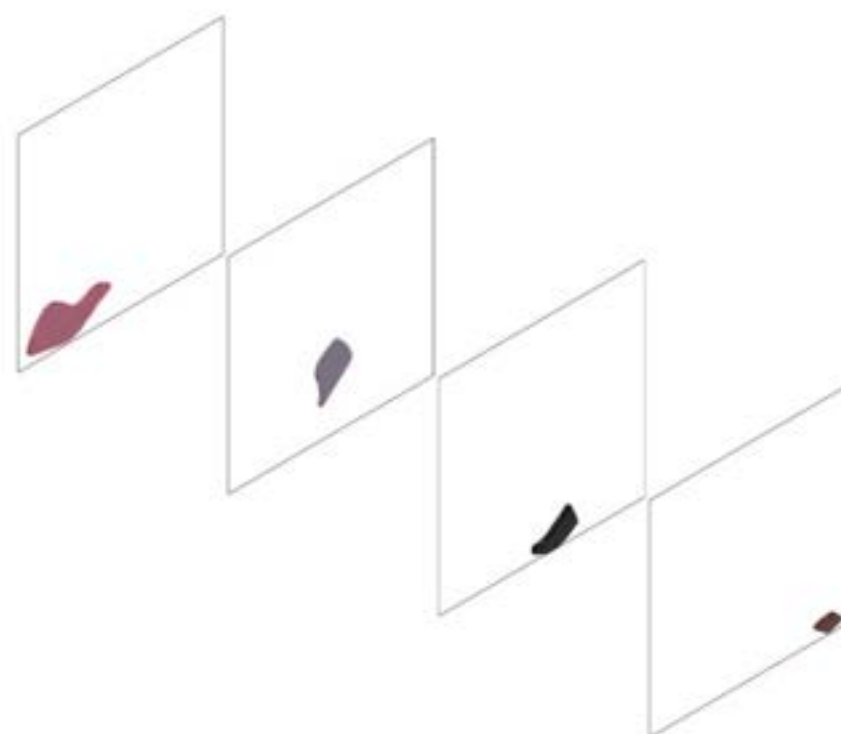


GRID OF VOLUMES




VOLUMETRIC SCENE 1-2-3

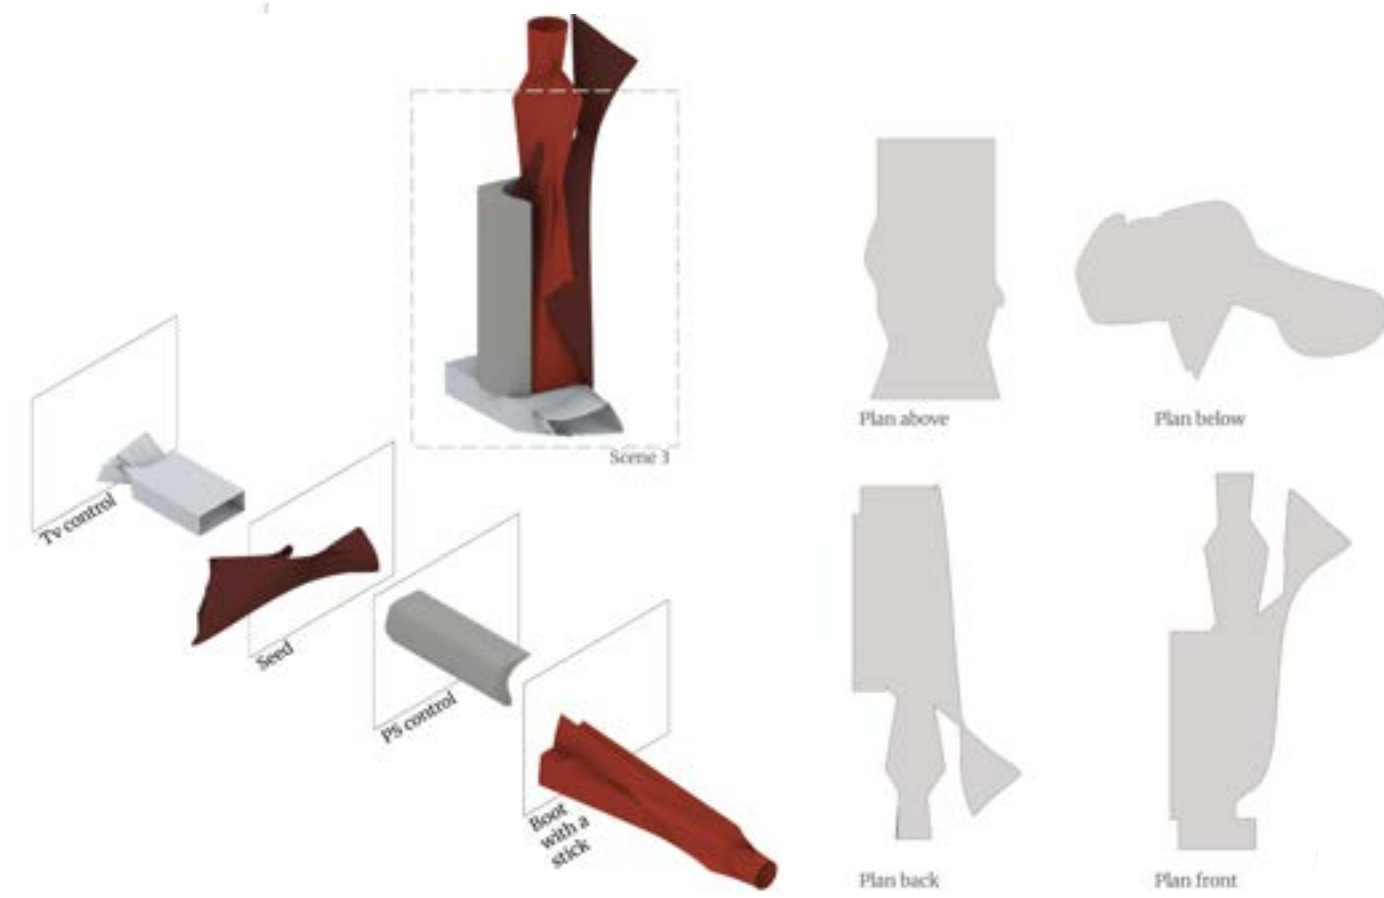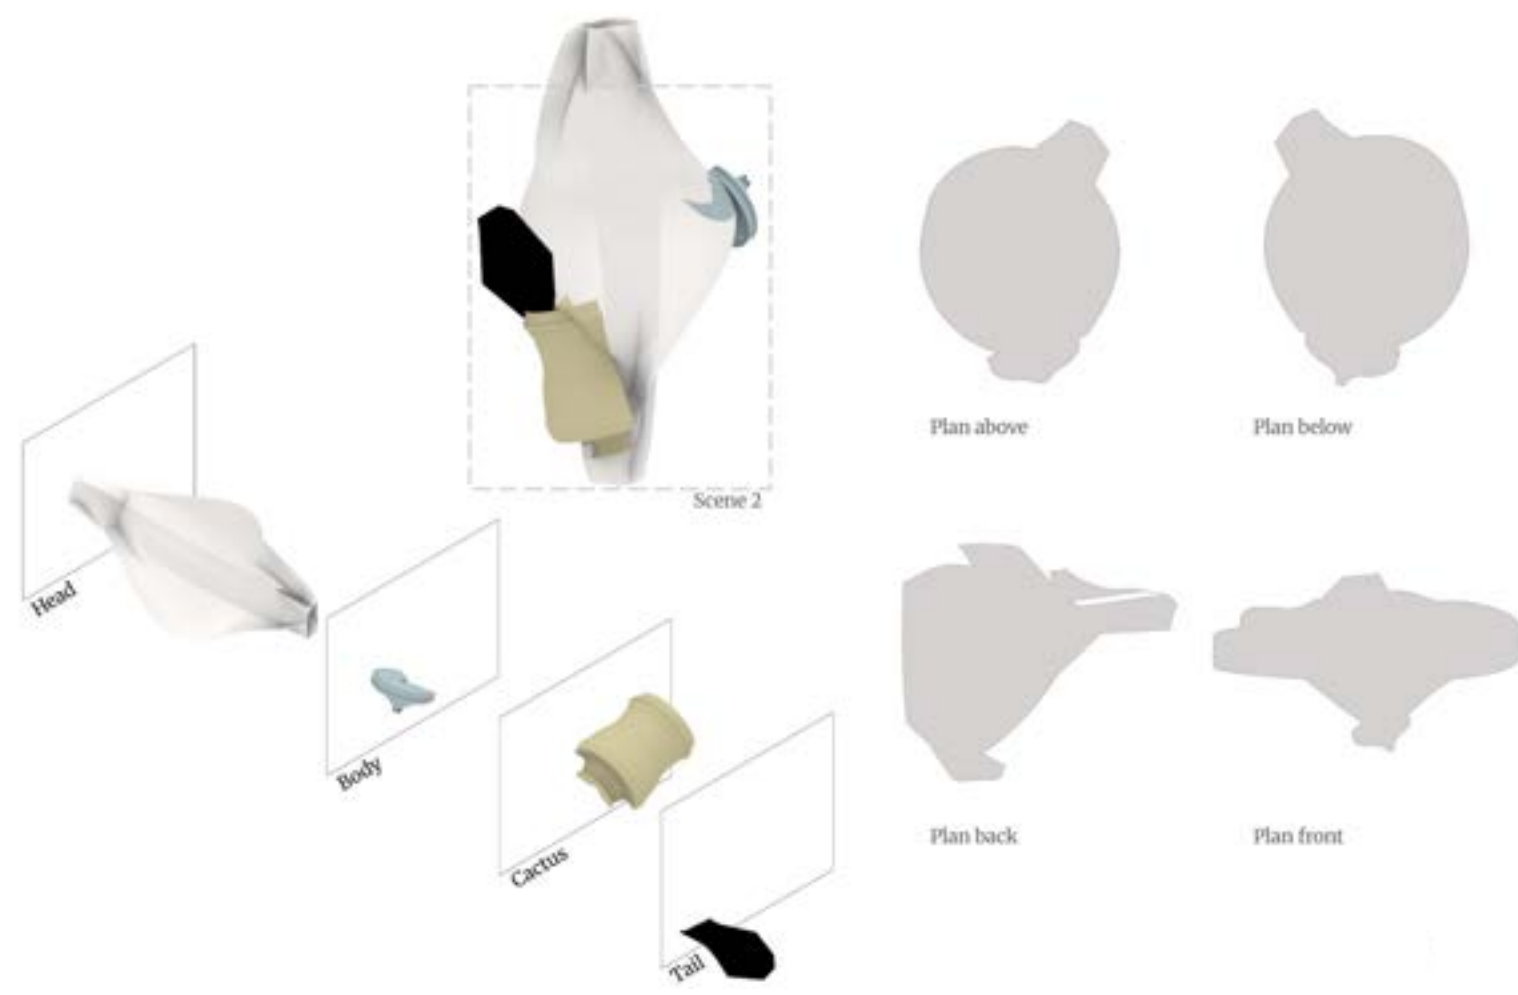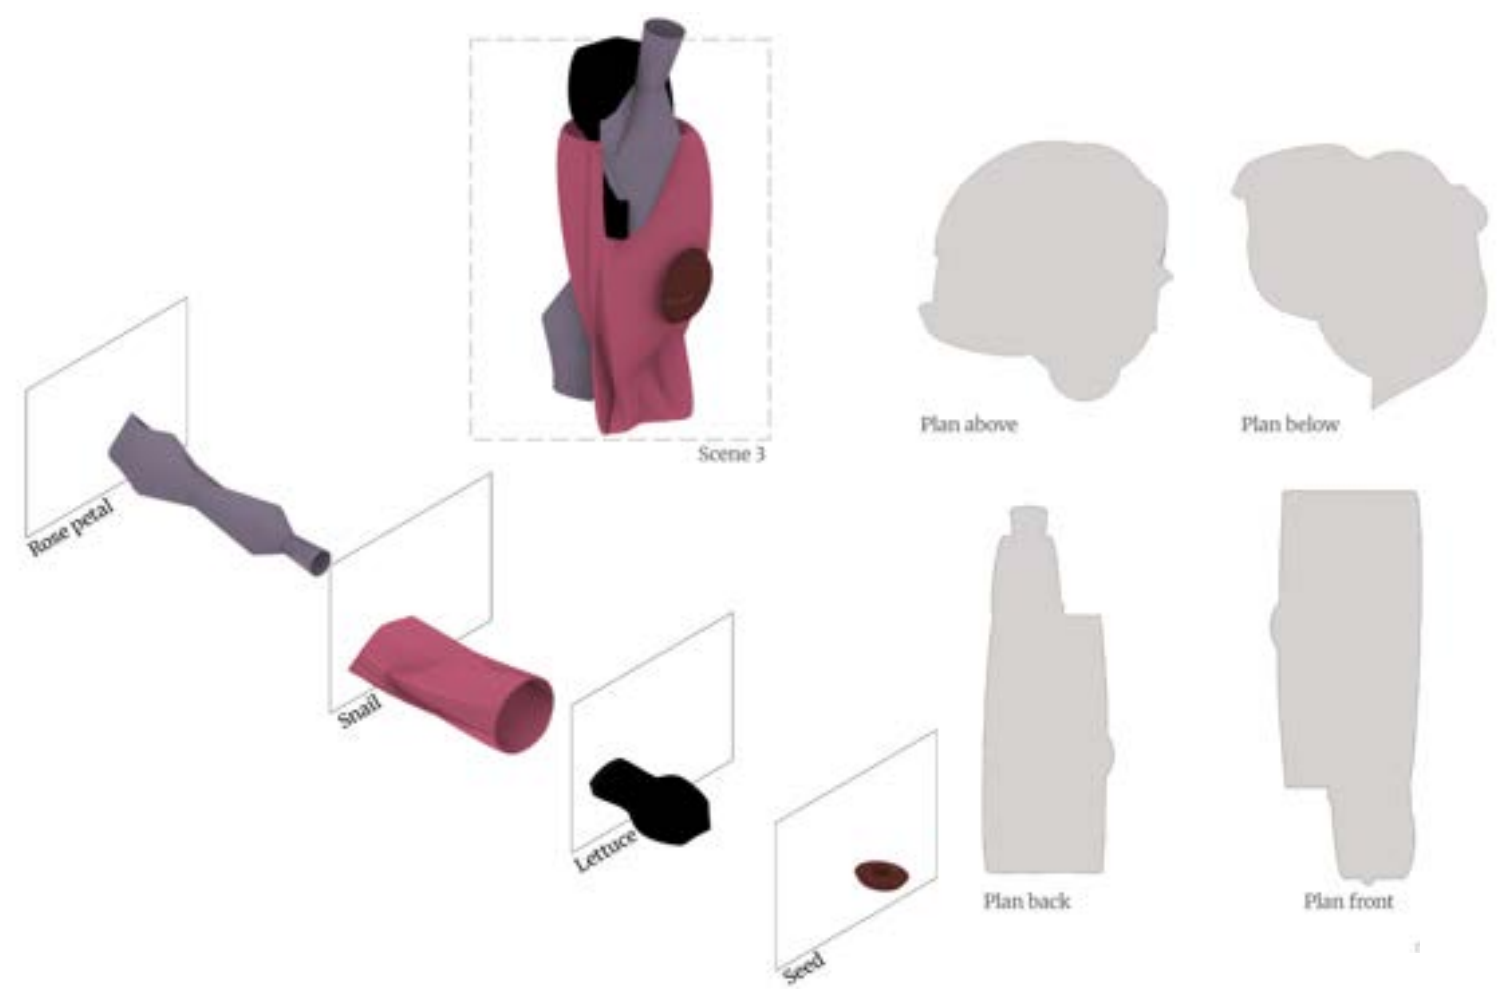


SPATIAL NARRATIVE 1 - ISOMETRIC

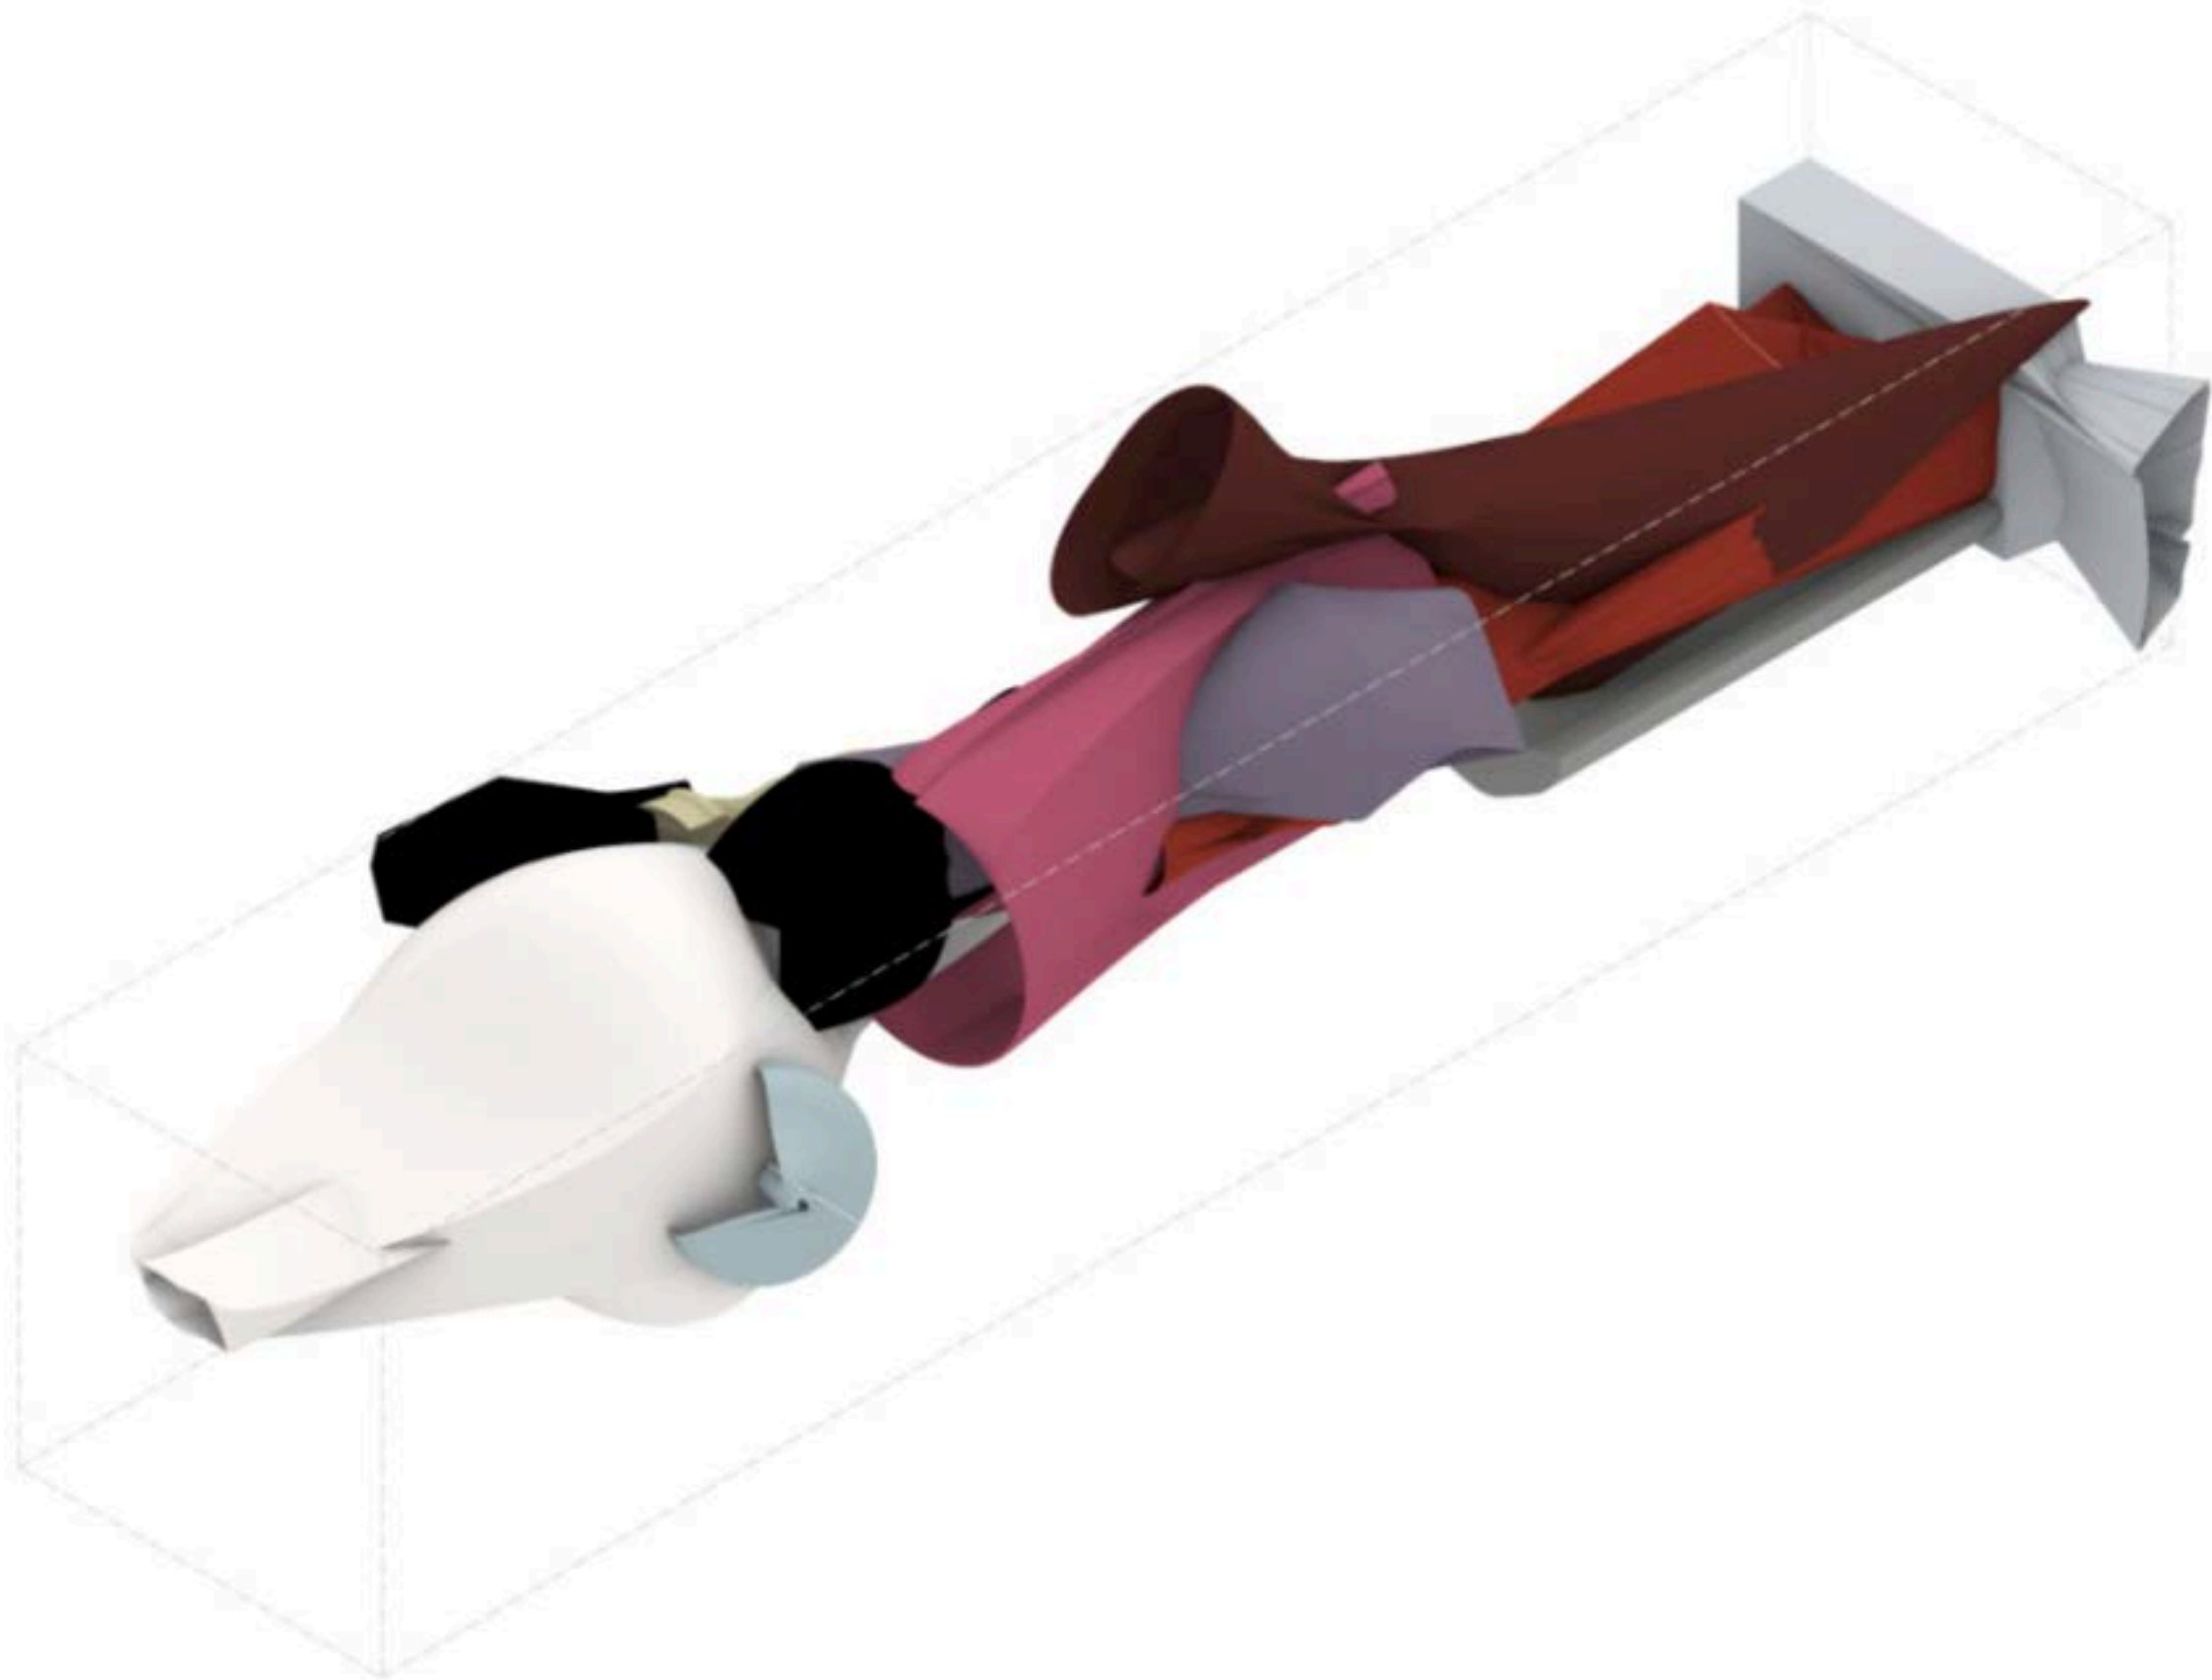

FLOOR PLANS

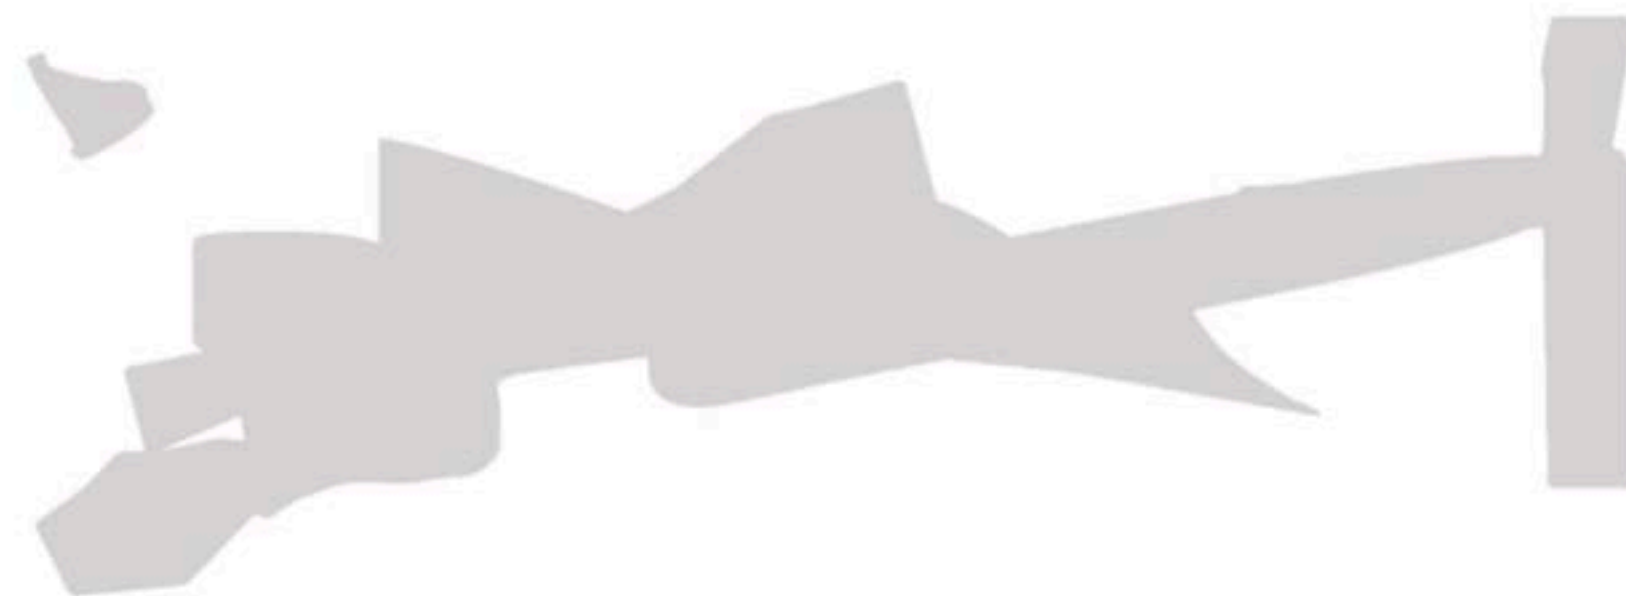

Floor Plan 1

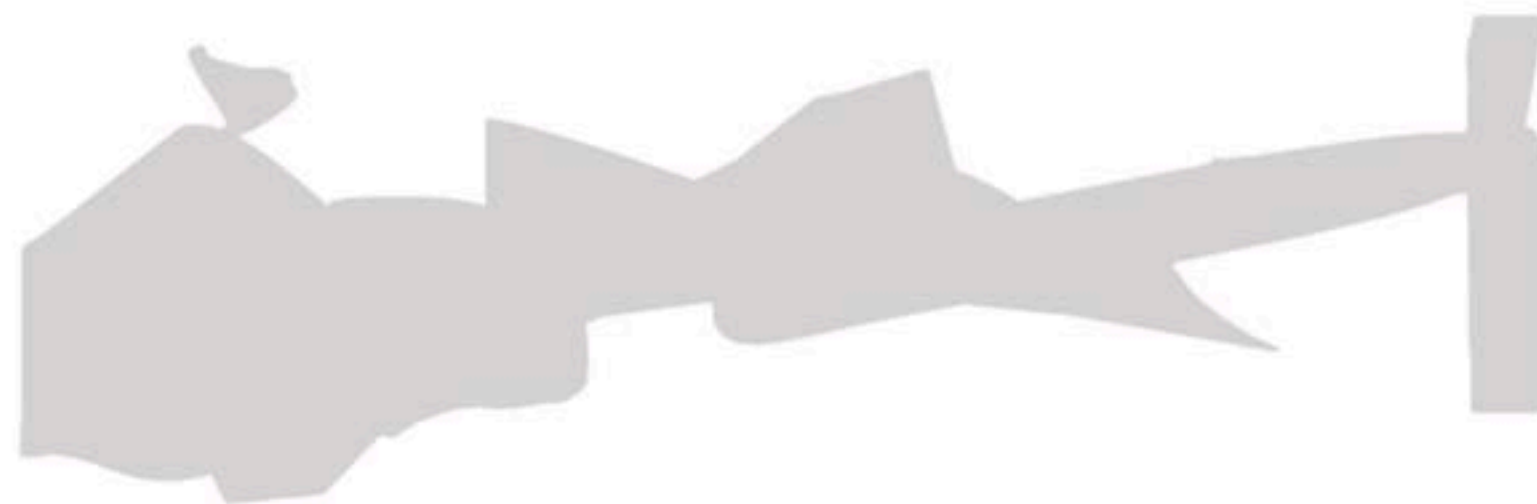

Floor Plan 2

- TRANSVERSE SECTIONS
- LONGITUDINAL SECTIONS



Transverse 1



Transverse 2



Transverse 3



Transverse 4



Transverse 5



Transverse 6



Longitudinal 1



Longitudinal 2



Transverse 1



Transverse 2



Transverse 3




Transverse 4




Transverse 5



Transverse 6

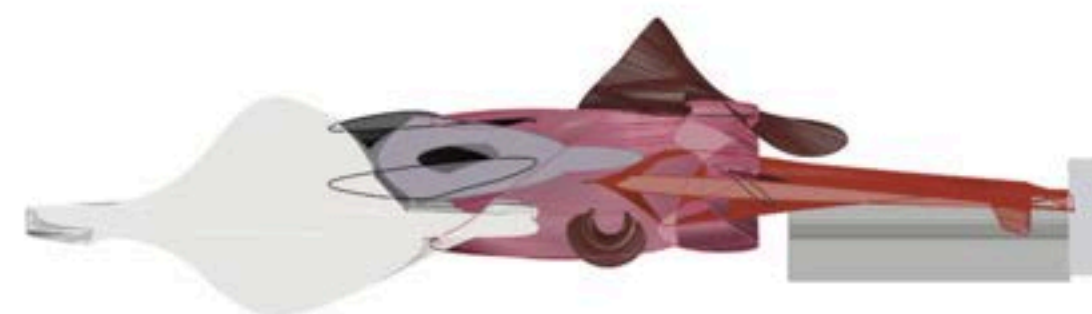


Longitudinal 1

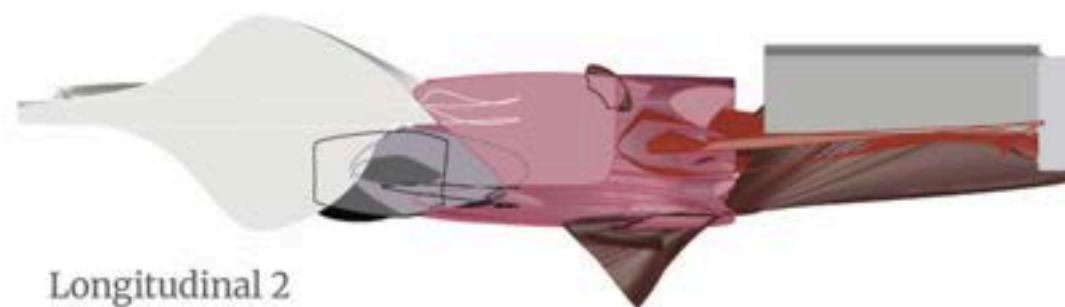


Longitudinal 2

- TRANSVERSE ELEVATIONS
- LONGITUDINAL ELEVATIONS

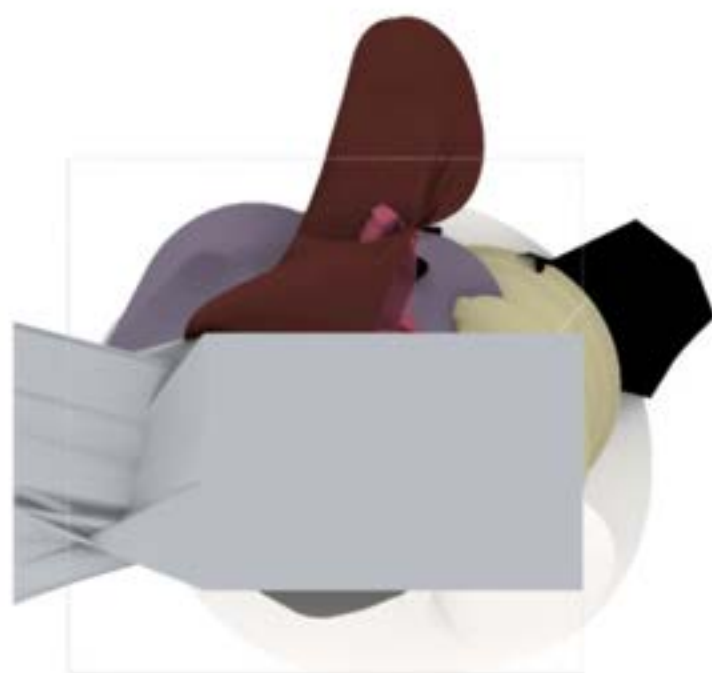


Front

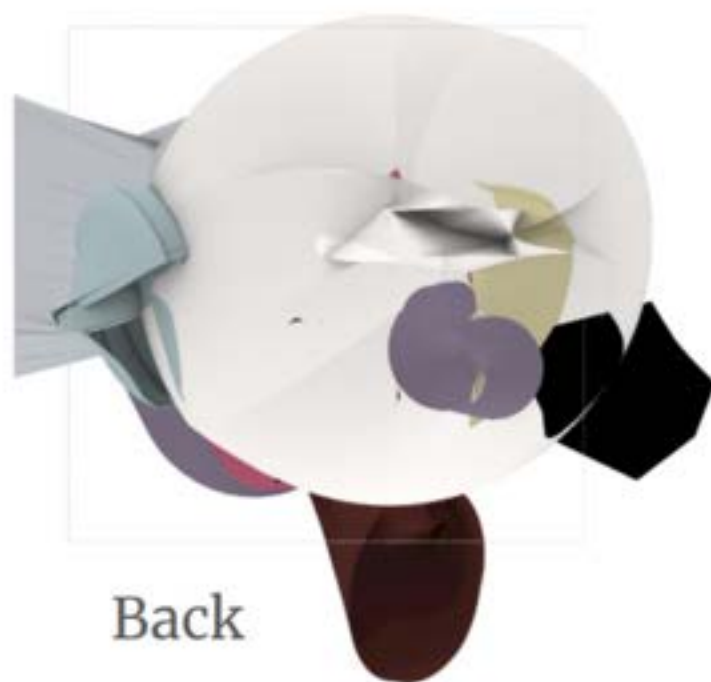

Back




Right View

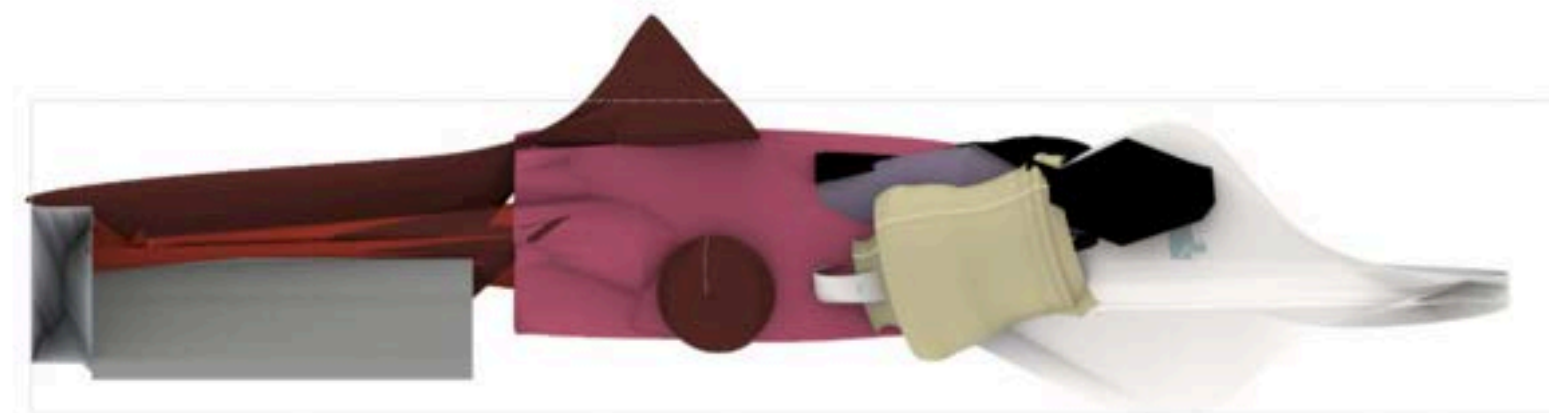


Left View









S I T E

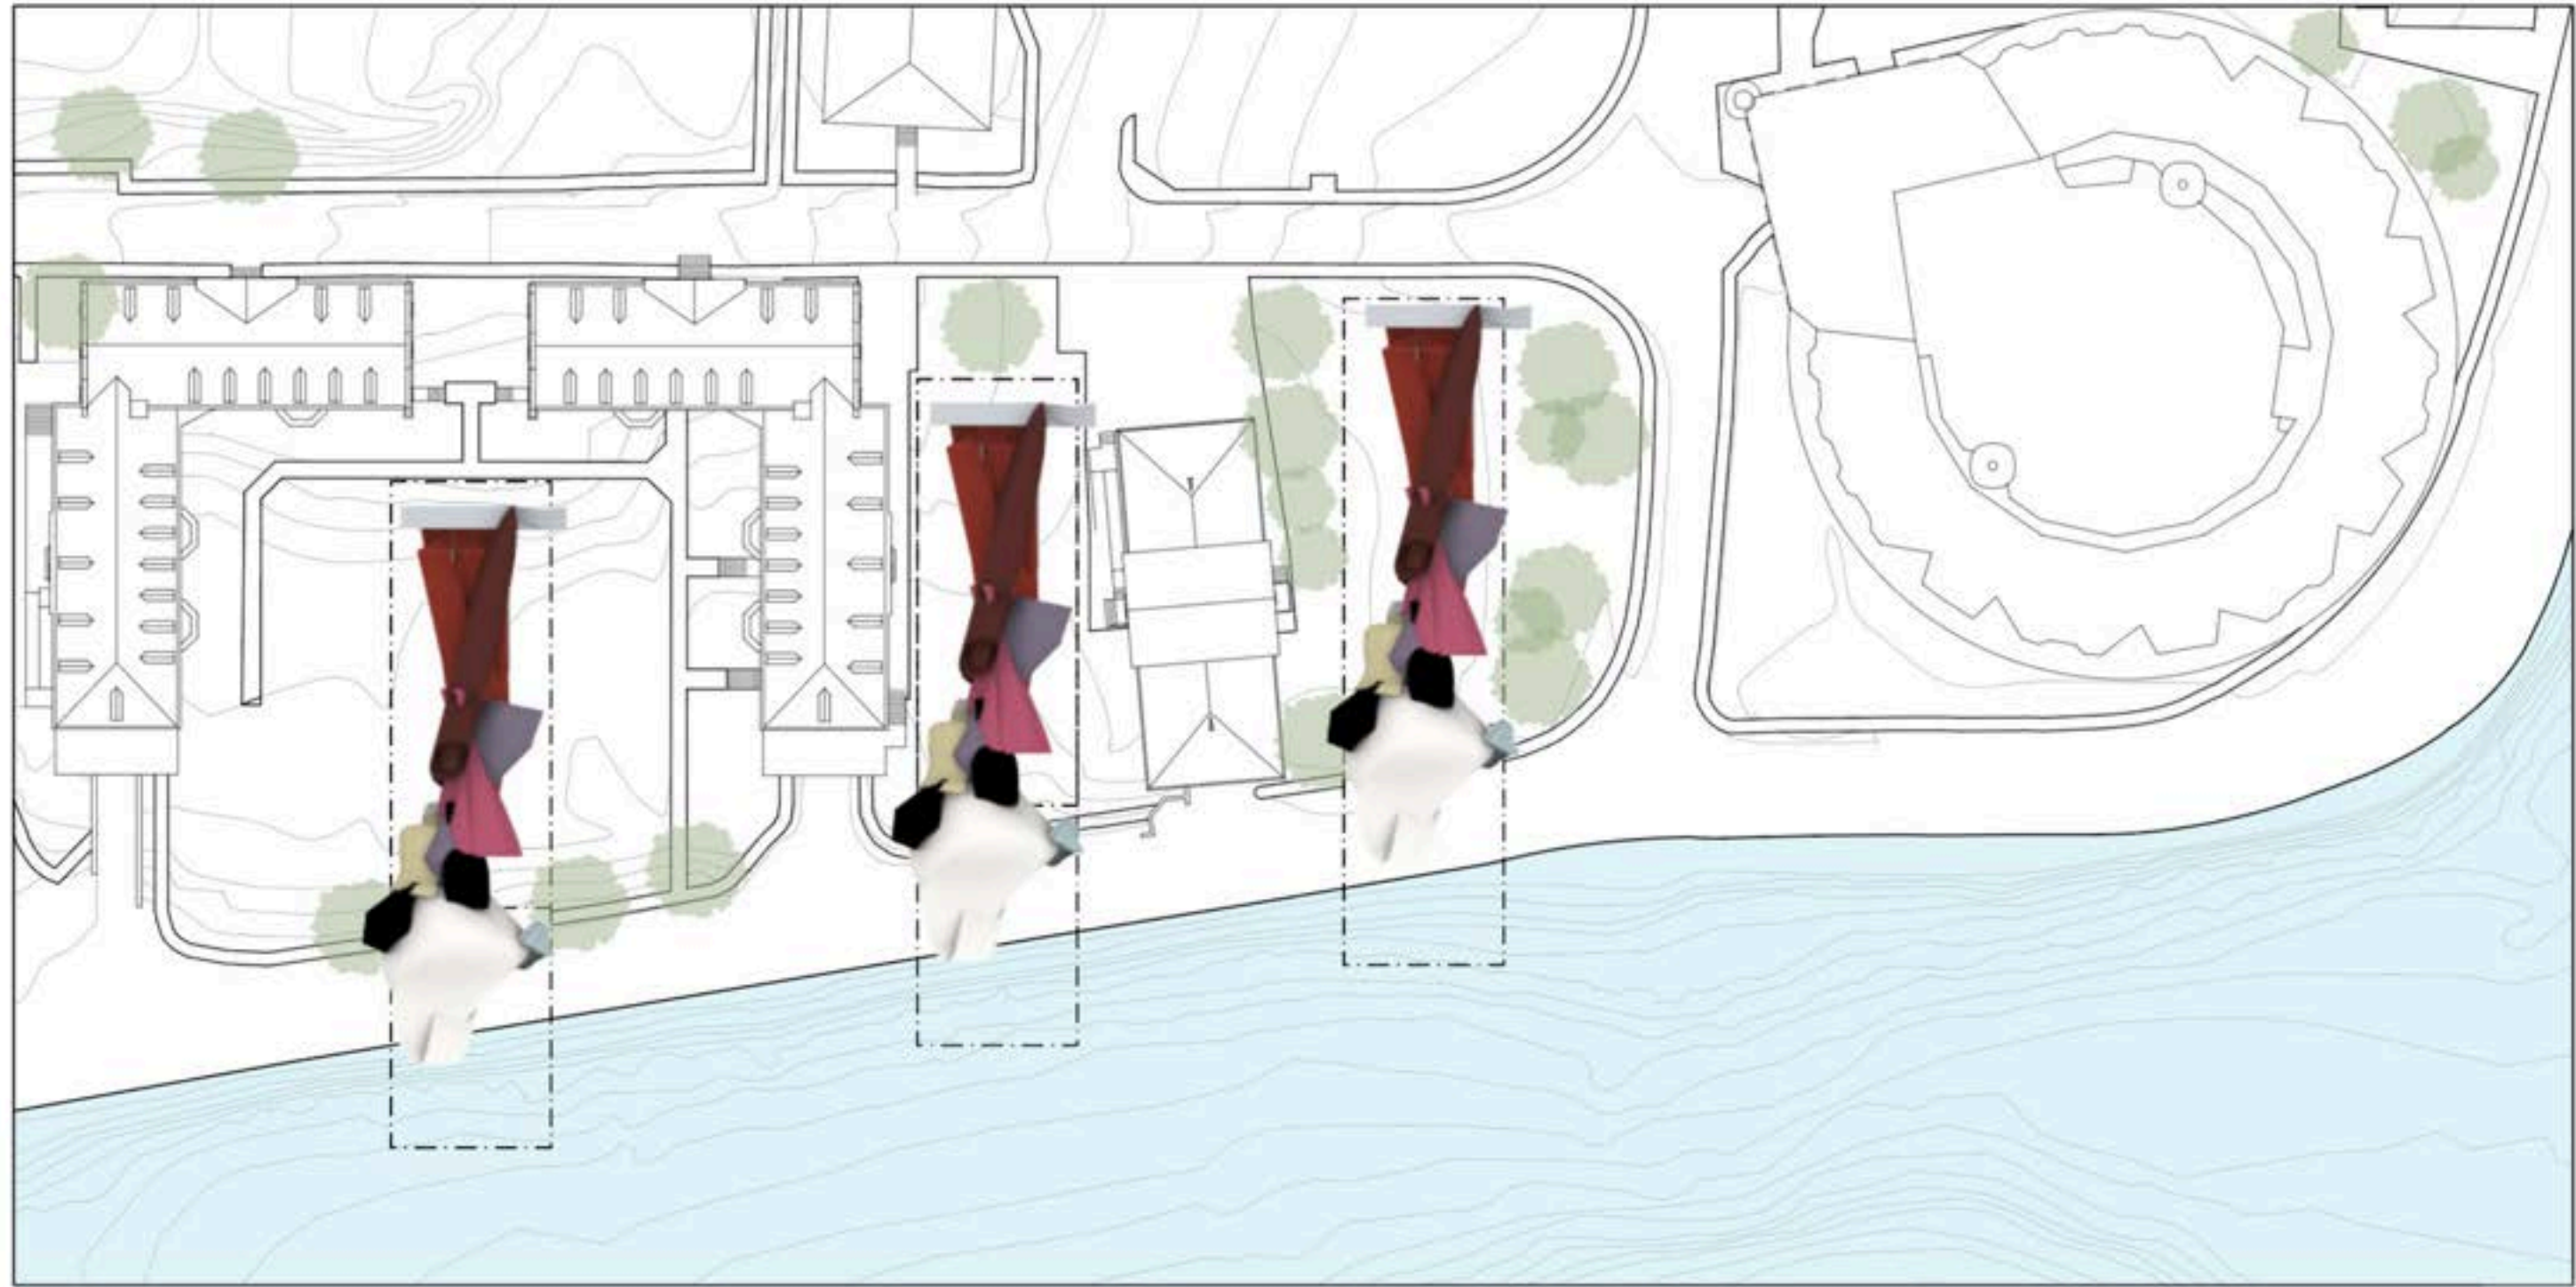


FINAL MODEL ISOMETRIC

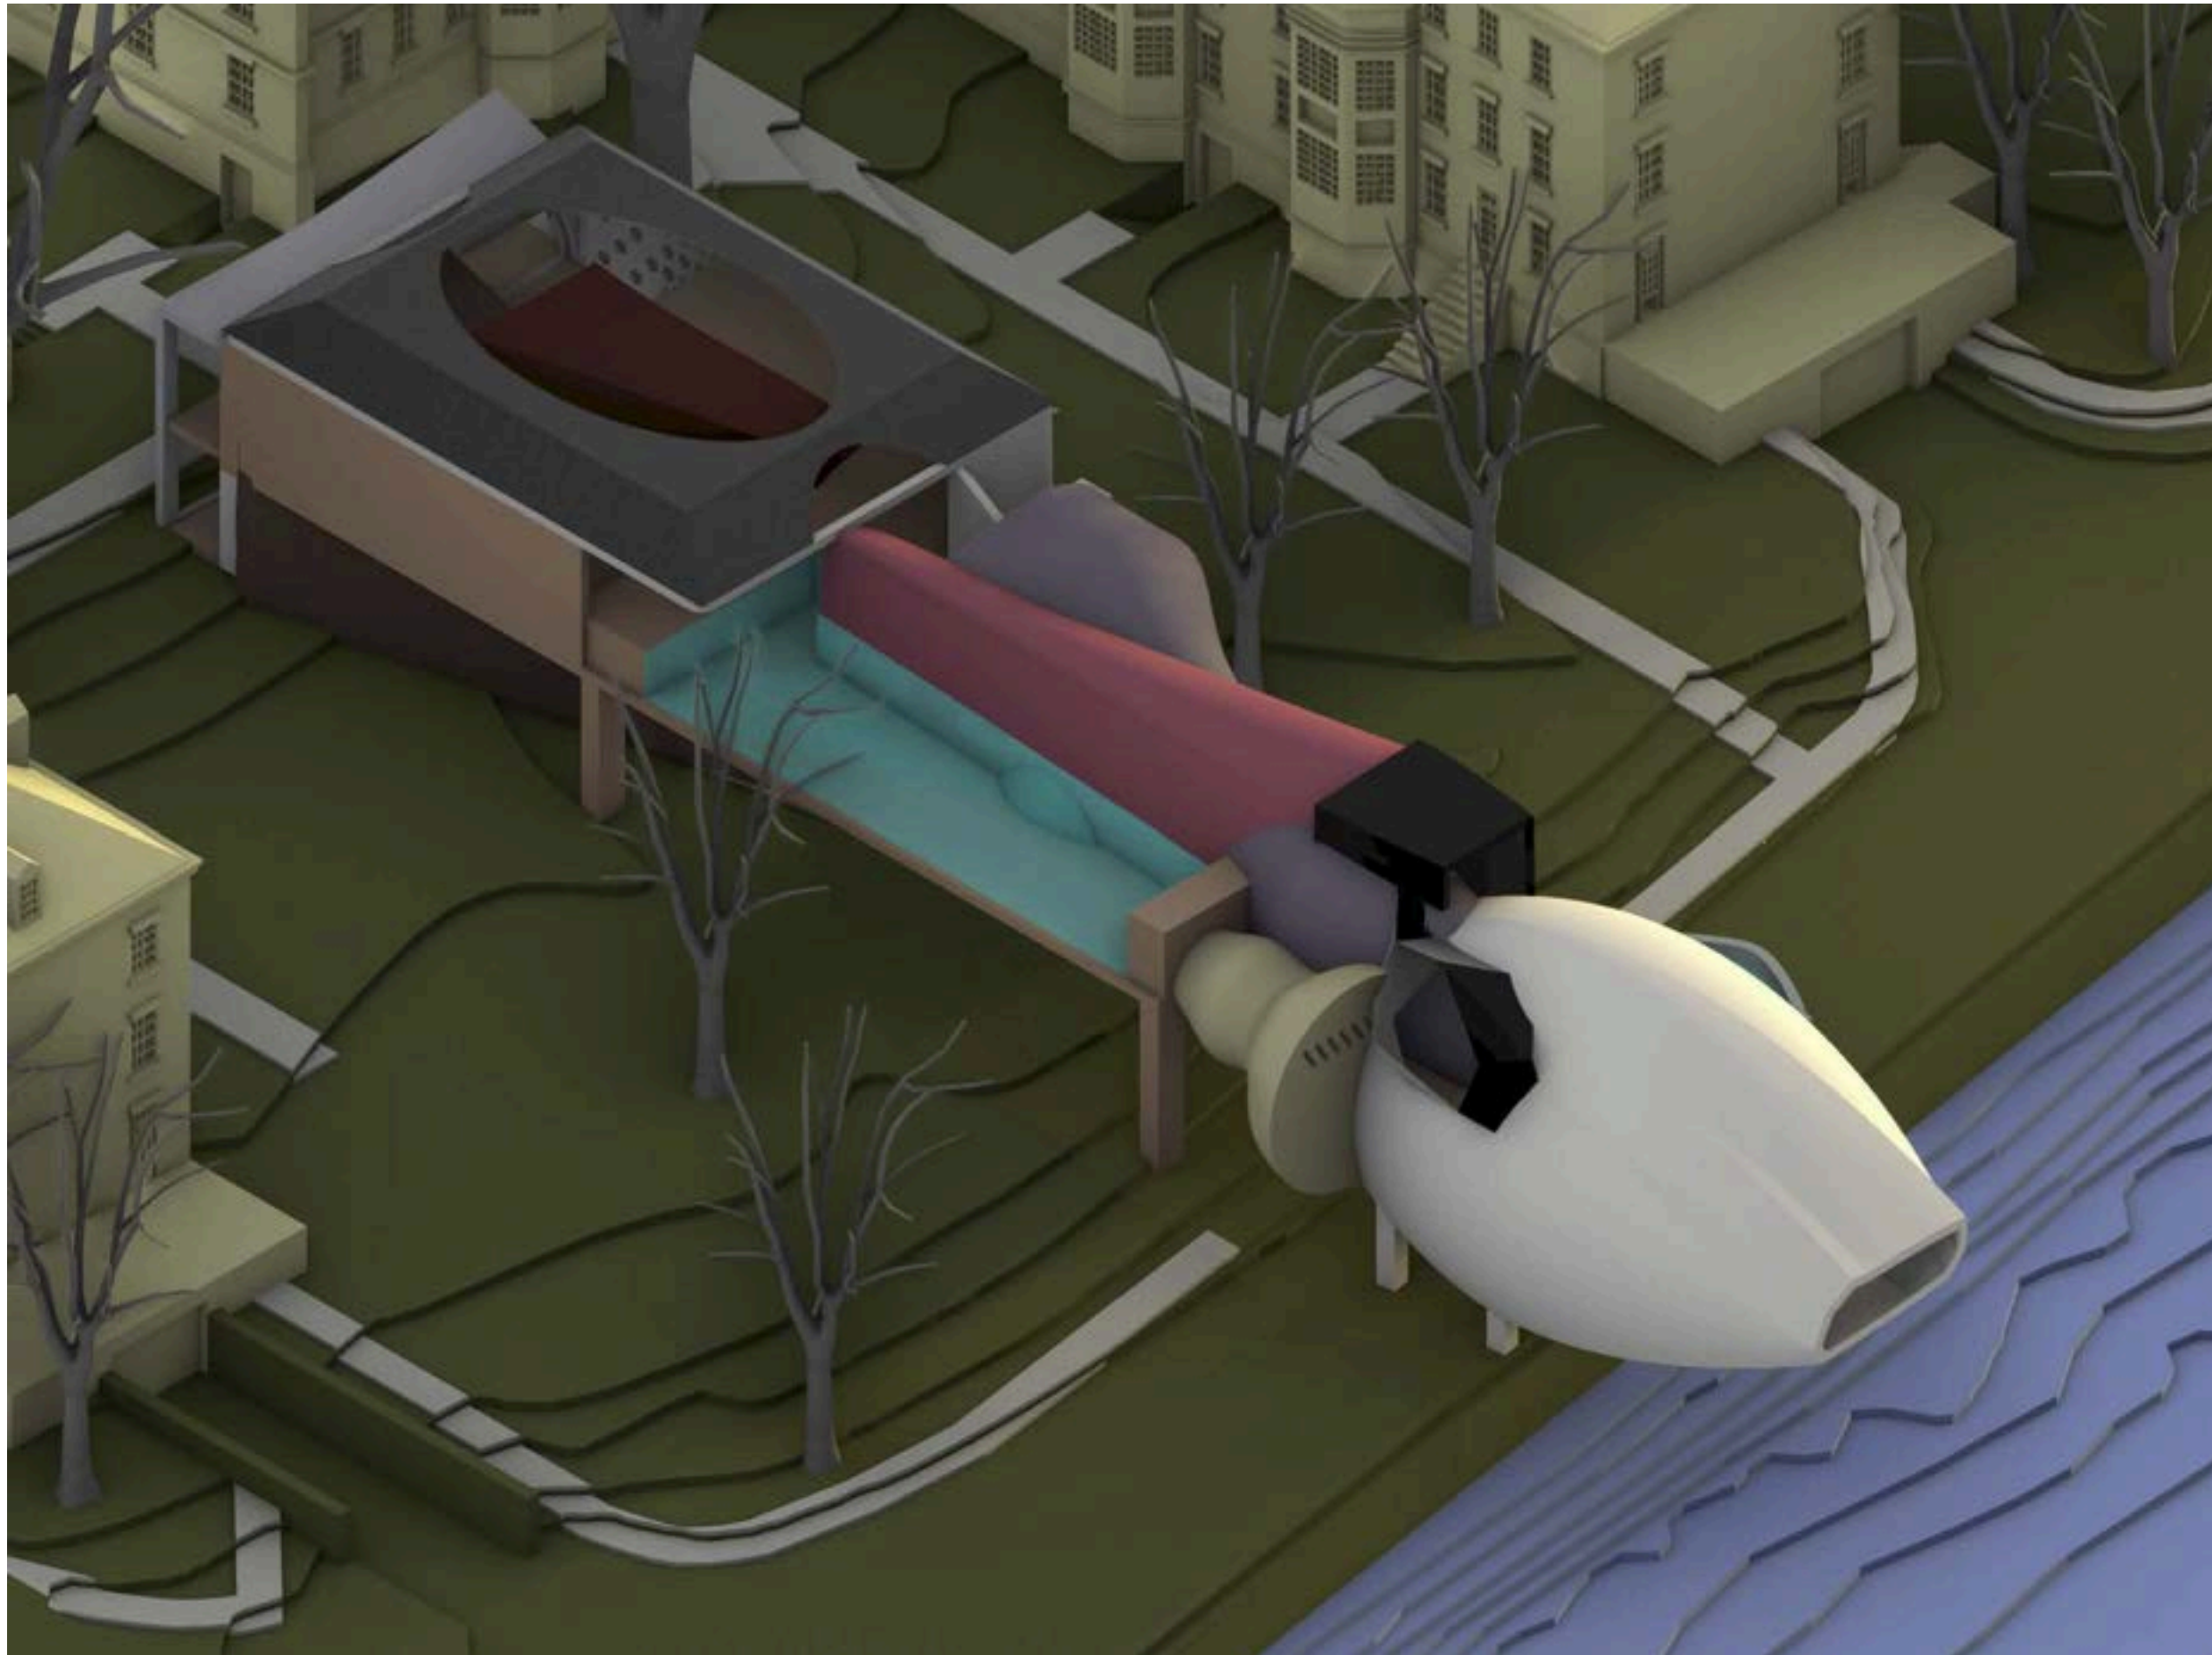

DIAGRAMS FINAL MODEL

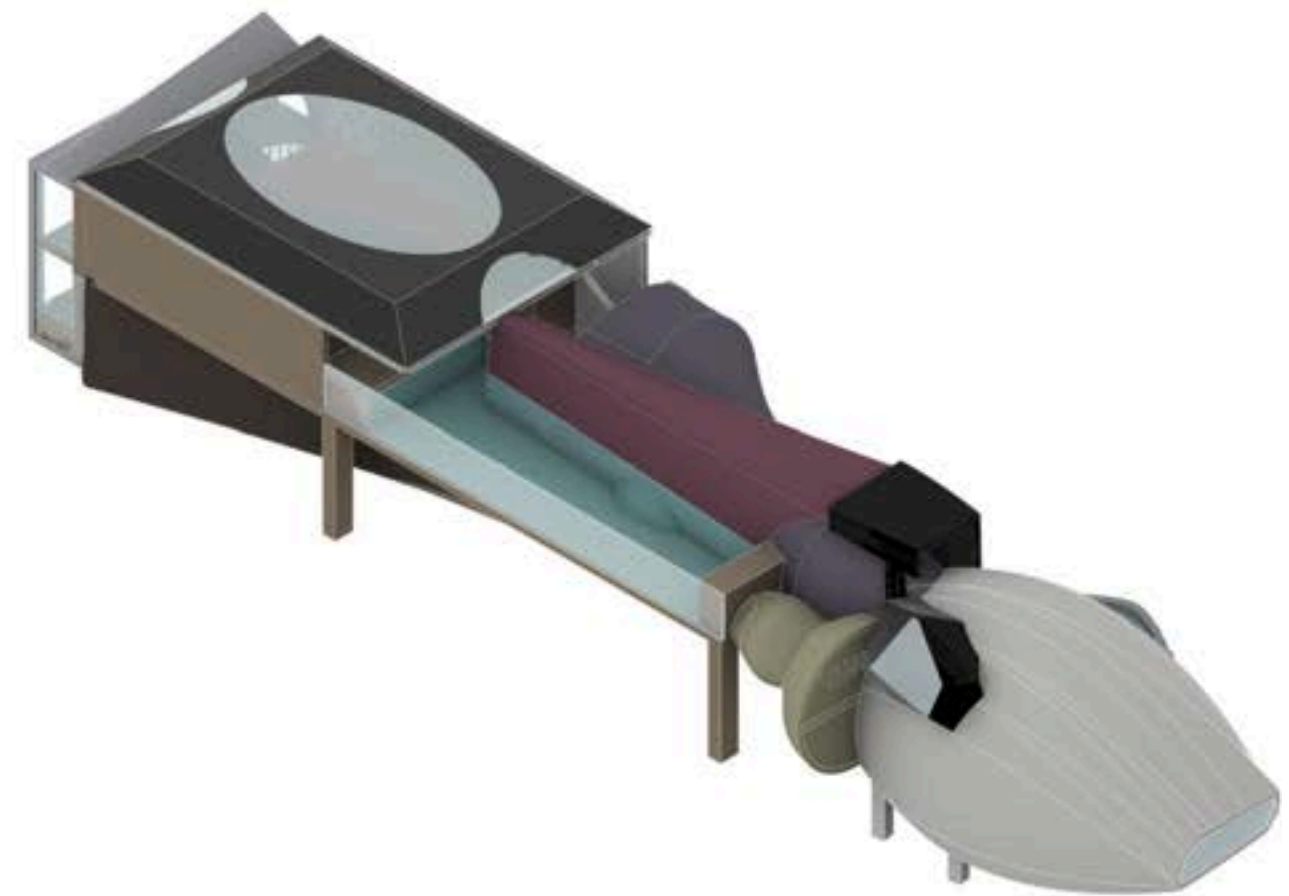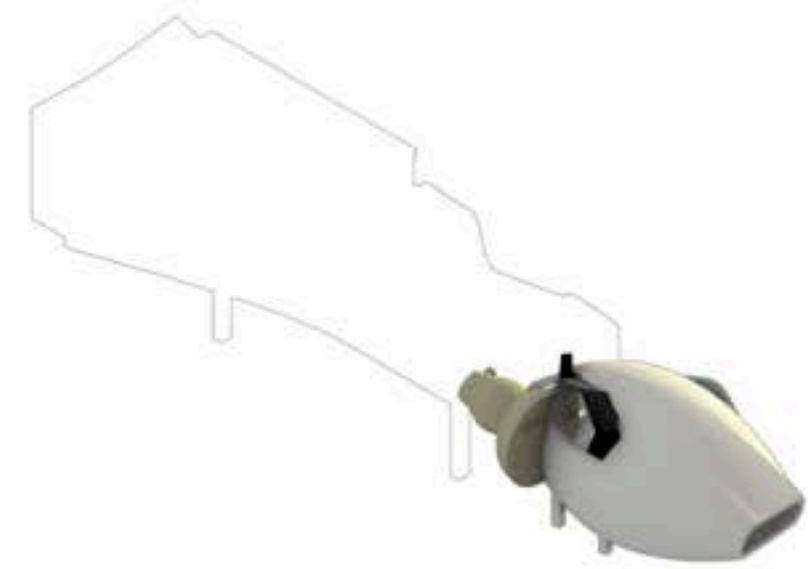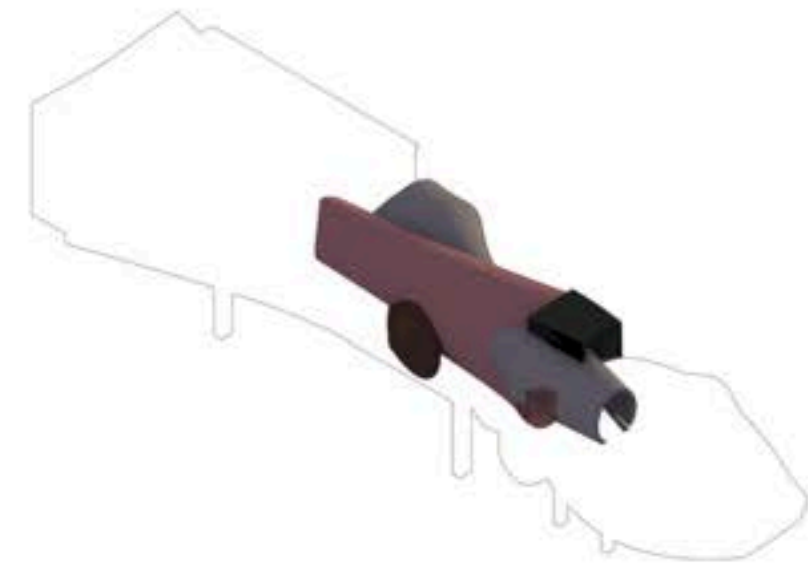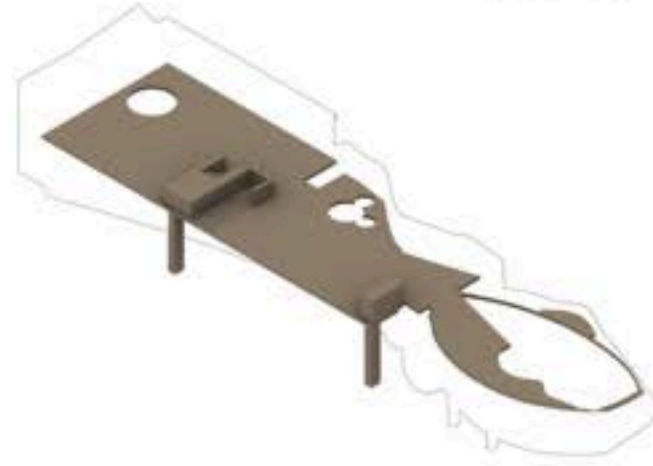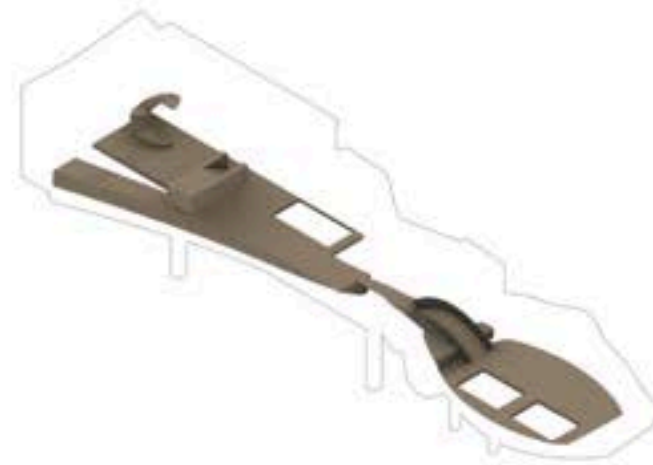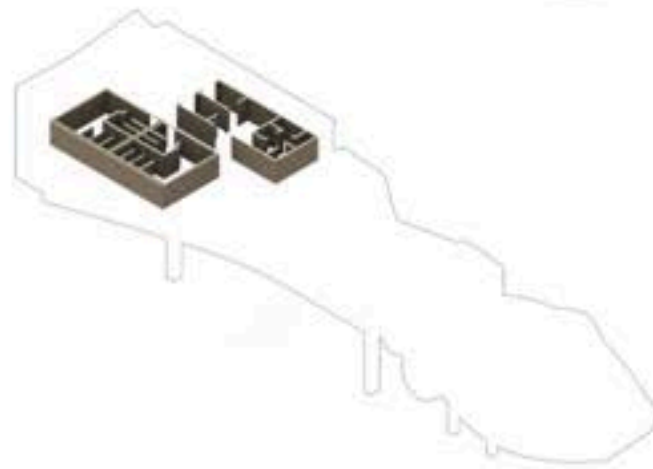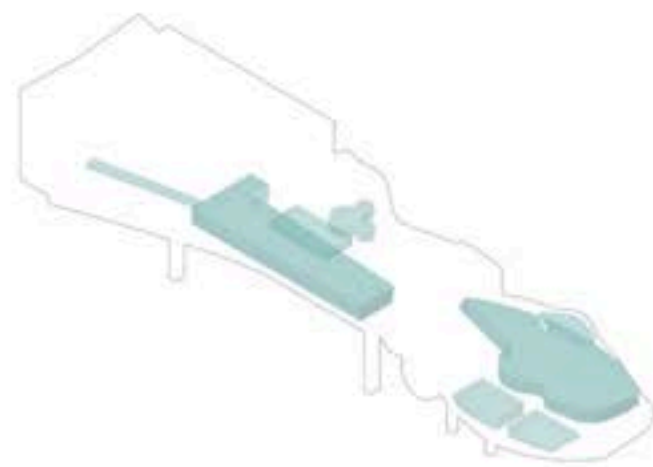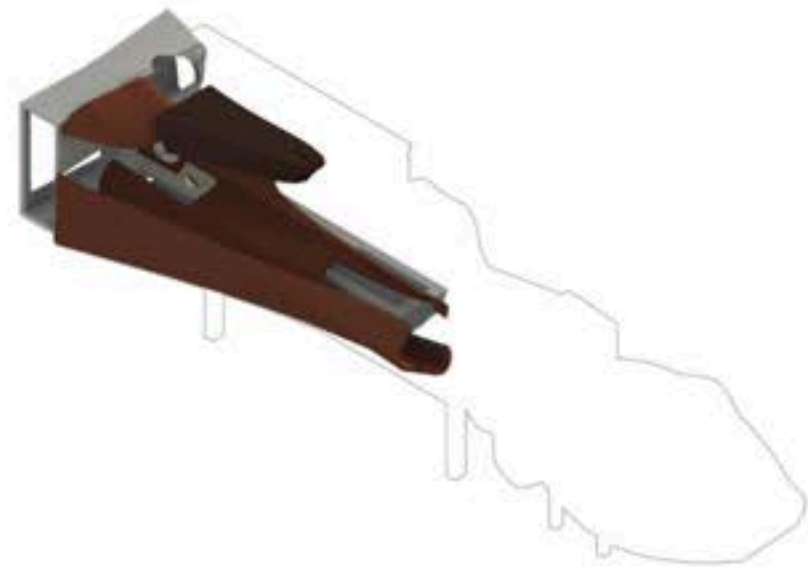



RENDERS

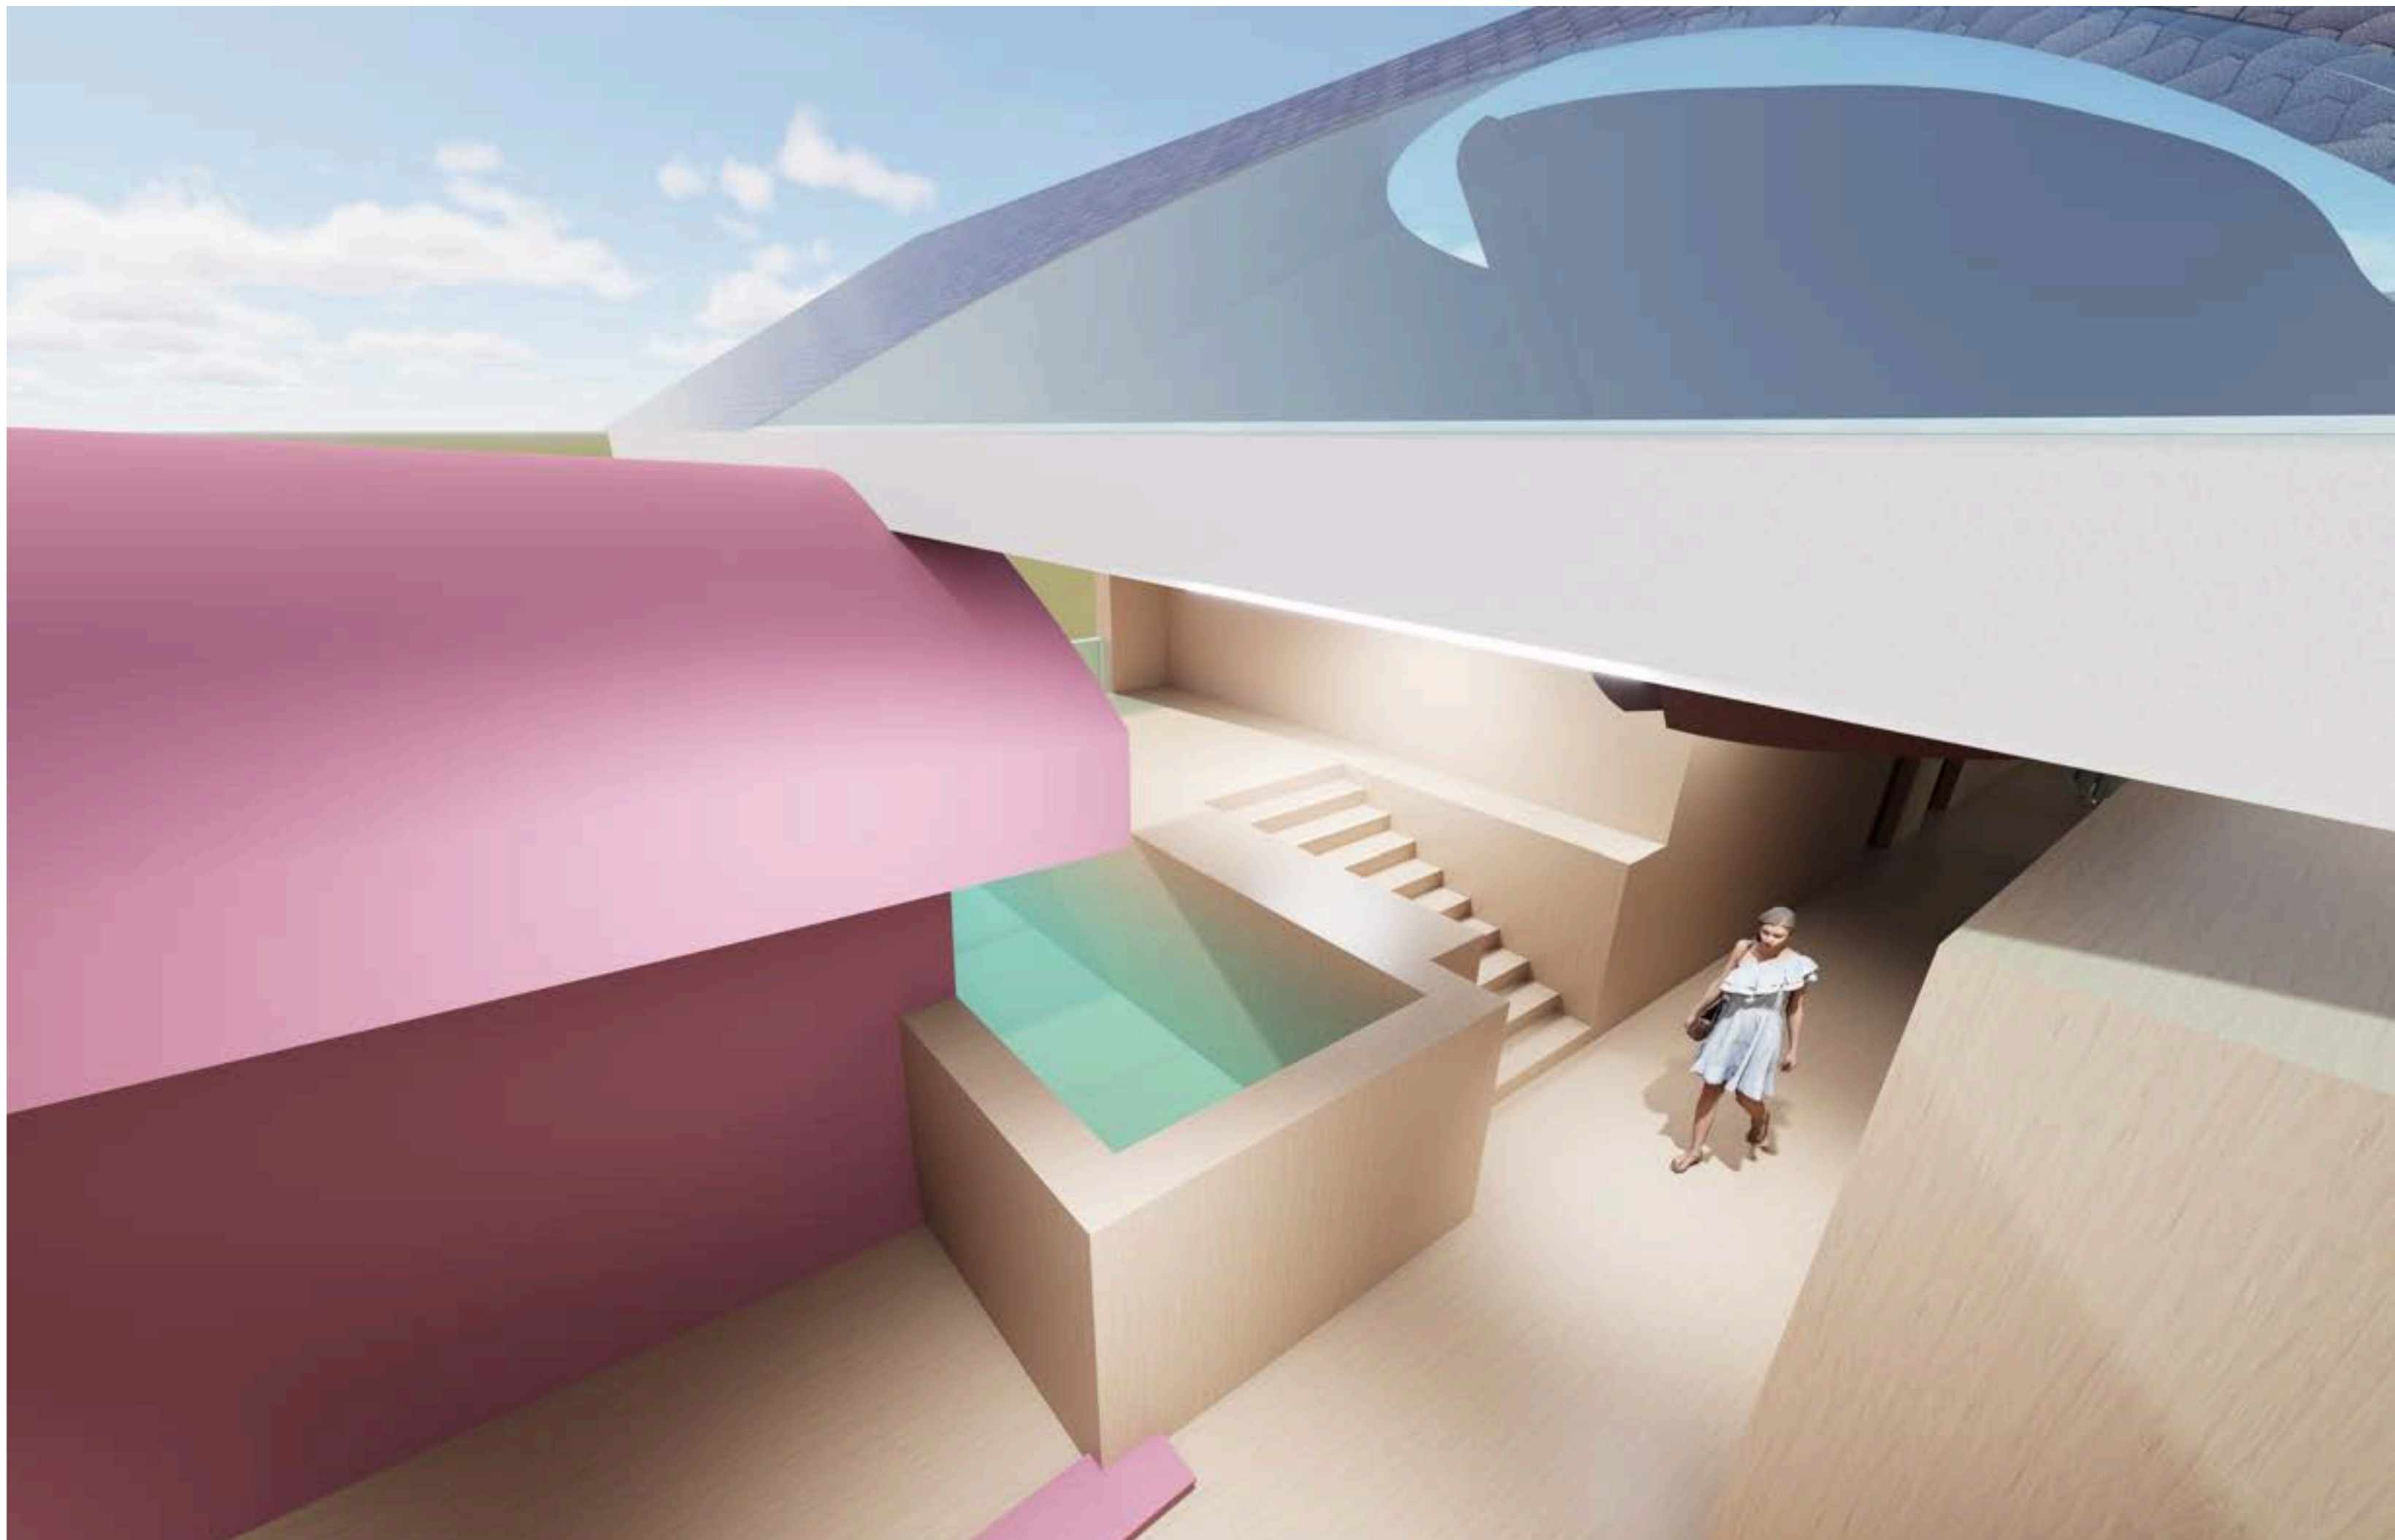






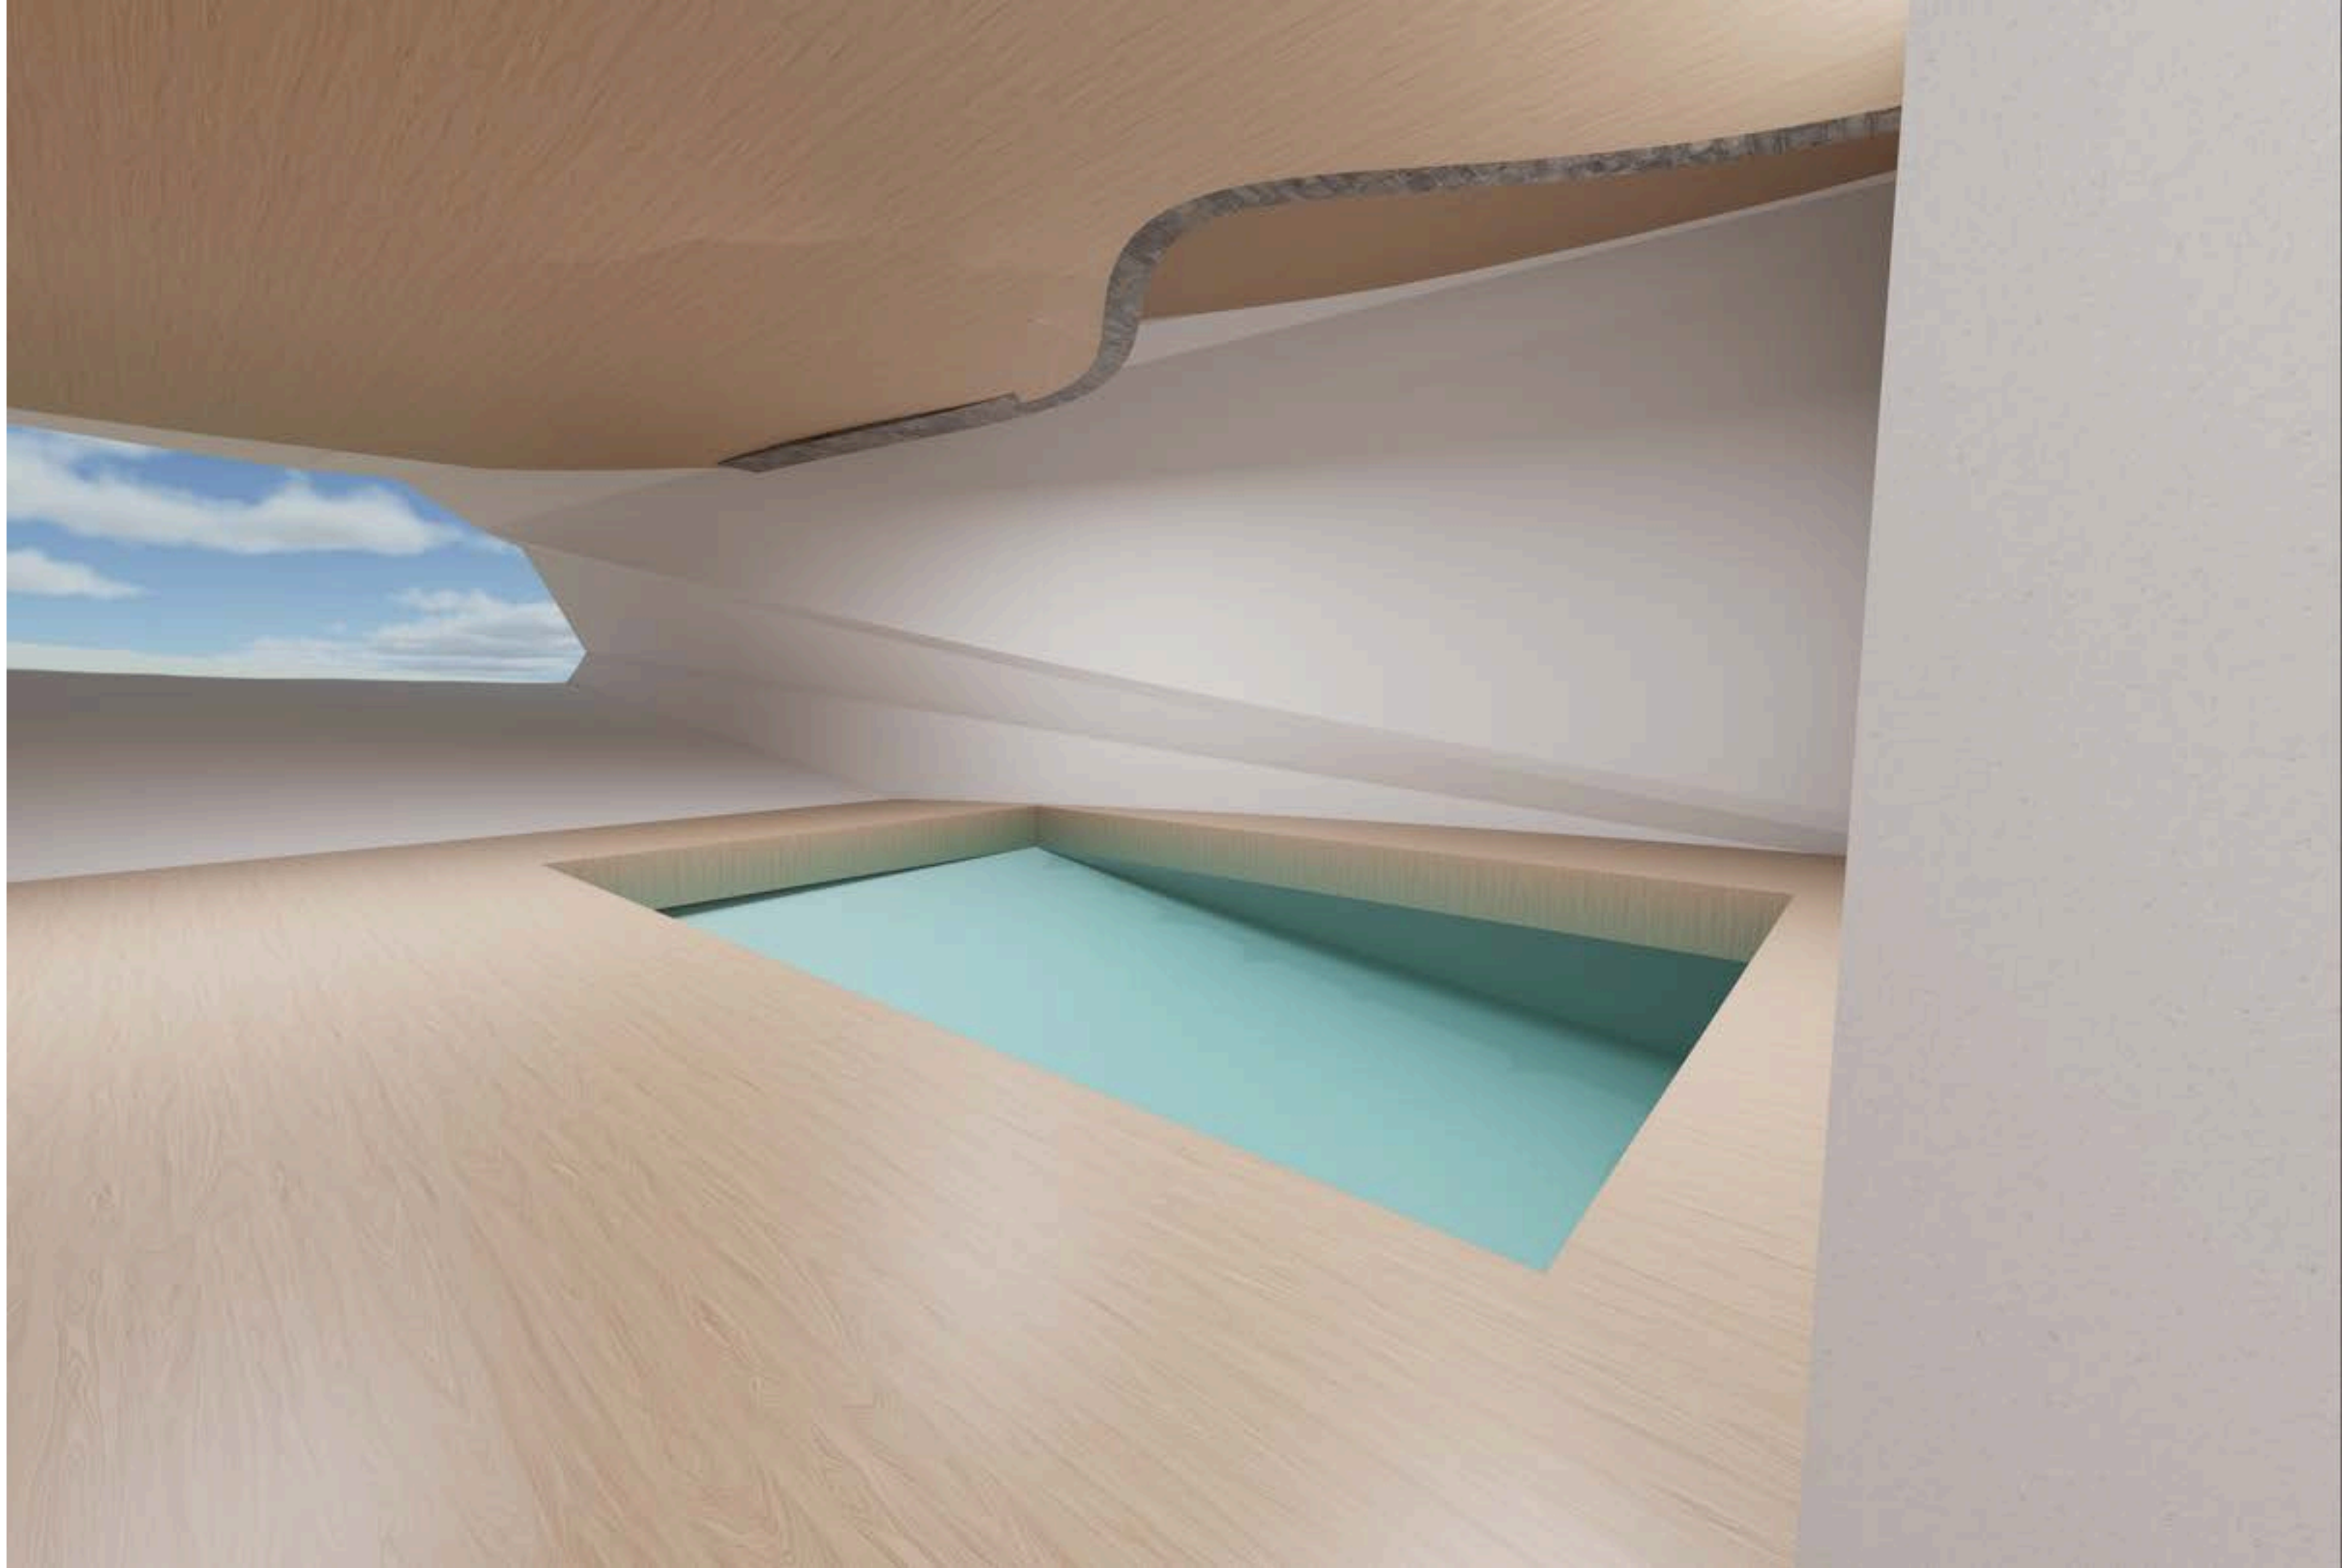

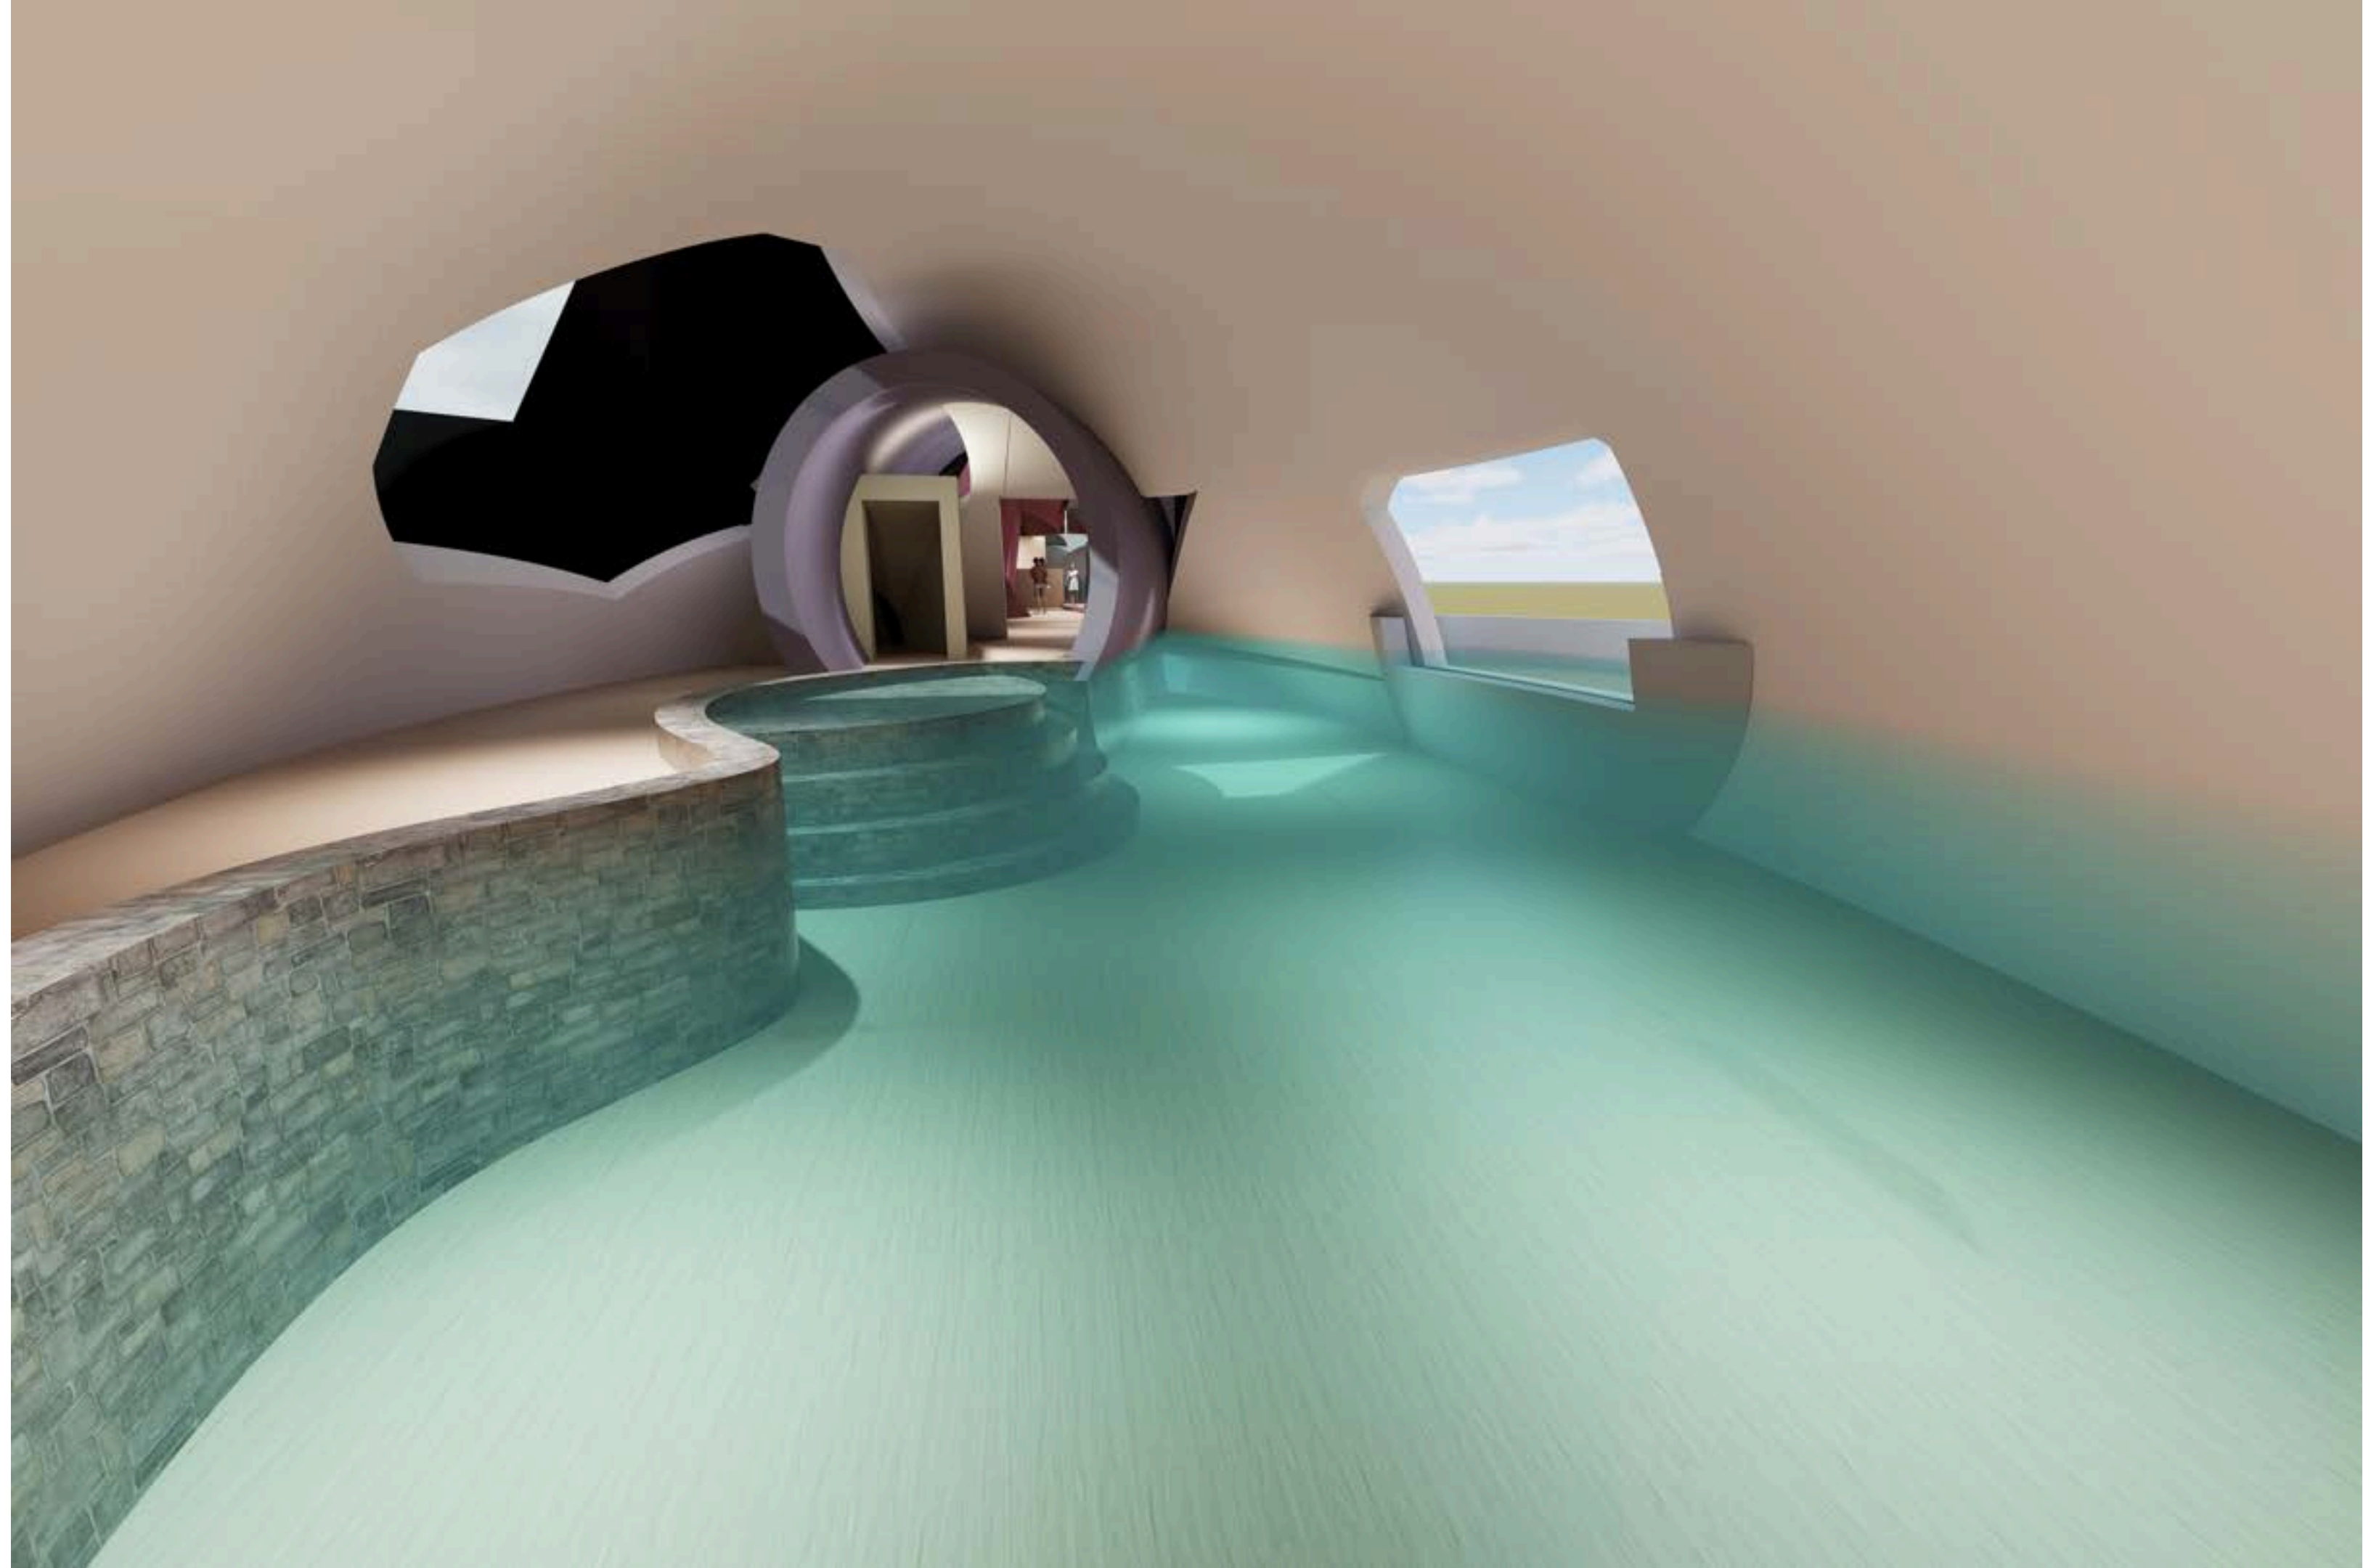


FINAL FLOOR PLANS


FIRST FLOOR

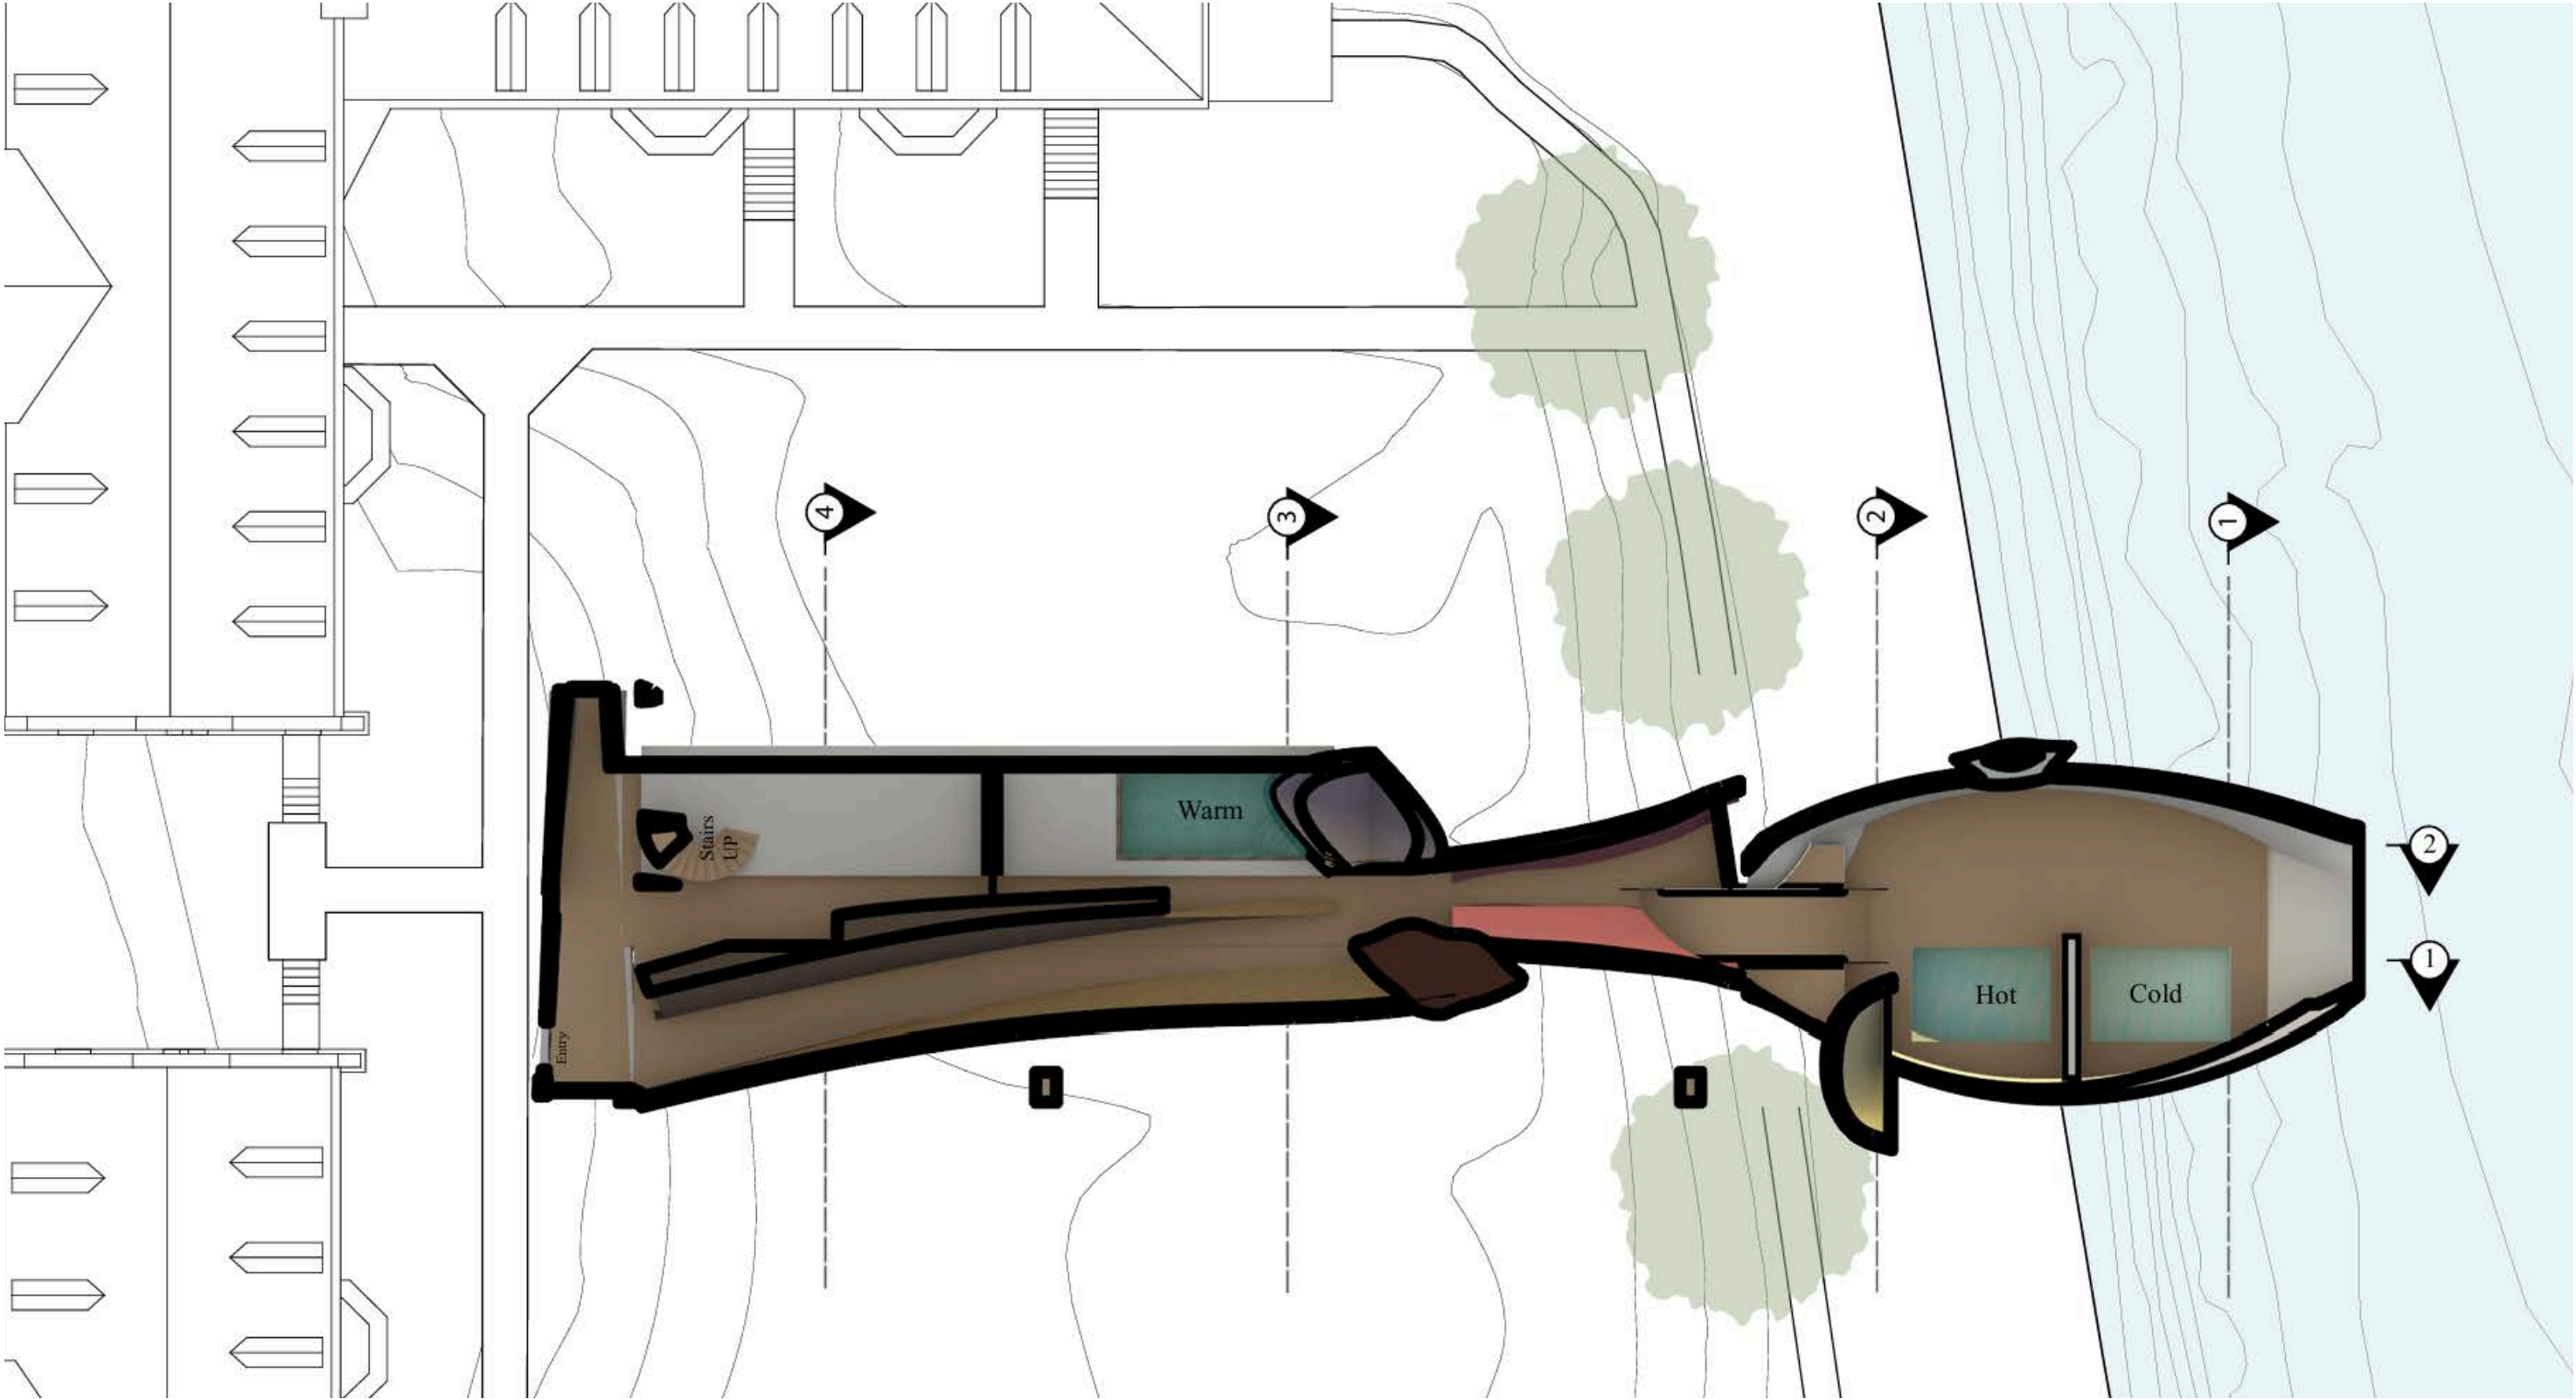



SECOND FLOOR

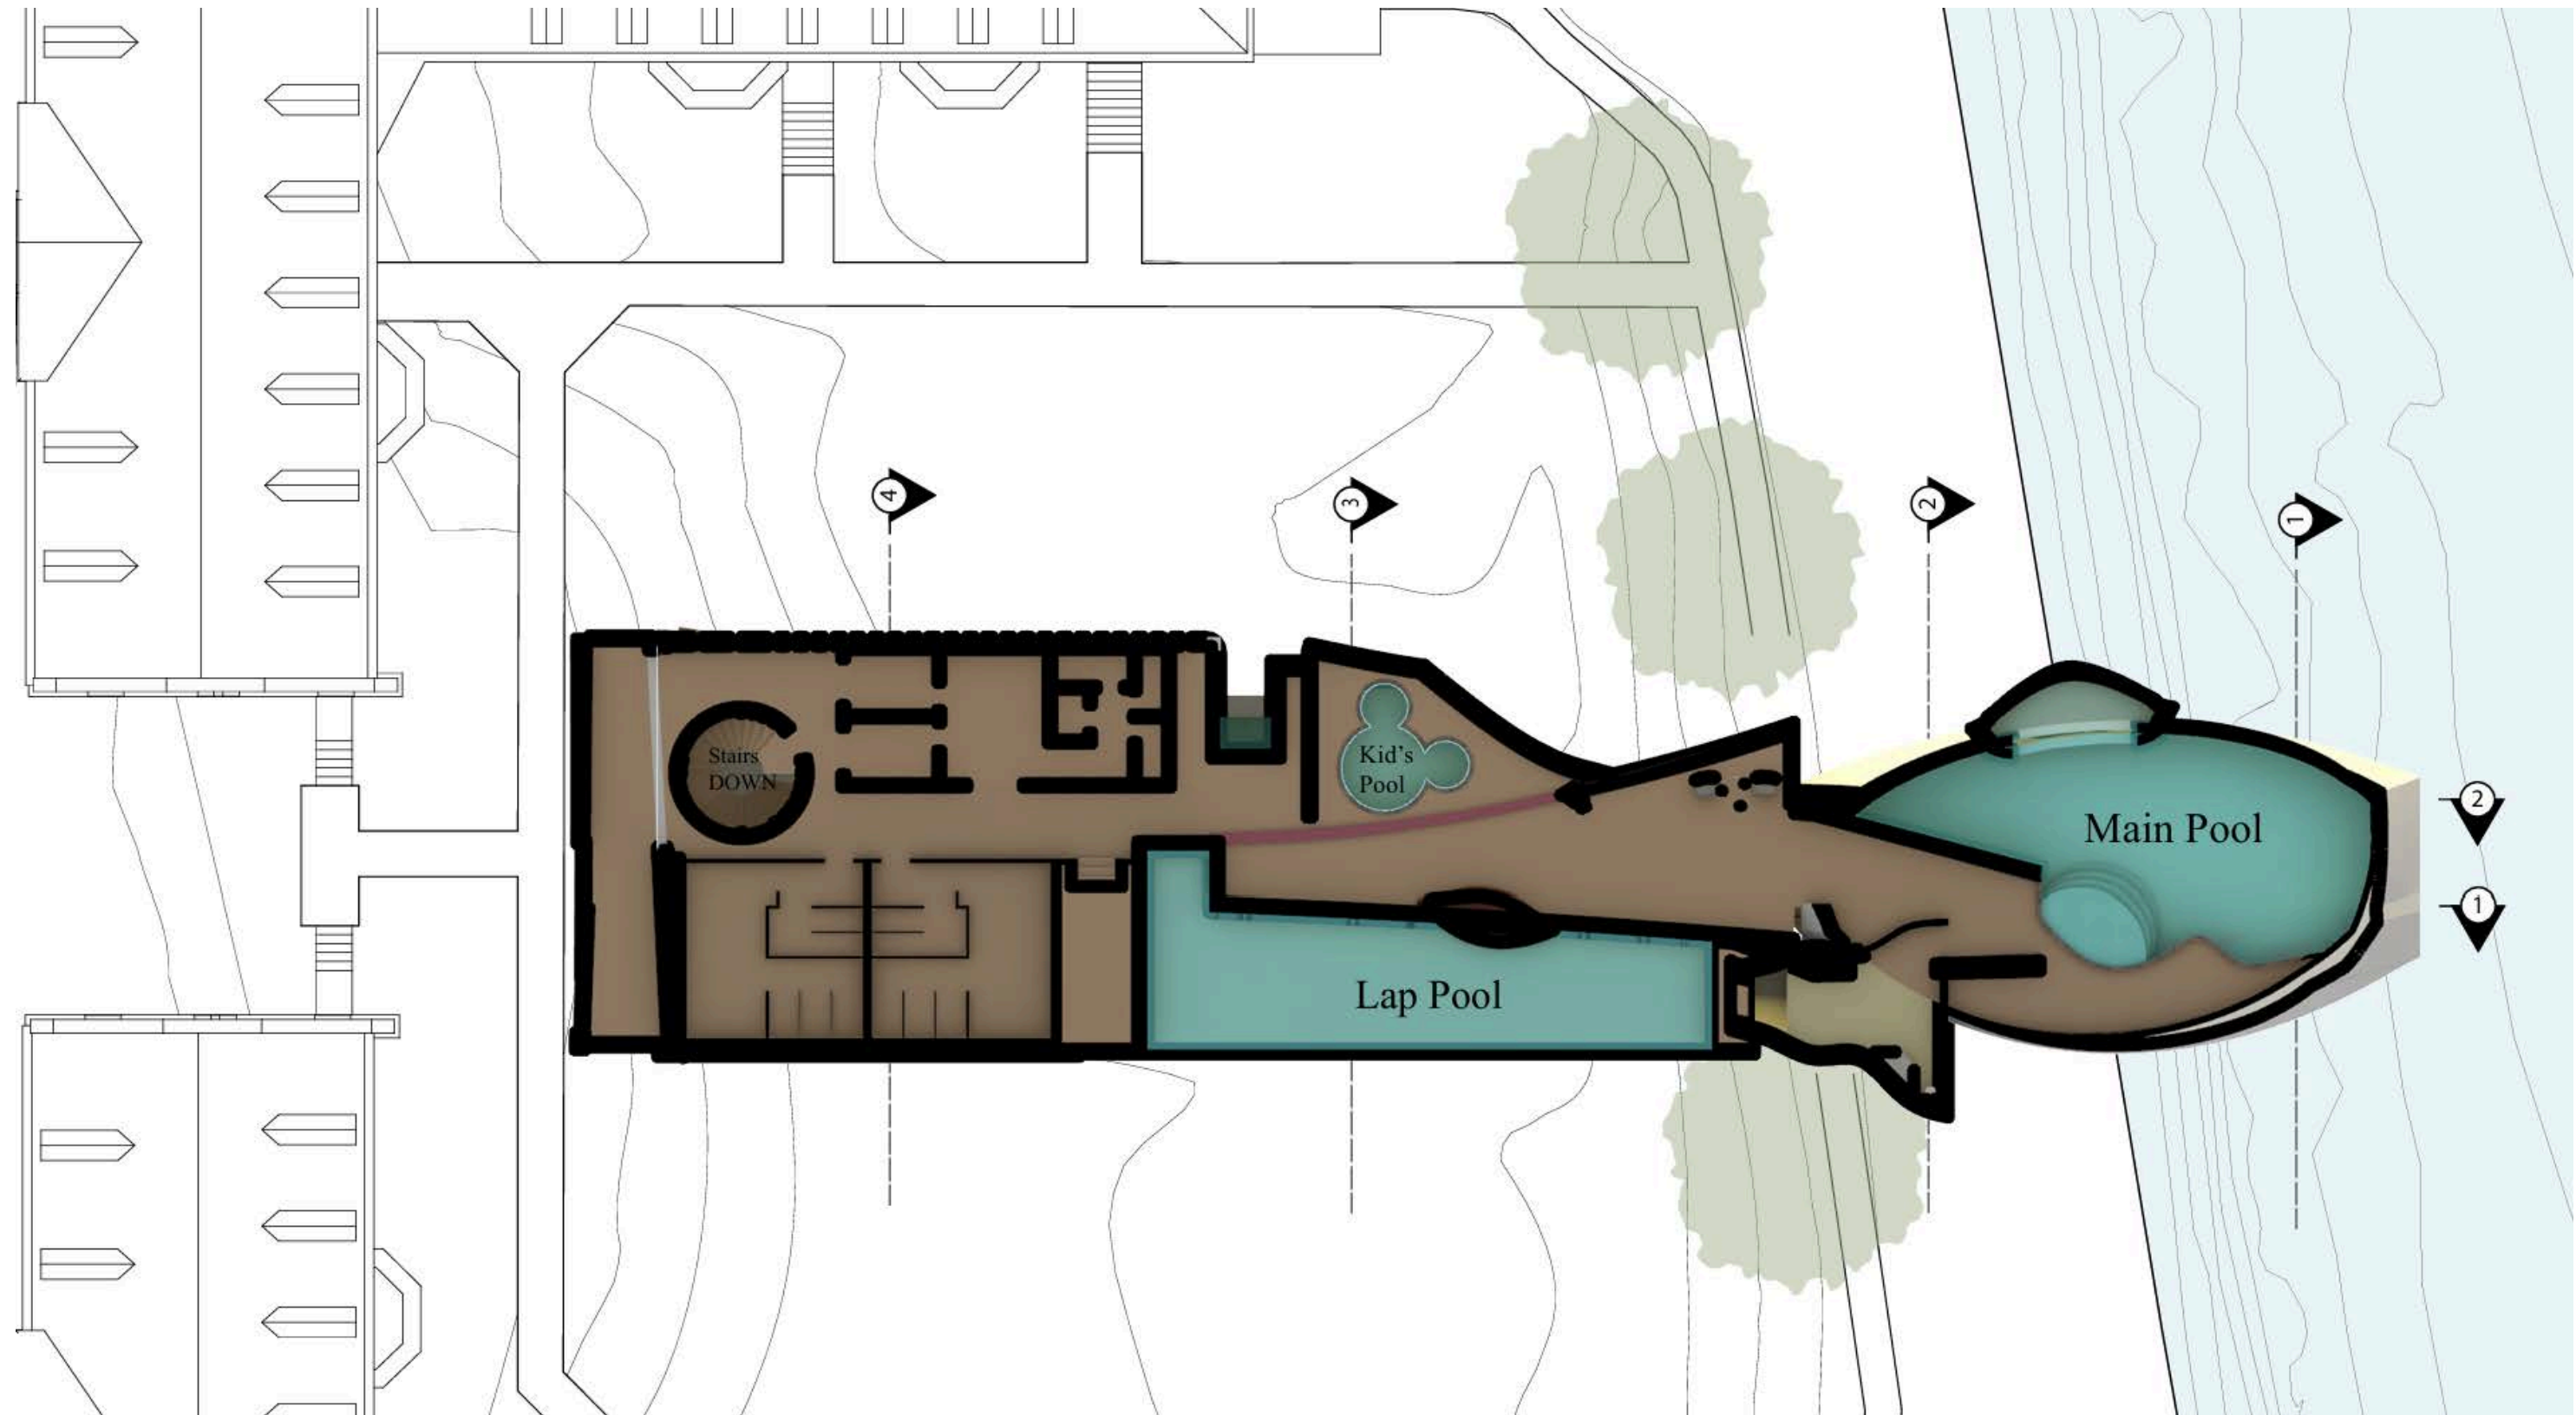


FINAL TRANSVERSES

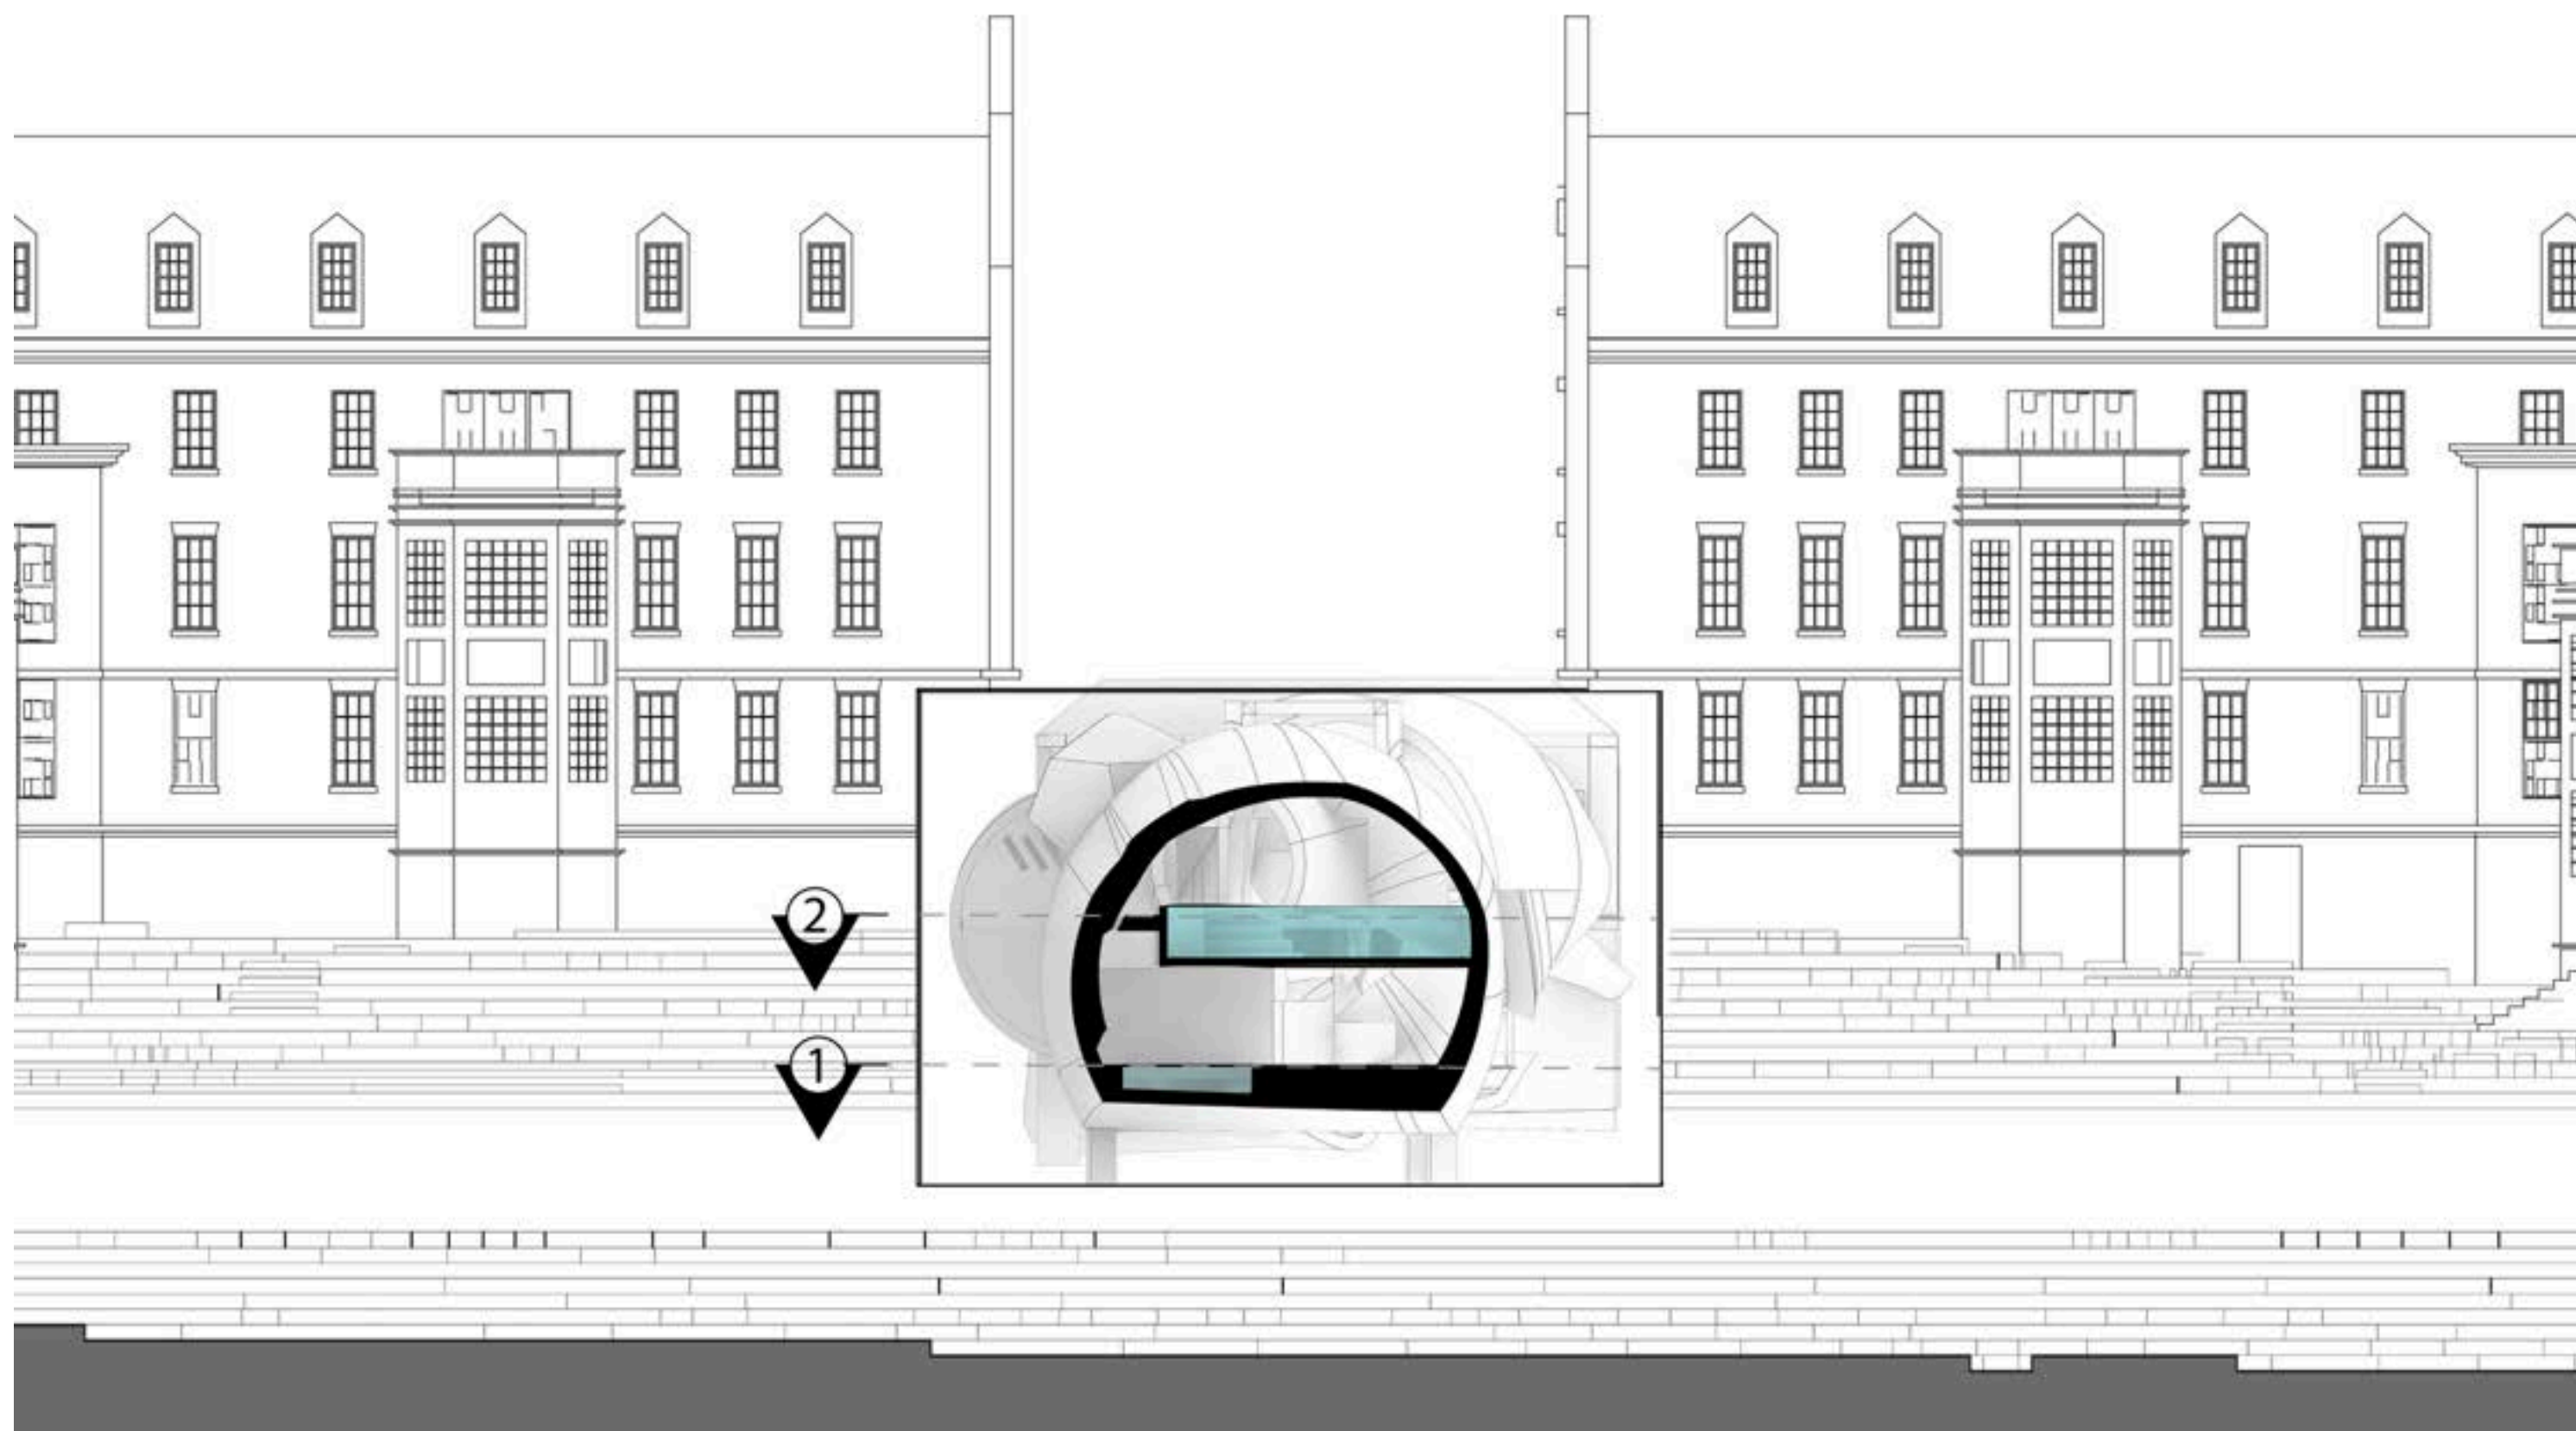

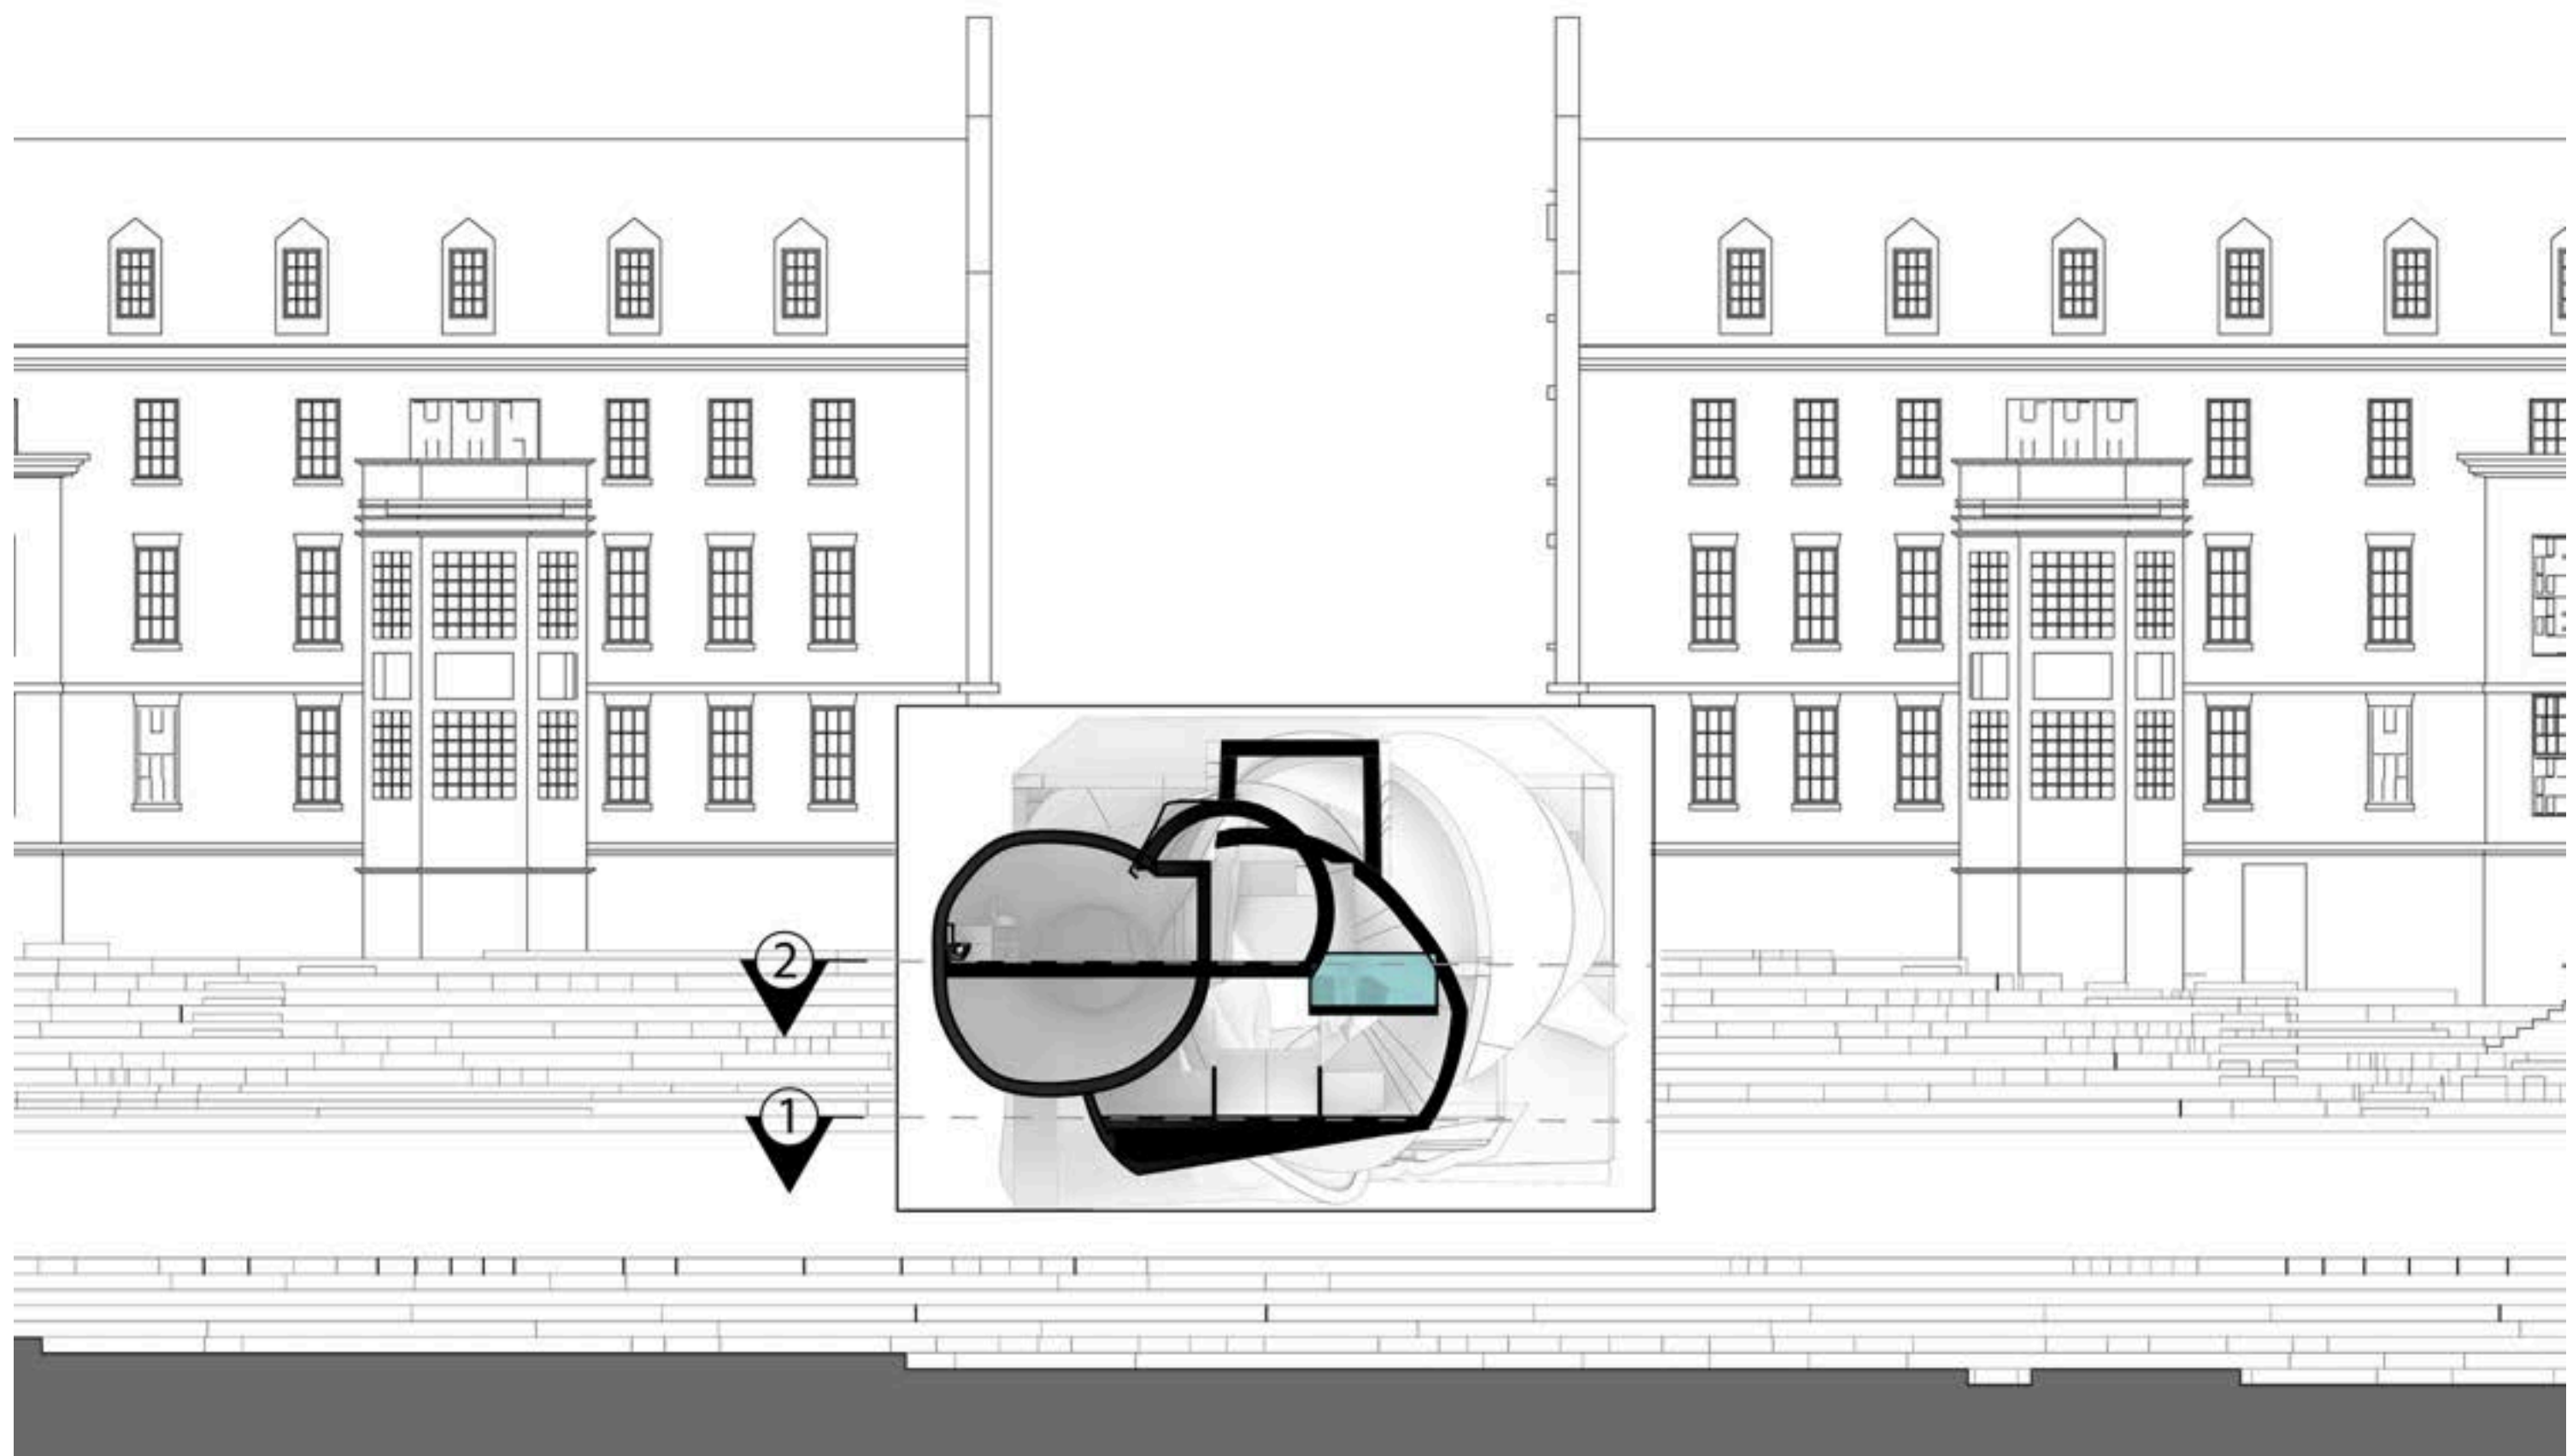

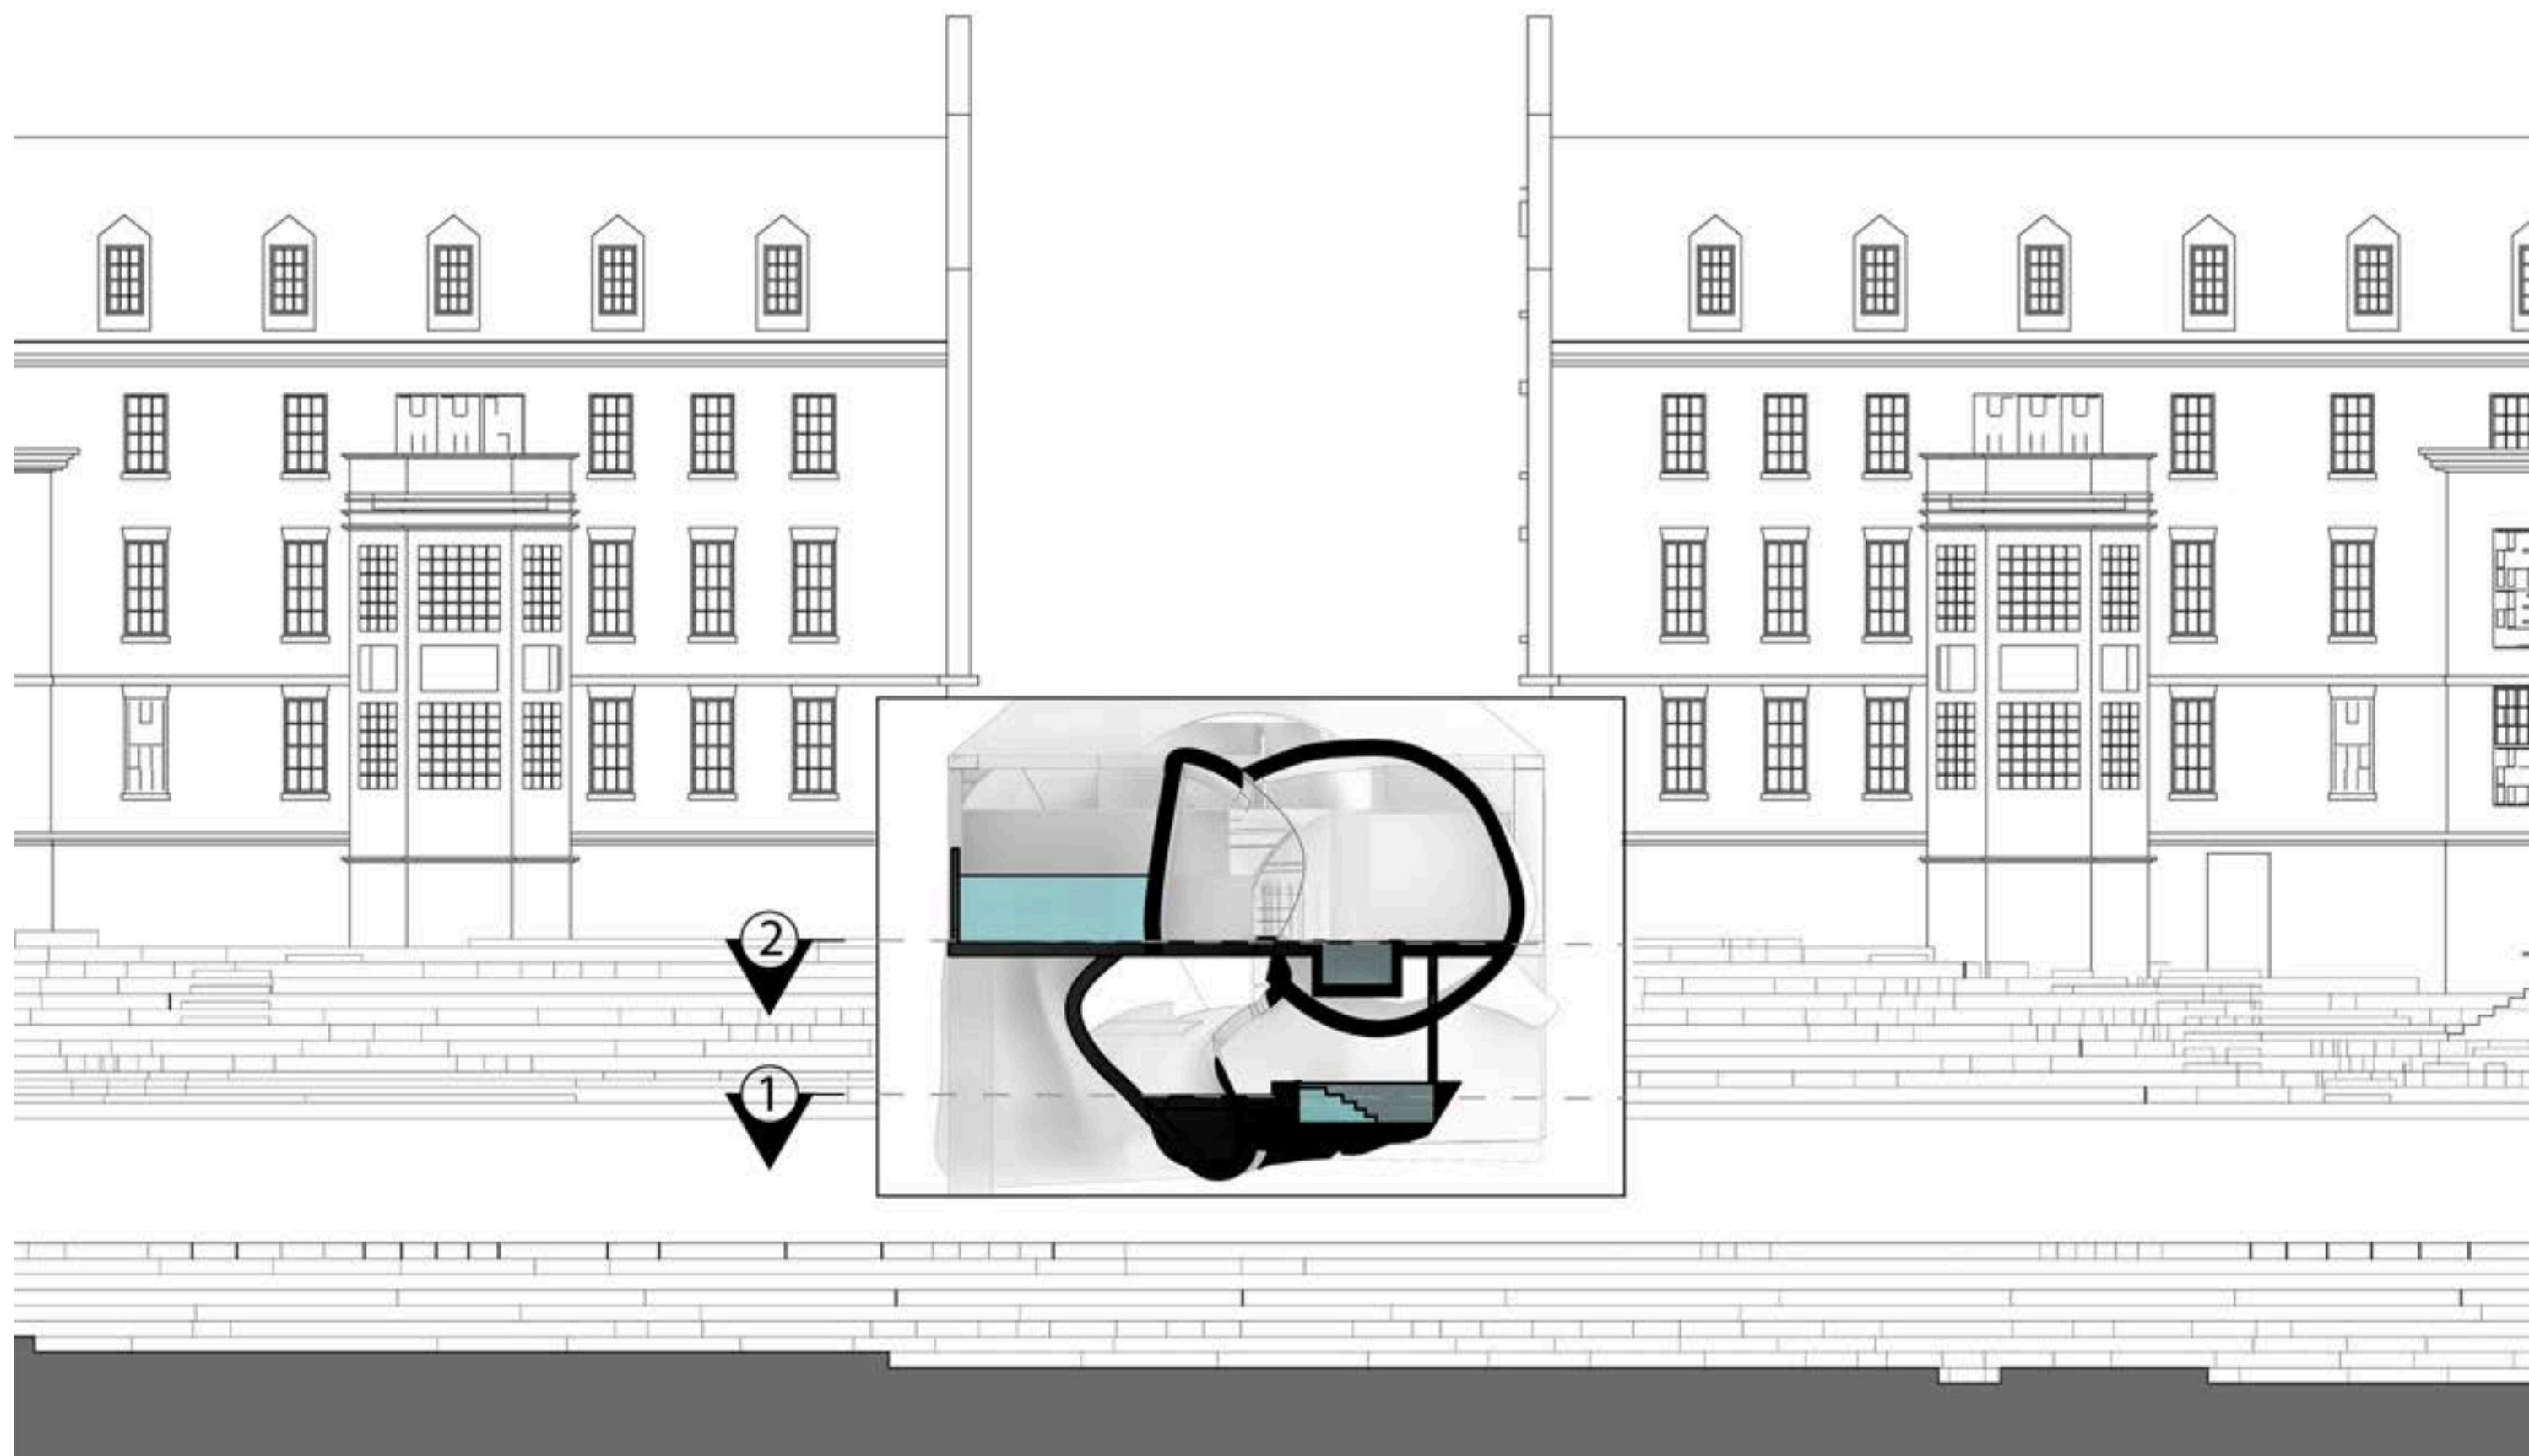

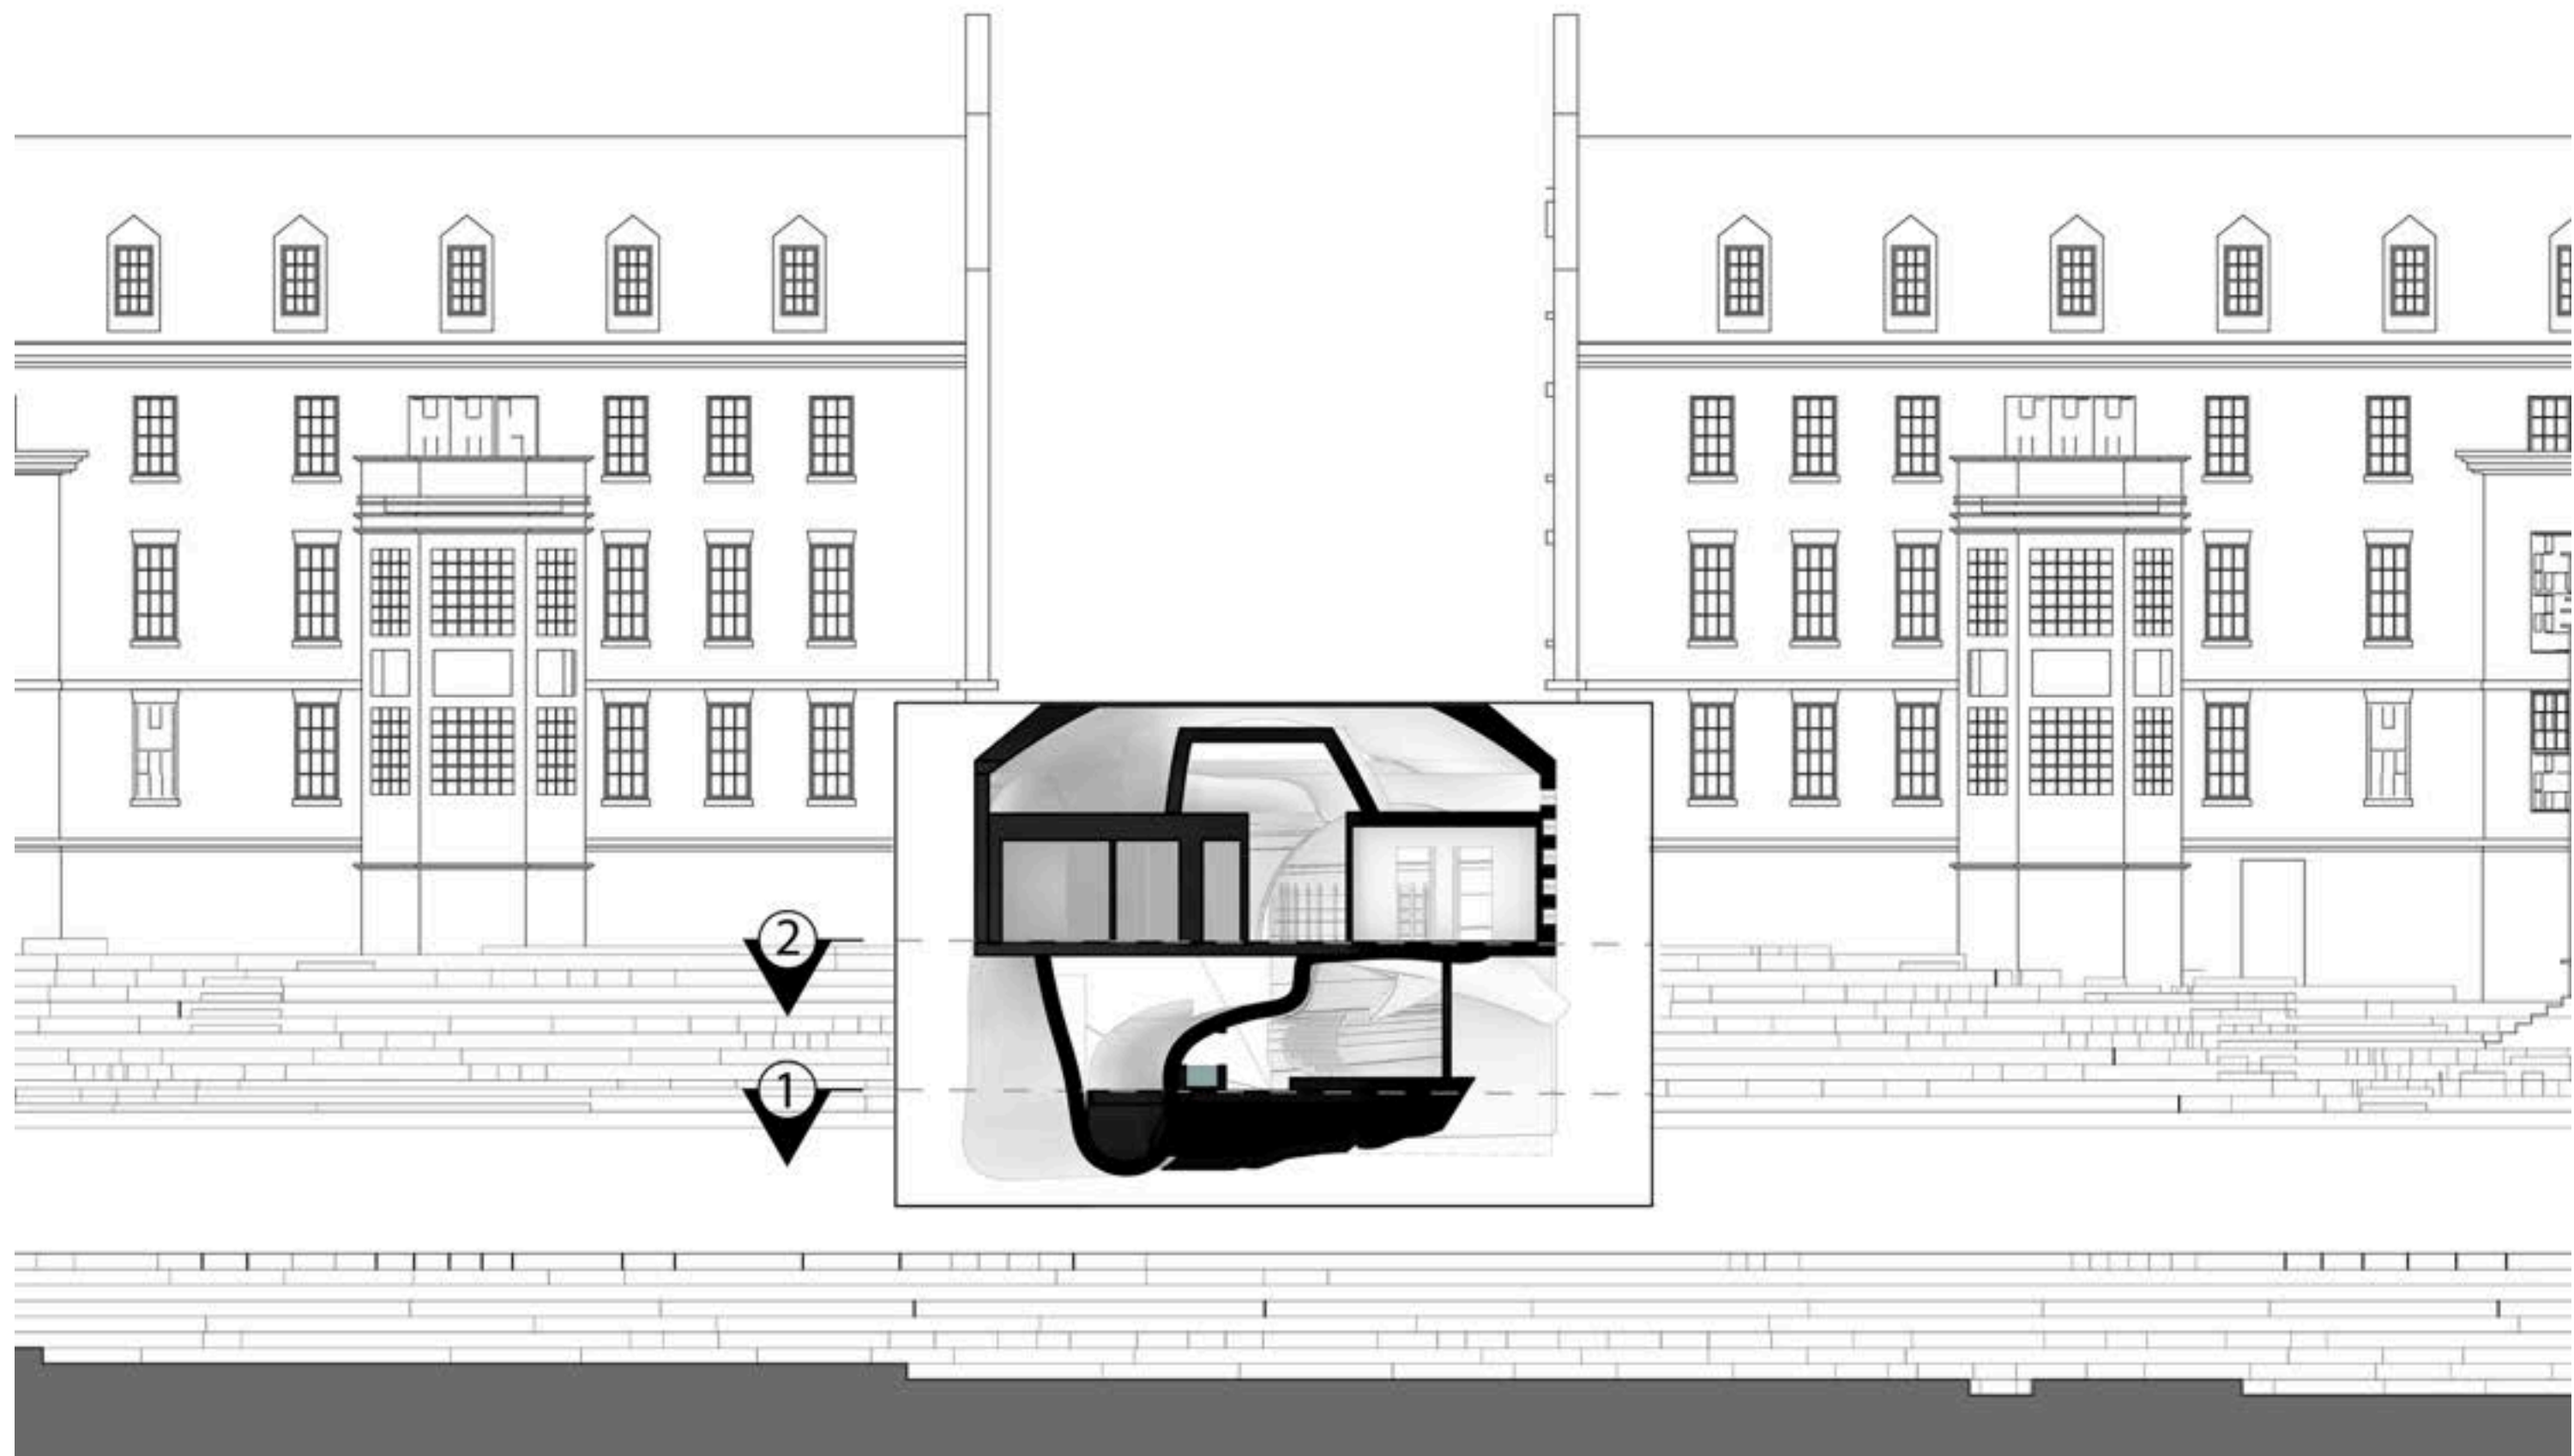

FINAL SECTIONS

